

PORTFOLIO

MOHAMED AYMAN

2023-2026
Maadi, Cairo, Egypt
mohamed.yman1152003@gmail.com



Junior Architect (Fresh Grad)

As an Architecture student at Ain Shams University, I'm driven by design, creativity, and exploration. Beyond academics, I engage in student activities and competitions, honing teamwork, leadership, and problem-solving skills.

Beyond Architecture learning I find inspiration in wandering the streets of Egypt, observing the layers of history, culture, and everyday life that shape the built environment. This exploration has deepened my appreciation for architecture and fueled my love for photography, allowing me to capture the essence of spaces and their stories.

Mohamed Ayman

Architecture Student

Cairo, Egypt

+20 01096107769

Mohamed.yman1152003@gmail.com

Behance.net

Linkedin.com

Education

SEP 2022- Present Student | Dept of Architecture | Ain Shams university, Cairo, Egypt

Experience

- SEP 2025

Snøhetta Master class 2nd edition.

Alexandria Library

- Selected among 35 students from over 650 applicants across Egypt to join the Snøhetta Masterclass at the Bibliotheca Alexandrina, led by Martin Gran.
- AUG 2025

Archigen Intern.

AI-driven architecture platform

-Hands-on with ComfyUI, developing custom workflows for generative architectural design.
- JUL 2025- AUG 2025

Architecture Intern.

ECG Consultants

- Working as a designer on making proposals for 2 buildings in (Libya & Egypt) and designing a parametric pattern on the elevation of a building in Kenya.
- SEP 2023- SEP 2025

Graphic design course instructor.

STP (Student Activity)

- Explaining photoshop ,Illustrator and Graphic design principles in Five sessions
- AUG2024- SEP2024

Architecture Intern.

ECG Consultants

-Contributed to Revit-based technical drawings for a school project in NEOM, Saudi Arabia.
- SEP 2022- AUG 2023

Member at Graphic design team.

STP (Student Activity)

- Working on online and offline campaigns

COMPETITIONS

- AUG 2025

First Place.

Egypt Urban Oasis competition.
- MAY 2025

First Place.

Beyond The Tide | Smart System design studio
- MAY 2025

Second Place.

Floating houses | World Architecture Competition
- AUG 2024

Honorable mention (Top 10).

Tamayouz Award | Dewan Award for Architecture
- JAN 2024

Honorable mention.

Ainshams University Rebranding
- JUL 2026

In progress.

Midar Library competition.
- MAR 2025

Participation.

120 Hours competition.
- JUN 2024

Participation.

Genius Loci 4 | De-lab
- JAN 2023

Participation.

Visual Identity for Cairo Governorate
- JAN 2026

Participation

Al Fozan Award | Islamic Center – Turku, Finland

Softwares

3ds Max, Revit, Rhino, Grasshopper, AutoCAD, Lumion, Adobe Suite, Chaos Corona, SketchUp

Soft Skills

Exploring Streets, Graphic Design, Presentation Skills, Time Management

CONTENTS

1.	RENILE Research center Graduation project	2
2.	ROSETTA Hotel Academic work	10
3.	MIDAAR LIBRARY Library Competition	14
4.	AL-GHEYYA Culture center Competition	19
5.	Wesal Pavilion Competition	22
6.	THE FLUX Interior design Academic work	24
7.	THE CAUSTIC Smart Chalets Competition	26
8.	Ehyaa Community Center Academic work	29
9.	A Journey for Discovery Photography Passion	32



1

RENILE

ACADEMIC WORK

GRADUATION PROJECT

Ain Shams University, Faculty of Engineering

Year: 2026

Location: Tushka, Egypt

Project: Hotel

Softwares: Rhino, 3Ds Max, Corona, Photoshop, Illustrator

Role: (Individual)

CONCEPT

“The Dialogue” is not merely a title — it is the essence of this architectural narrative. The project embodies the unique conversation between land and sea, between structure and flow, between the contained (indoor) and the limitless (outdoor). Inspired by Rashid’s unique geographical and historical context — where the Nile and Mediterranean meet — the design draws from this natural confluence, creating a fluid form that extends bridges out into the landscape, just as the Nile stretches into the sea

PROBLEM DEFINITION

1



NATIONAL VISION – 1997
National mega-project announced.

2



CANAL COMPLETED– 2003
Water reached Toshka through the Sheikh Zayed Canal.

3



SLOW PROGRESS– 2005
Development fell behind expectations.

4



PROJECT FAILURE– 2015
Widely considered an unsuccessful national project.

5



CANAL COMPLETED– 2003
Government relaunched and expanded the project.




6




THE NEW ERA– 2150
Smart Nile systems • Sustainability • Food Security




USER SCENARIO
PUBLIC USER

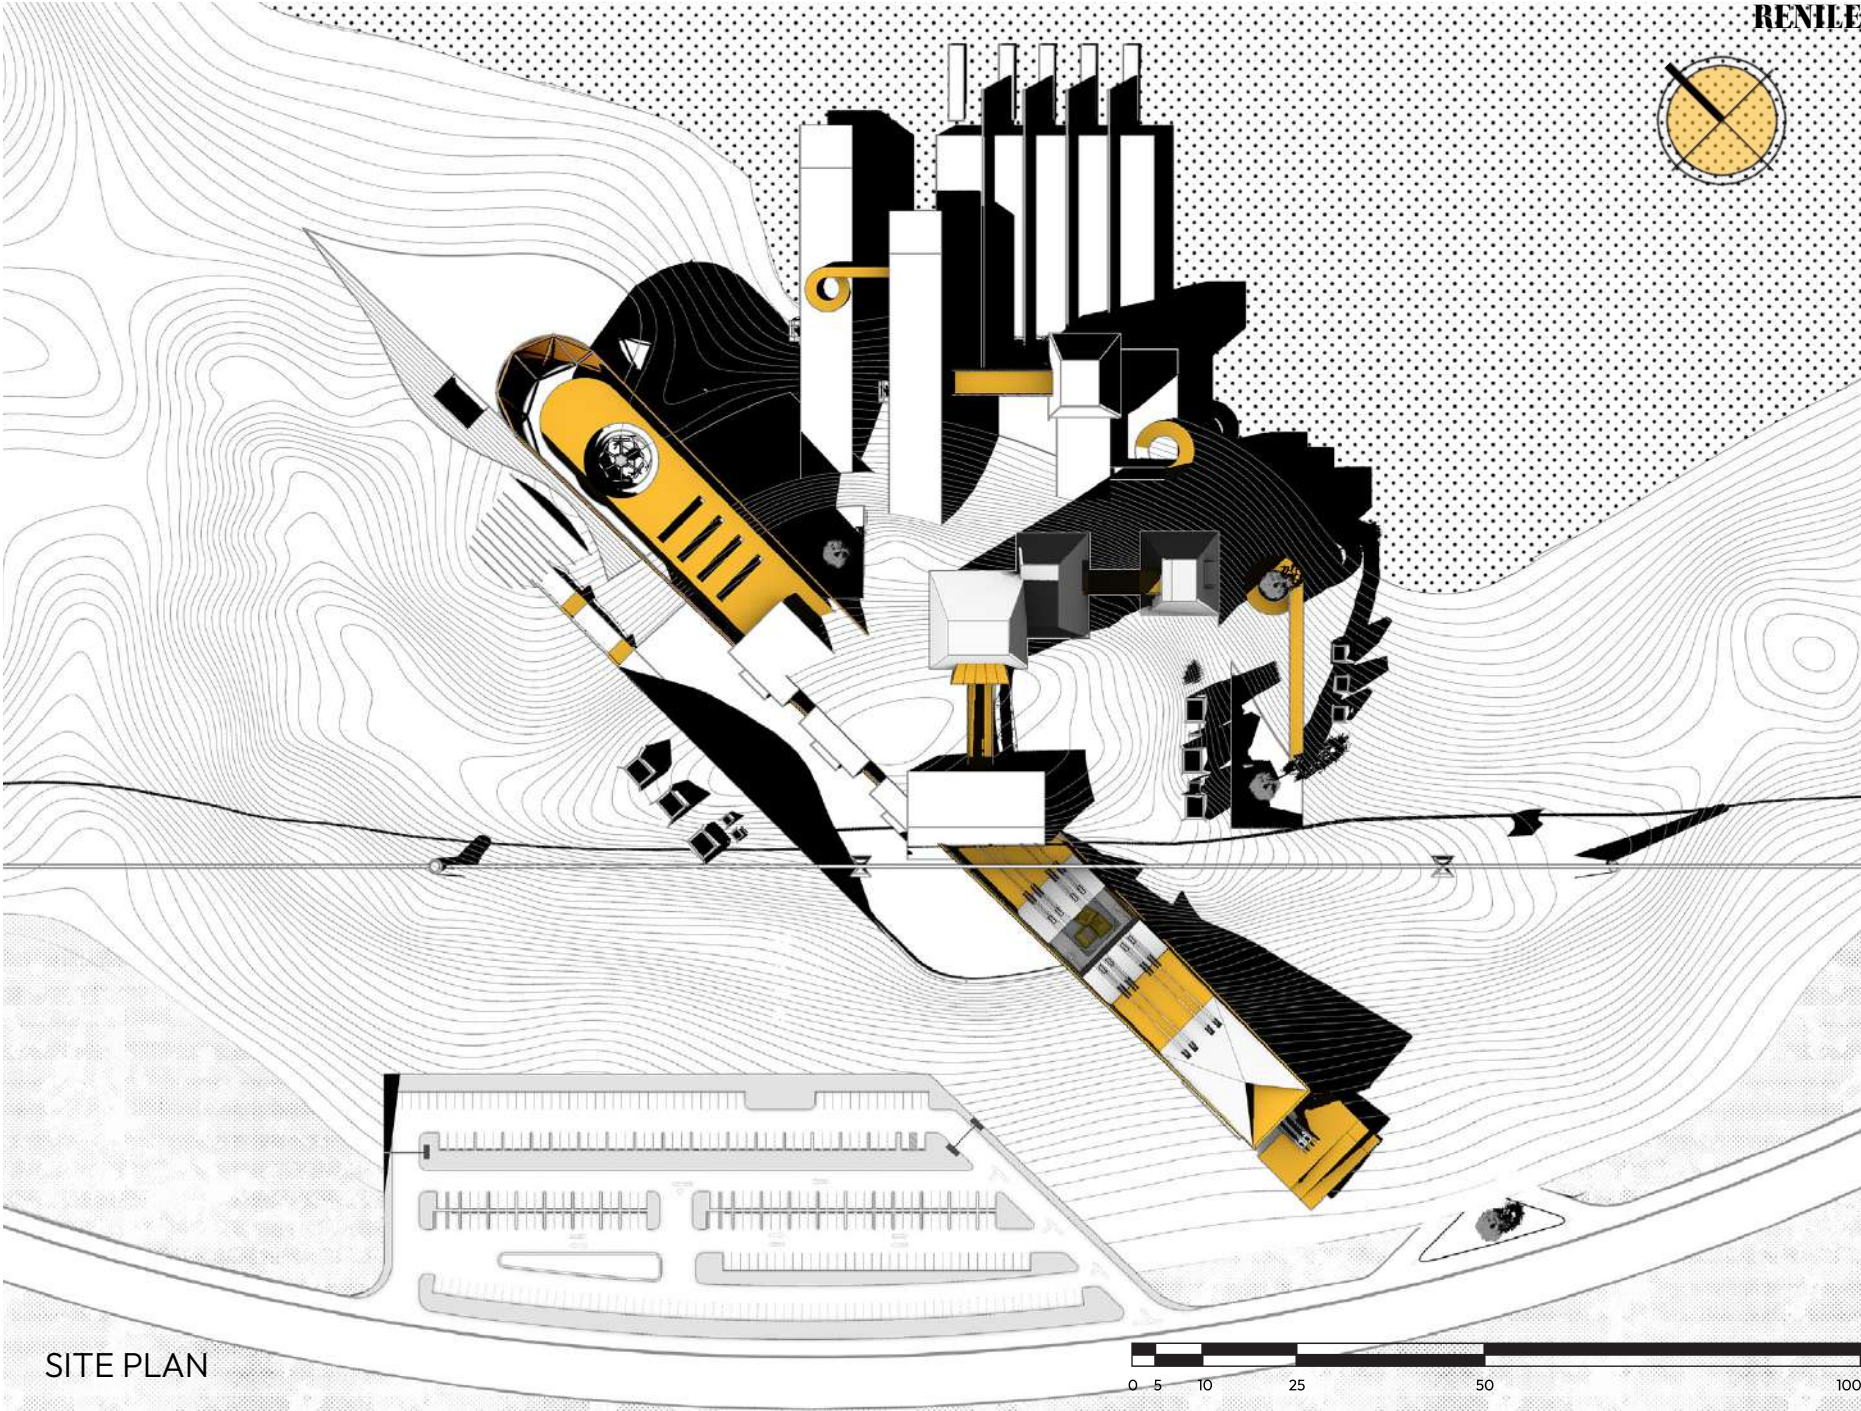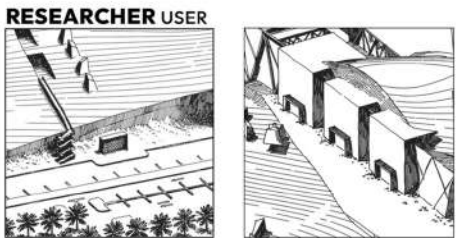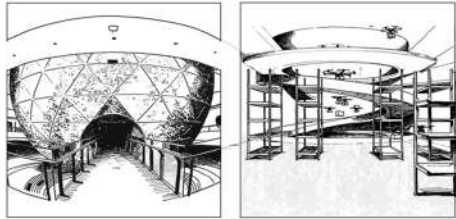

The site is not treated as a static piece of land, but as a living landscape shaped by movement, memory, and interaction. Architecture emerges from the terrain rather than resting upon it, allowing the built form, circulation, and topography to merge into a continuous spatial dialogue. The drawing captures this relationship as a dynamic composition where every layer contributes to a single architectural narrative.

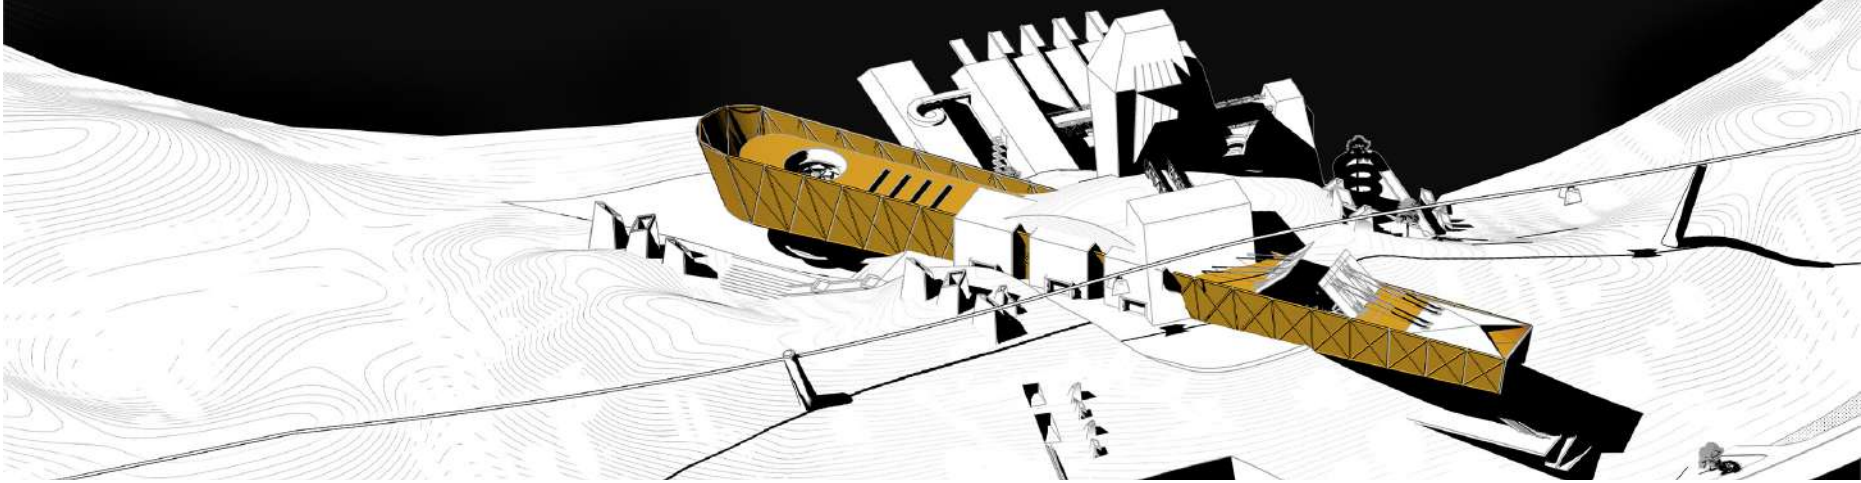


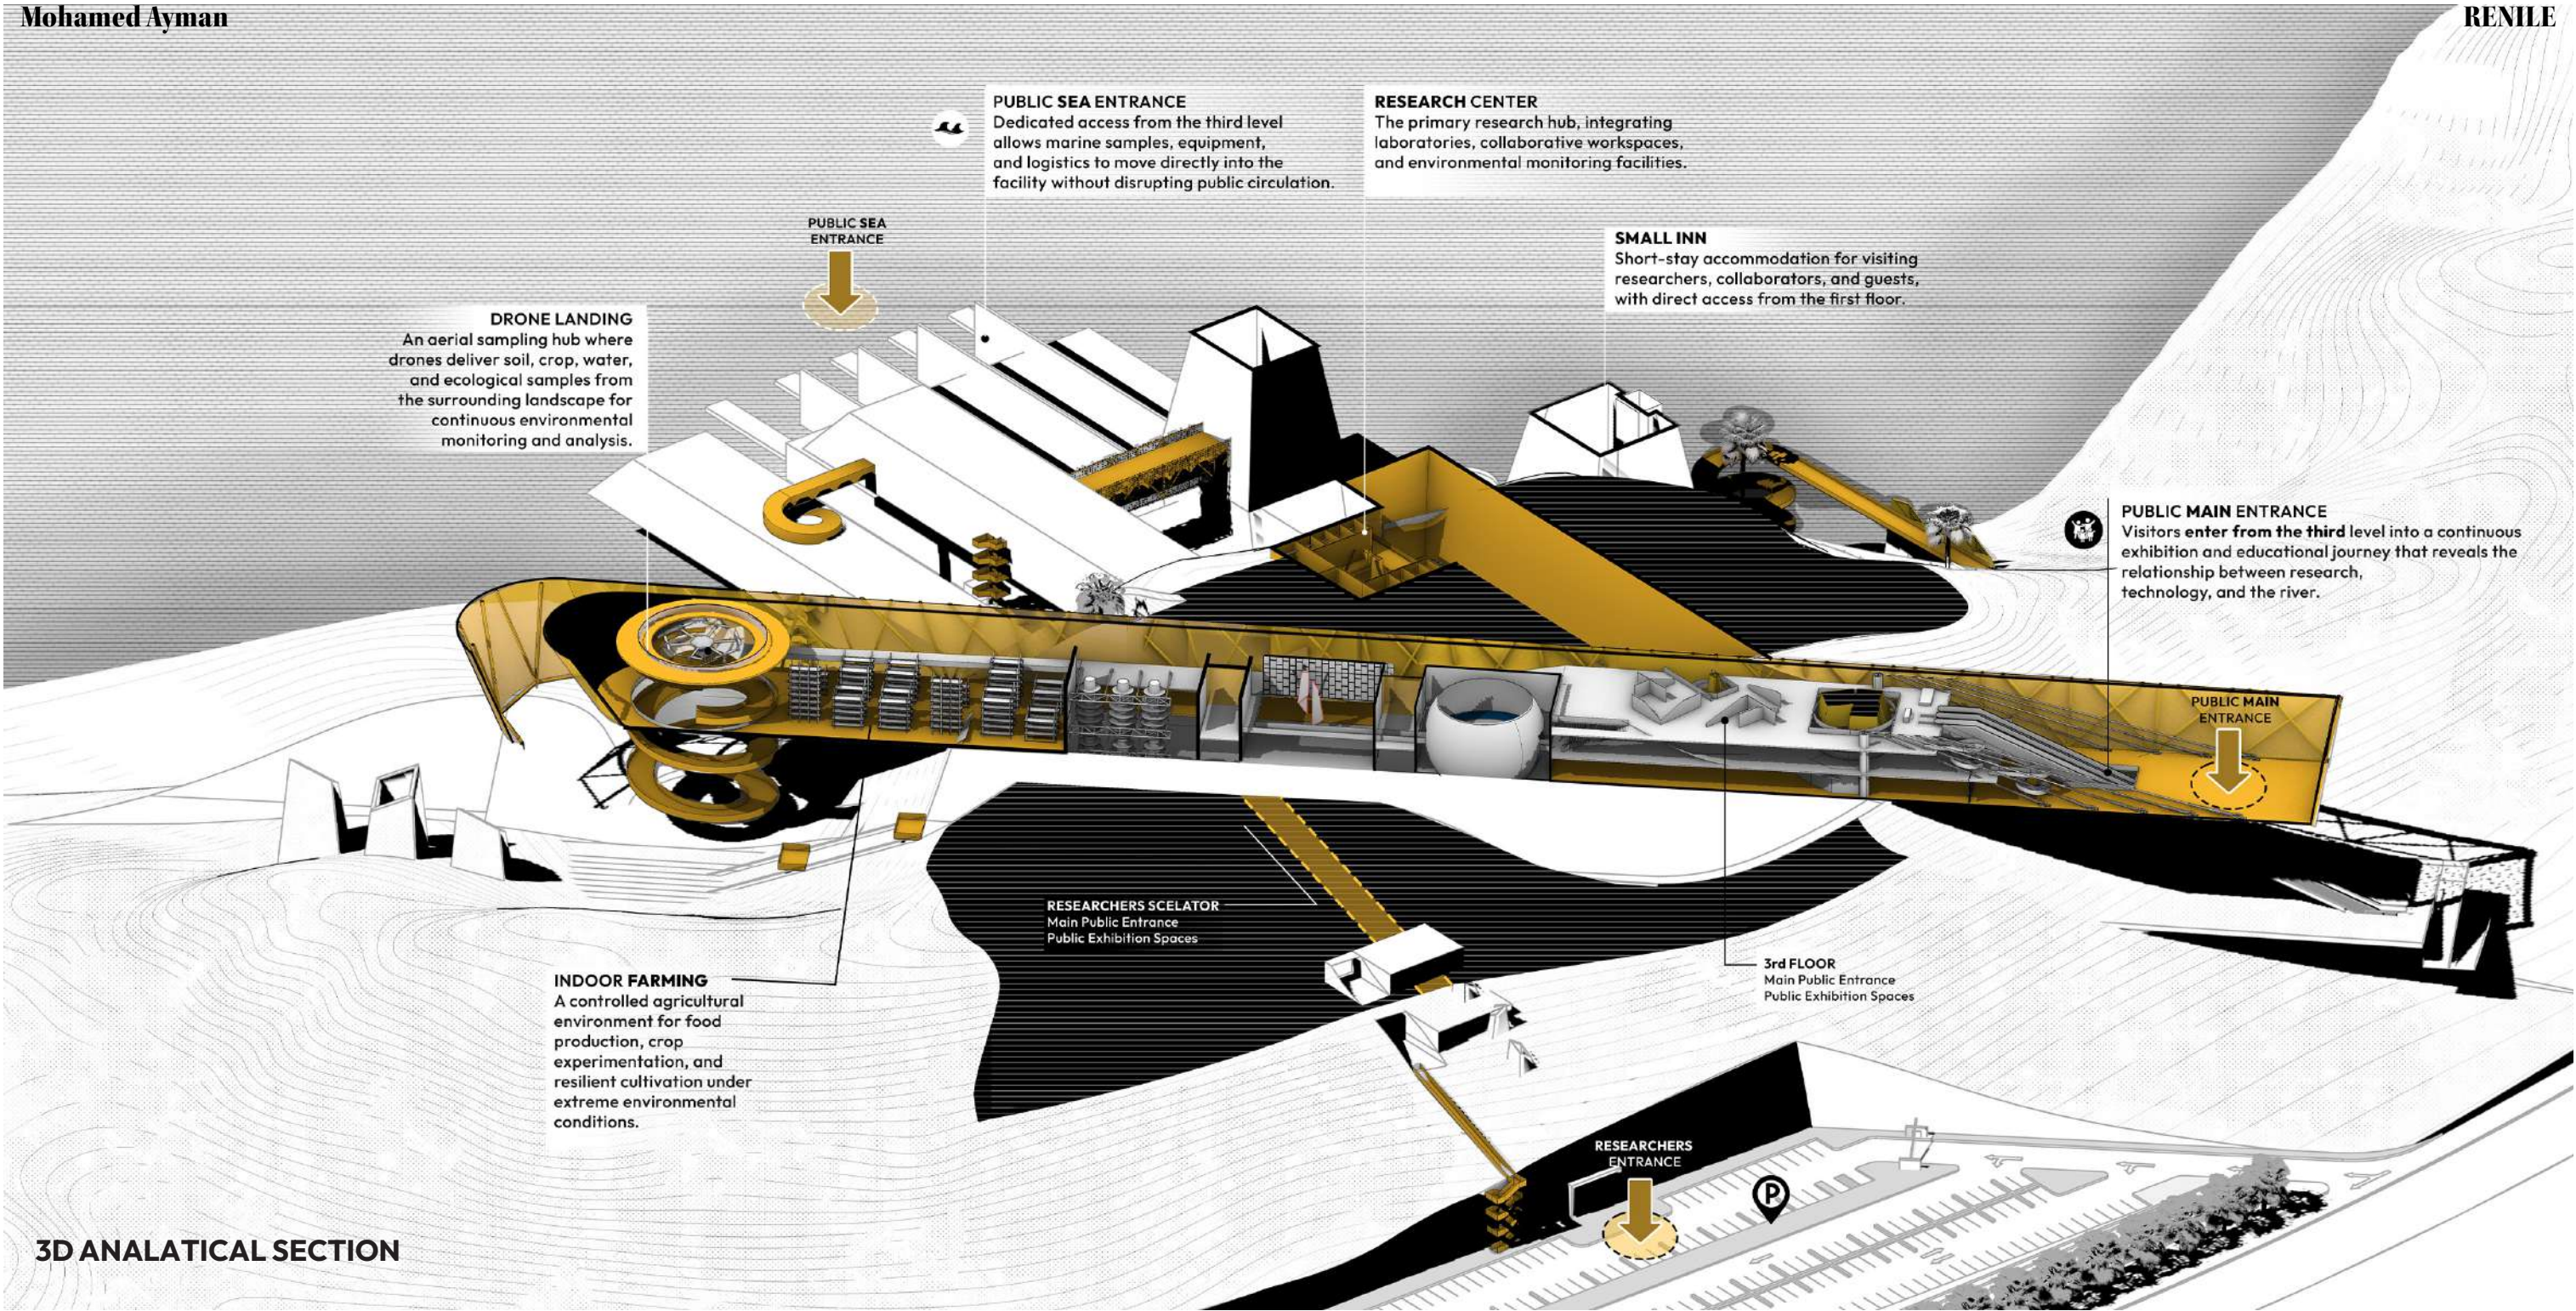



TO THE STATUE

A futuristic golden interior with twin escalators leading to a monumental abstract sculpture. Bold geometric forms, spiral ramps, and expansive glass surfaces create a dramatic sense of scale, while warm golden finishes and natural light enhance the space with elegance, innovation, and timeless architectural character.

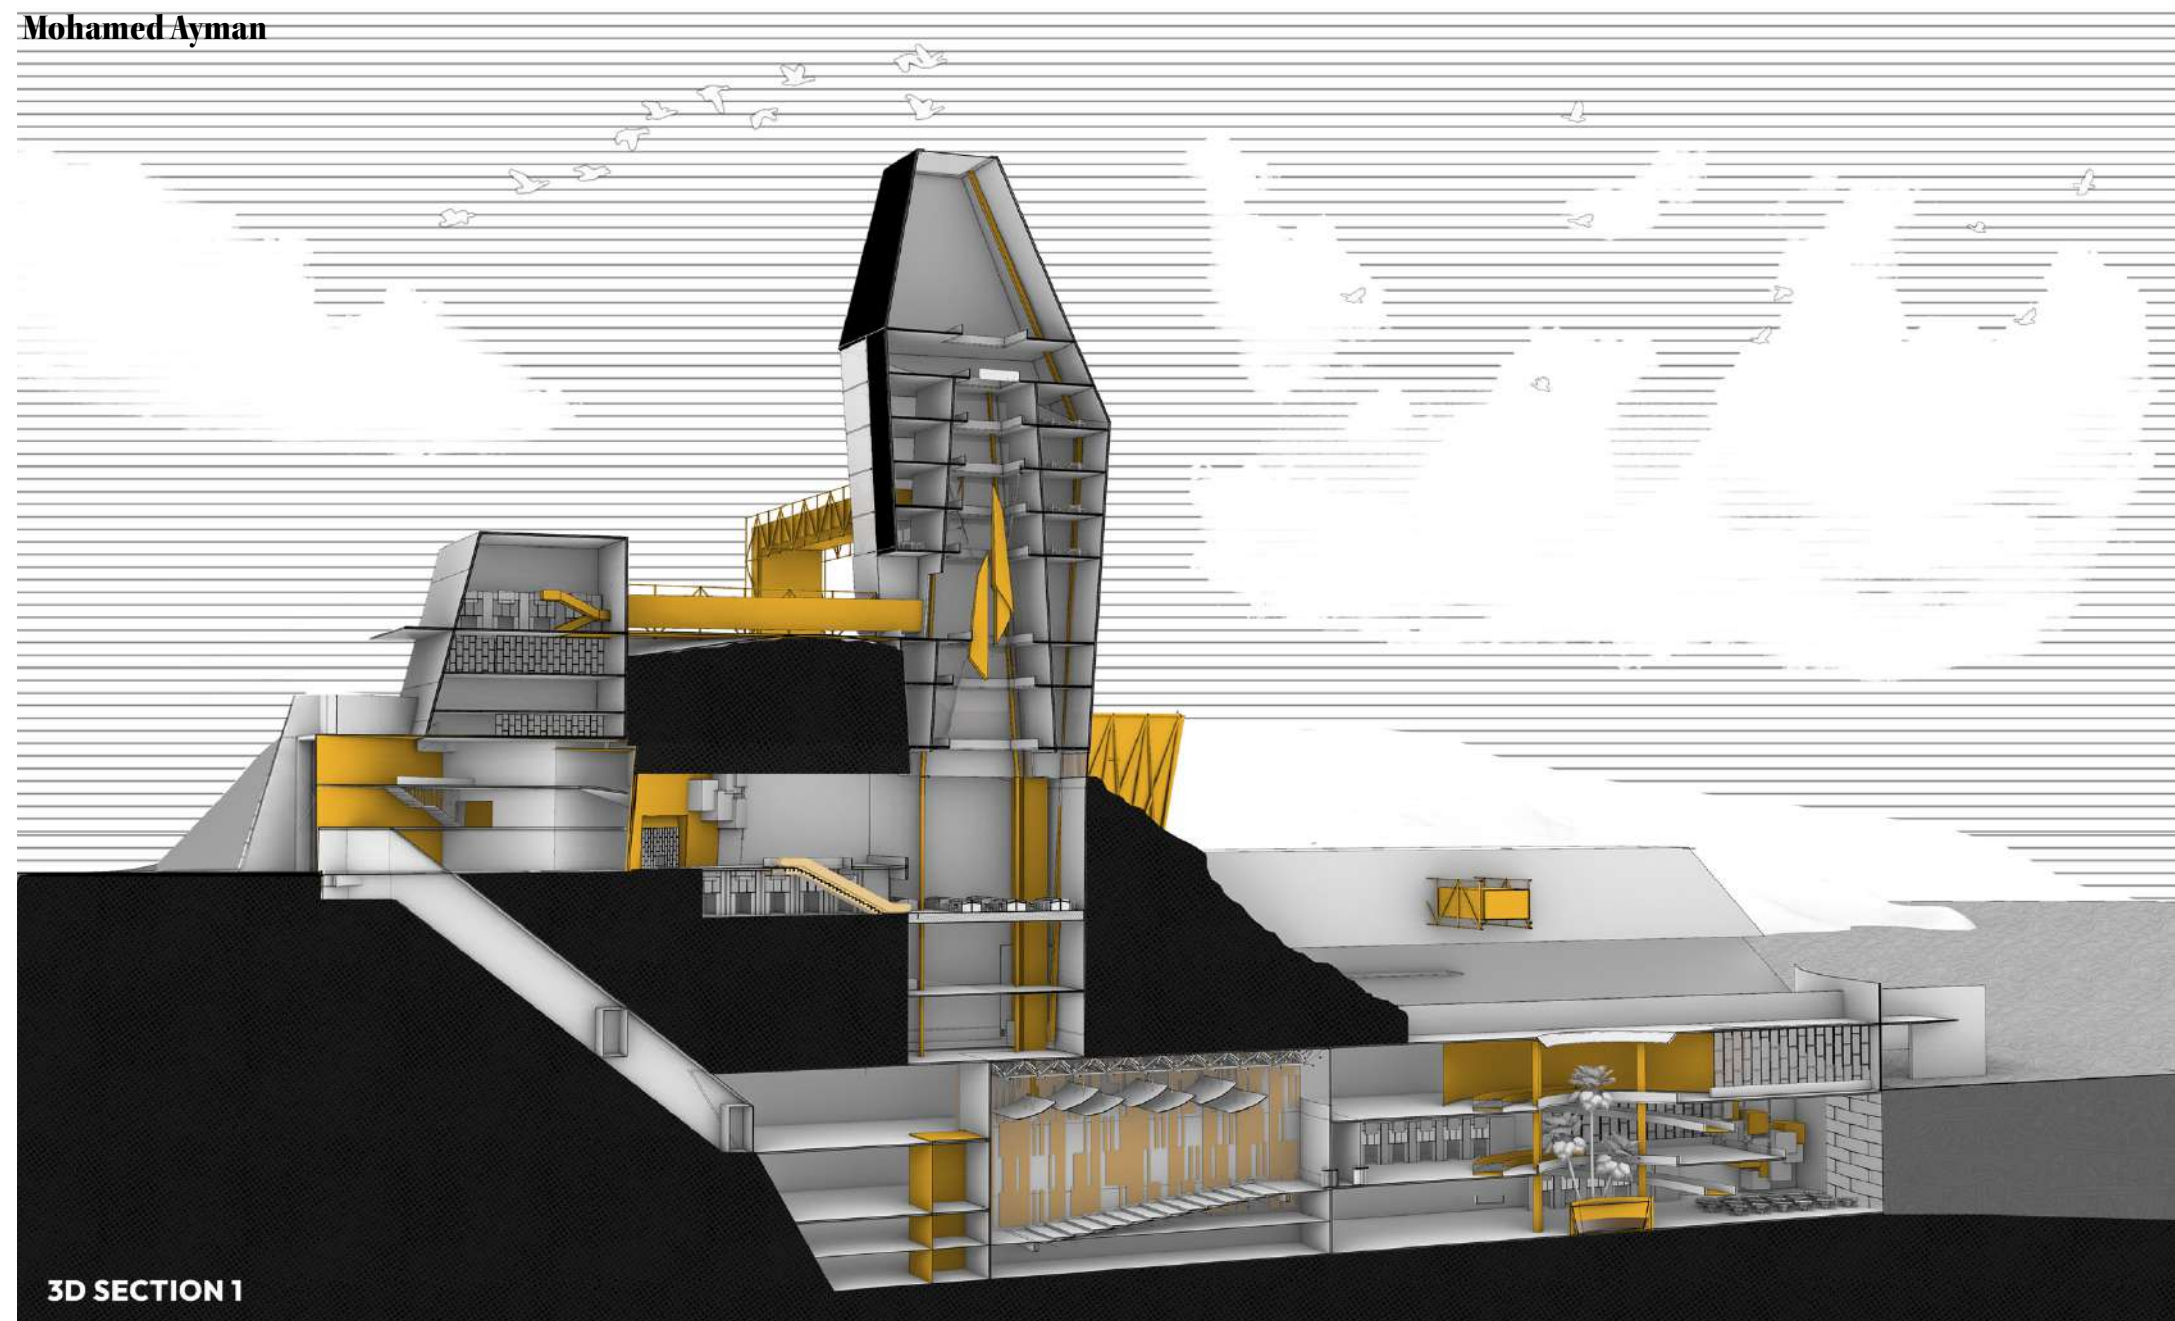

STUDIO THEME


A journey from darkness to light.



THE ELEMENT OF SURPRISE

Inspired by mountain caves, the project reveals space gradually moving from darkness into light, creating a moment of discovery.

WALL SECTION

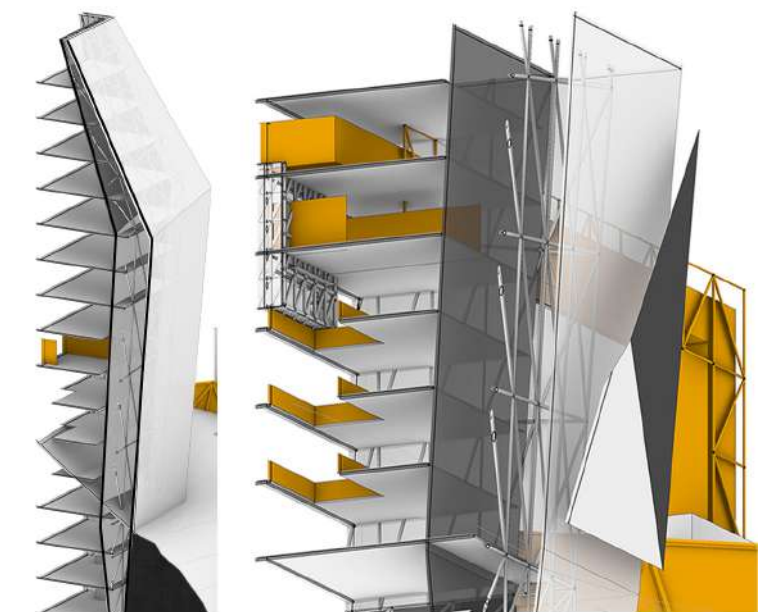


A multi-layered smart façade system integrating energy-efficient glazing with an adaptive structural frame, complemented by dynamic light and privacy screens to achieve optimal environmental performance and visual comfort.





2D SECTION

FORM GENERATION

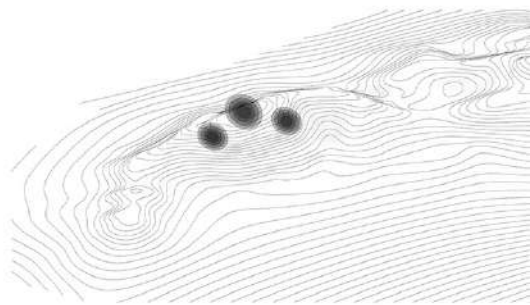


1) Site Forces
Analyzing topography and environmental forces shaping the site.




2)3D Zoning
Organizing functions vertically and horizontally across the terrain.




3) INTIAL MASSING
Generating primary volumes based on zoning and site response.

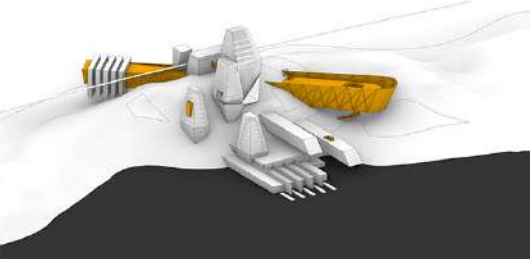

4) CONCEPT LAYER
Applying the conceptual theme to articulate and sculpt the masses

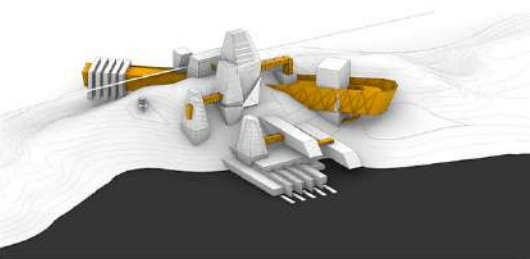

5) FINAL FORM
Connecting volumes through bridges to achieve a unified final form

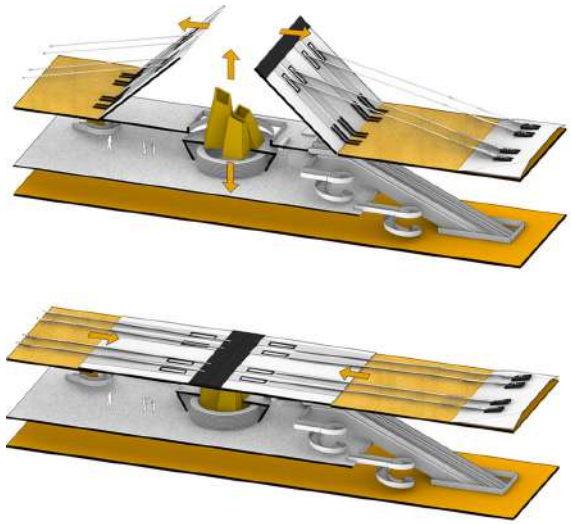

RESPONSIVE ROOF
A kinetic roof system that transitions between open and closed configurations to regulate environmental conditions and spatial experience.


MASTERPLAN

LEGEND


- 1 ENTRANCE
- 2 CAFE
- 3 TICKET PASSAGE
- 4 EXHIBITION 1
- 5 EXHIBITION 2
- 6 EXHIBITION 3
- 7 EXHIBITION 4
- 8 FARMING
- 9 RARE PLANTS
- 10 DRONE LANDING
- 11 RESEARCH HUB
- 12 RESEARCH TOWER
- 13 SMALL INN
- 14 PLANTATION SUPPLY




ENTRANCE STUDY

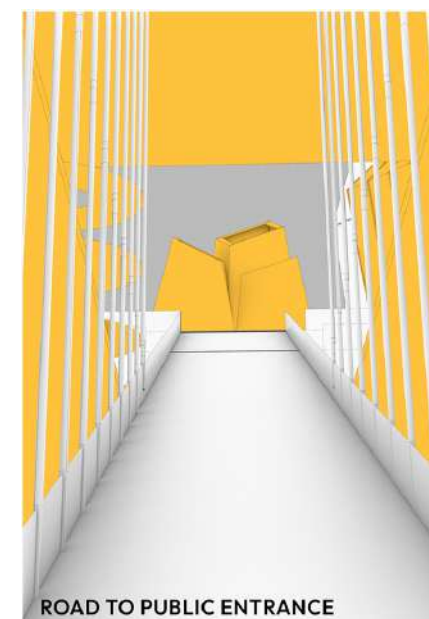


ROAD TO PUBLIC ENTRANCE

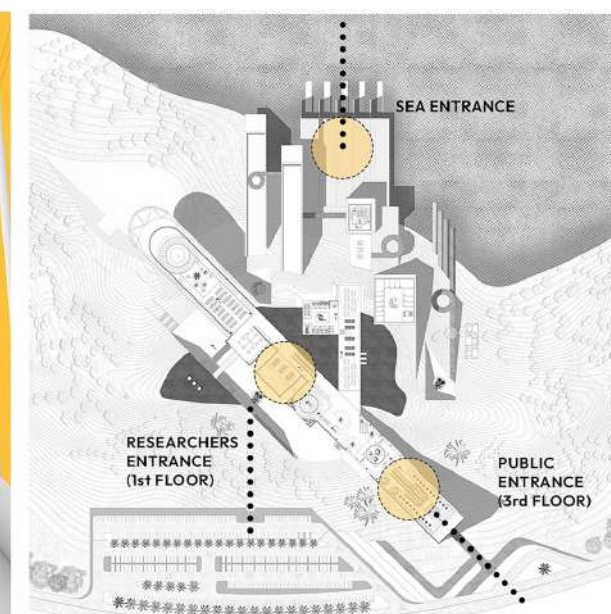

The project orchestrates a **layered sequence of entrances**, each responding to a different user group and level. From the public approach to the elevated entry, the journey is framed by vertical elements that guide movement and gradually reveal the architecture, while maintaining a clear separation between public, researchers, and sea access.


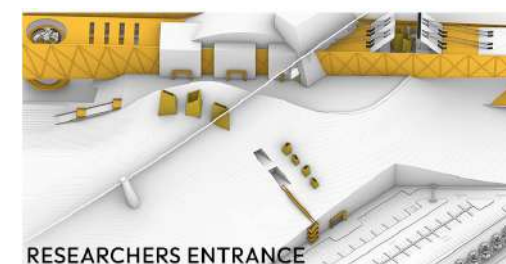


RESEARCHERS ENTRANCE

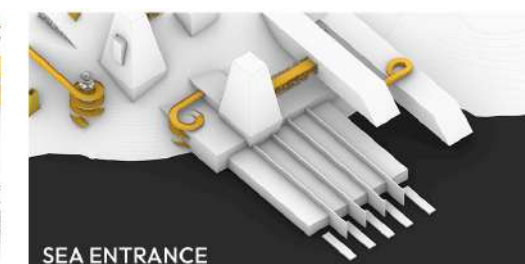


SEA ENTRANCE

STRUCTURE STUDY

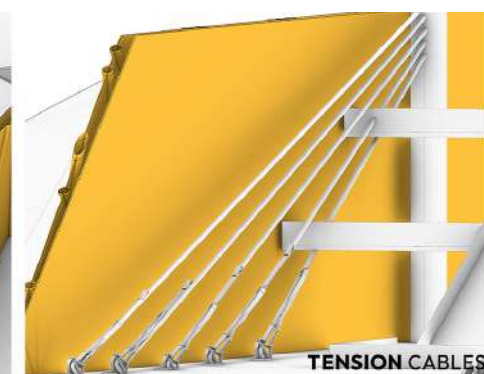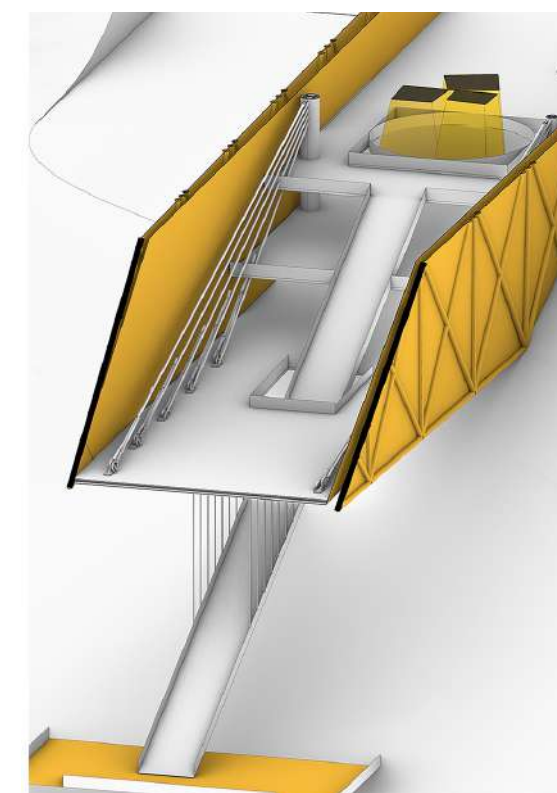

TENSION CABLES

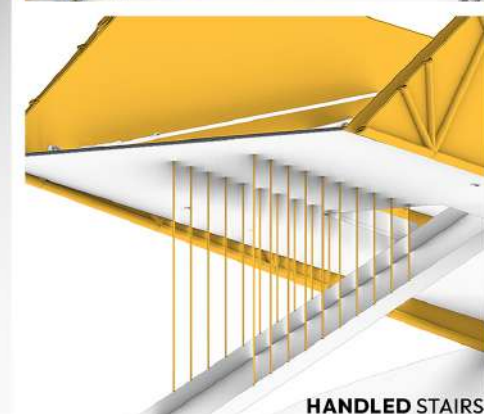


HANDLED STAIRS

Tension cables are used to support a **70m cantilever**, reducing bending moments and transferring loads to rear anchorage points for a more efficient structural system.

FIRST FLOOR PLAN

LEGEND



- 1 KITCHEN
- 2 STORAGE
- 3 ADMIN
- 4 VIP ENTRANCE
- 5 EXHIBITION 2
- 6 EXHIBITION 3
- 7 EXHIBITION 4
- 8 FARMING
- 9 RARE PLANTS
- 10 DRONE LANDING
- 11 WATER FILTRATION BY ROBOTS
- 12 RESEARCH TOWER
- 13 SMALL INN
- 14 MOVABLE SERVICE UNIT
- 15 PLANITATION SUPPLY

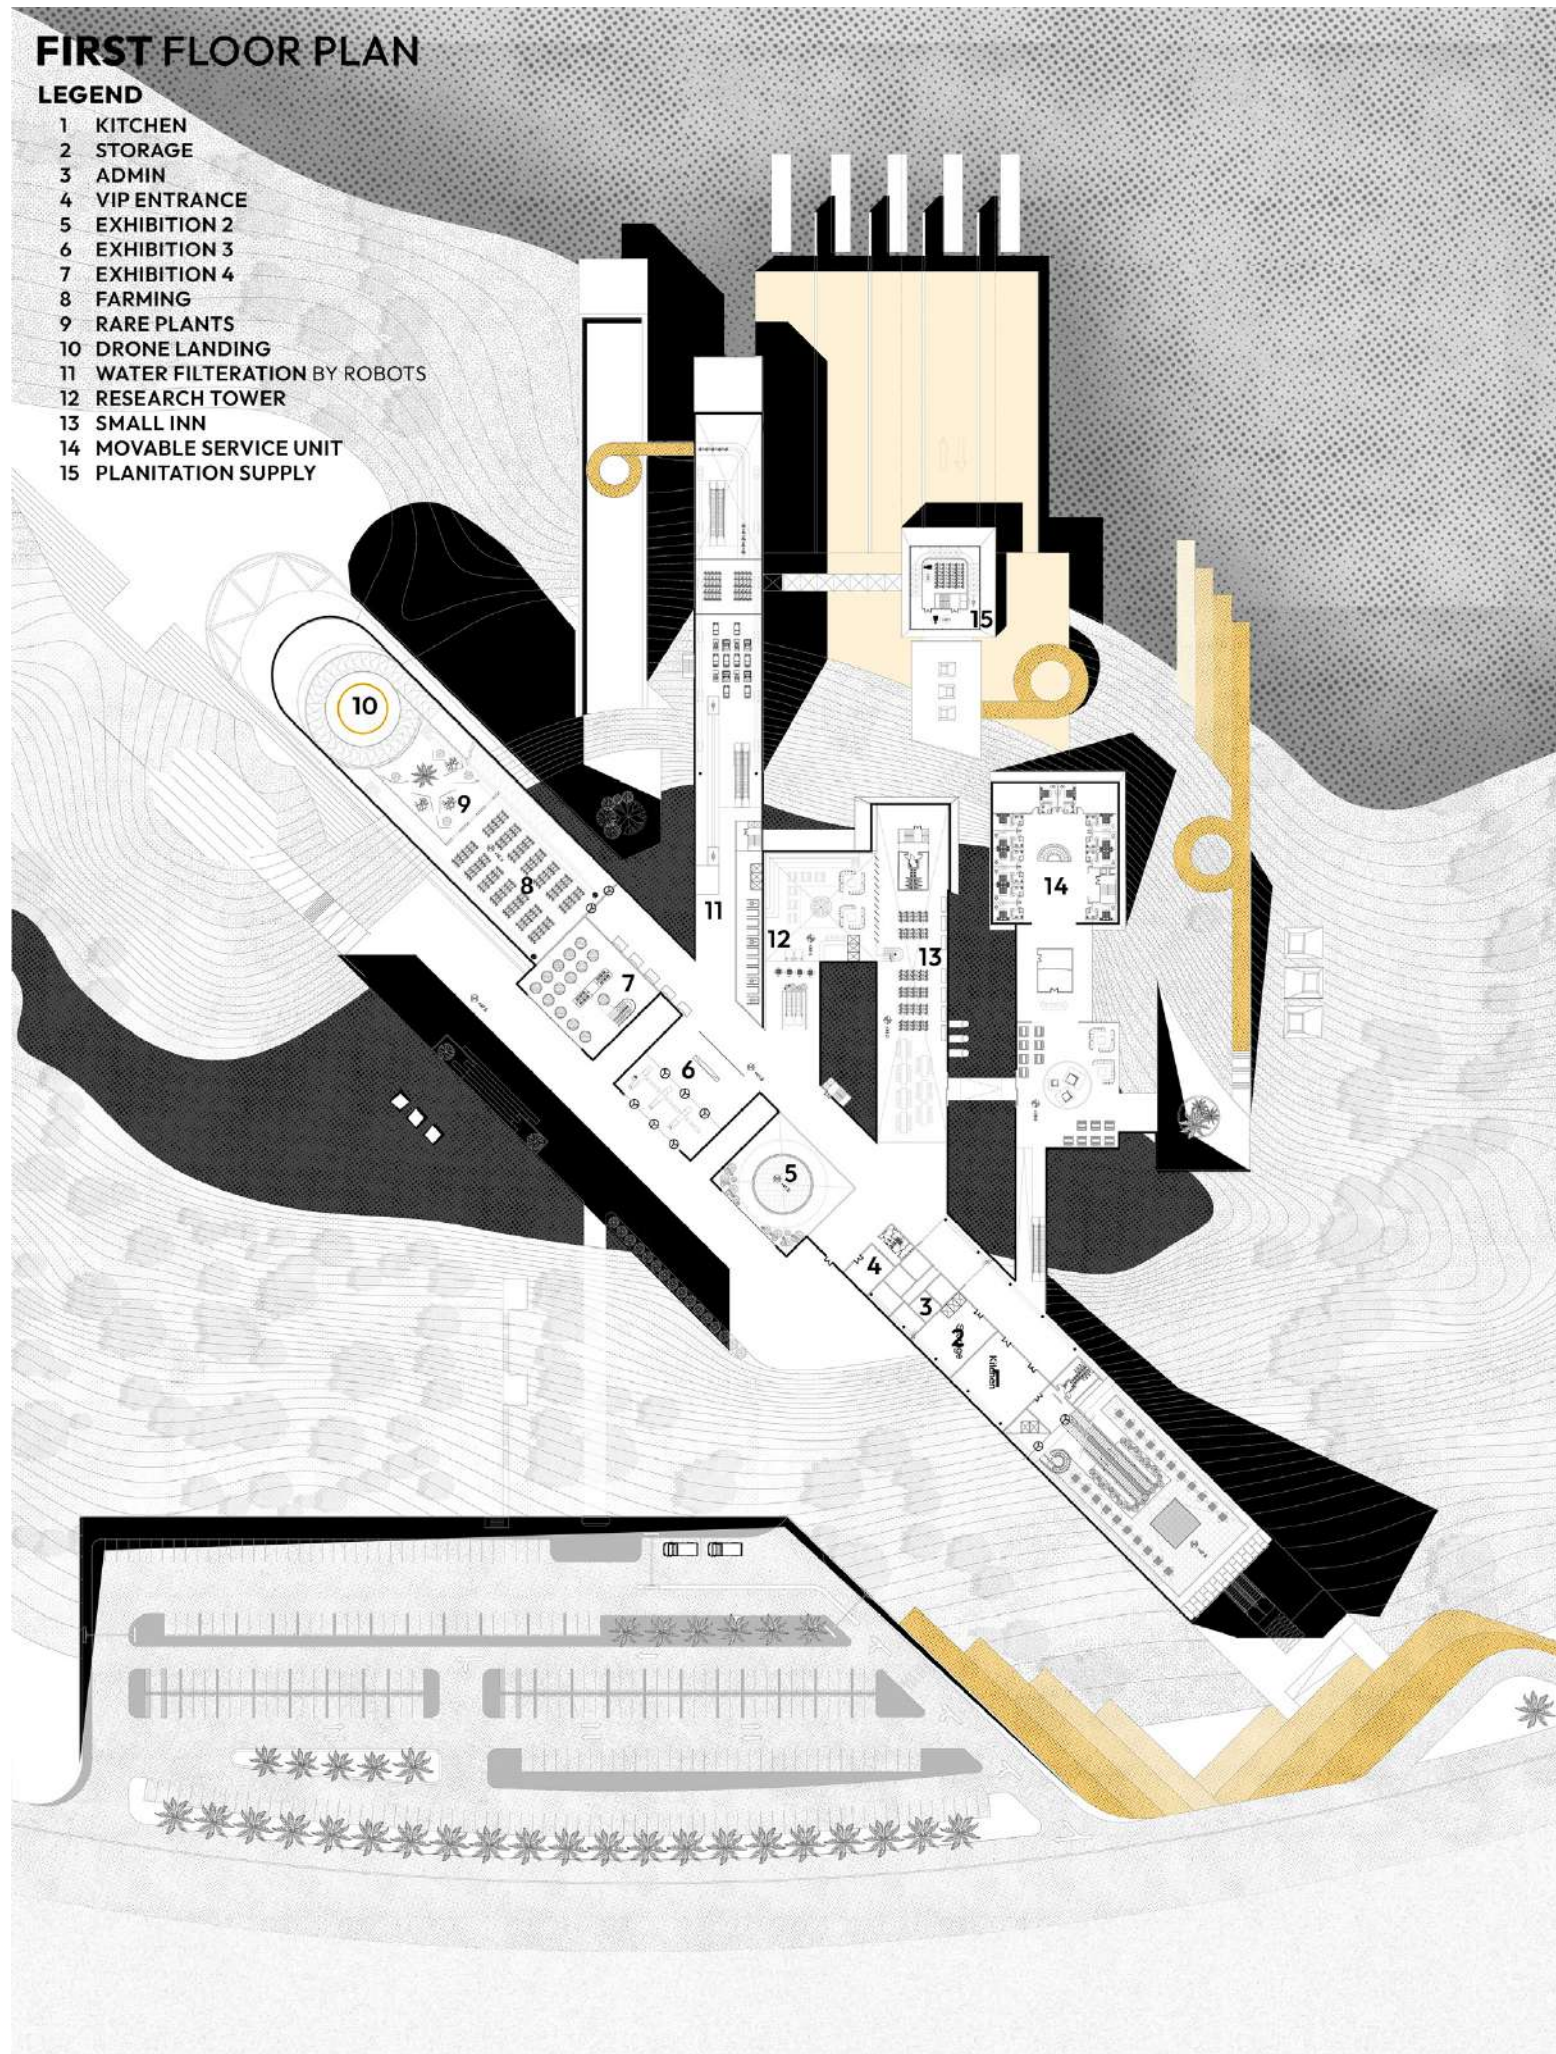

SEA FLOOR PLAN

LEGEND

- 01 Café
- 02 Small Kitchen
- 03 Central Atrium
- 04 Booths
- 05 Administration
- 06 Pavilion
- 07 Auditorium
- 08 Audio Room 01
- 09 Audio Room 02
- 10 Library
- 11 Exhibition Hall
- 12 Seating Area
- 13 Outdoor Gathering Space
- 14 Workshop Area
- 15 Exhibition Storage
- 16 Kitchen Storage
- 17 Trolley Storage
- 18 Waiting Area

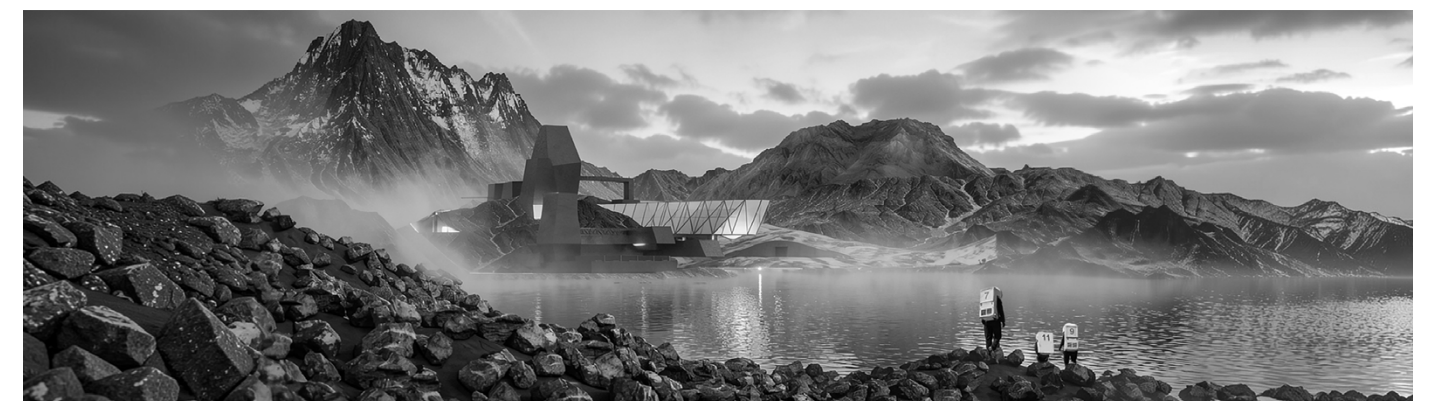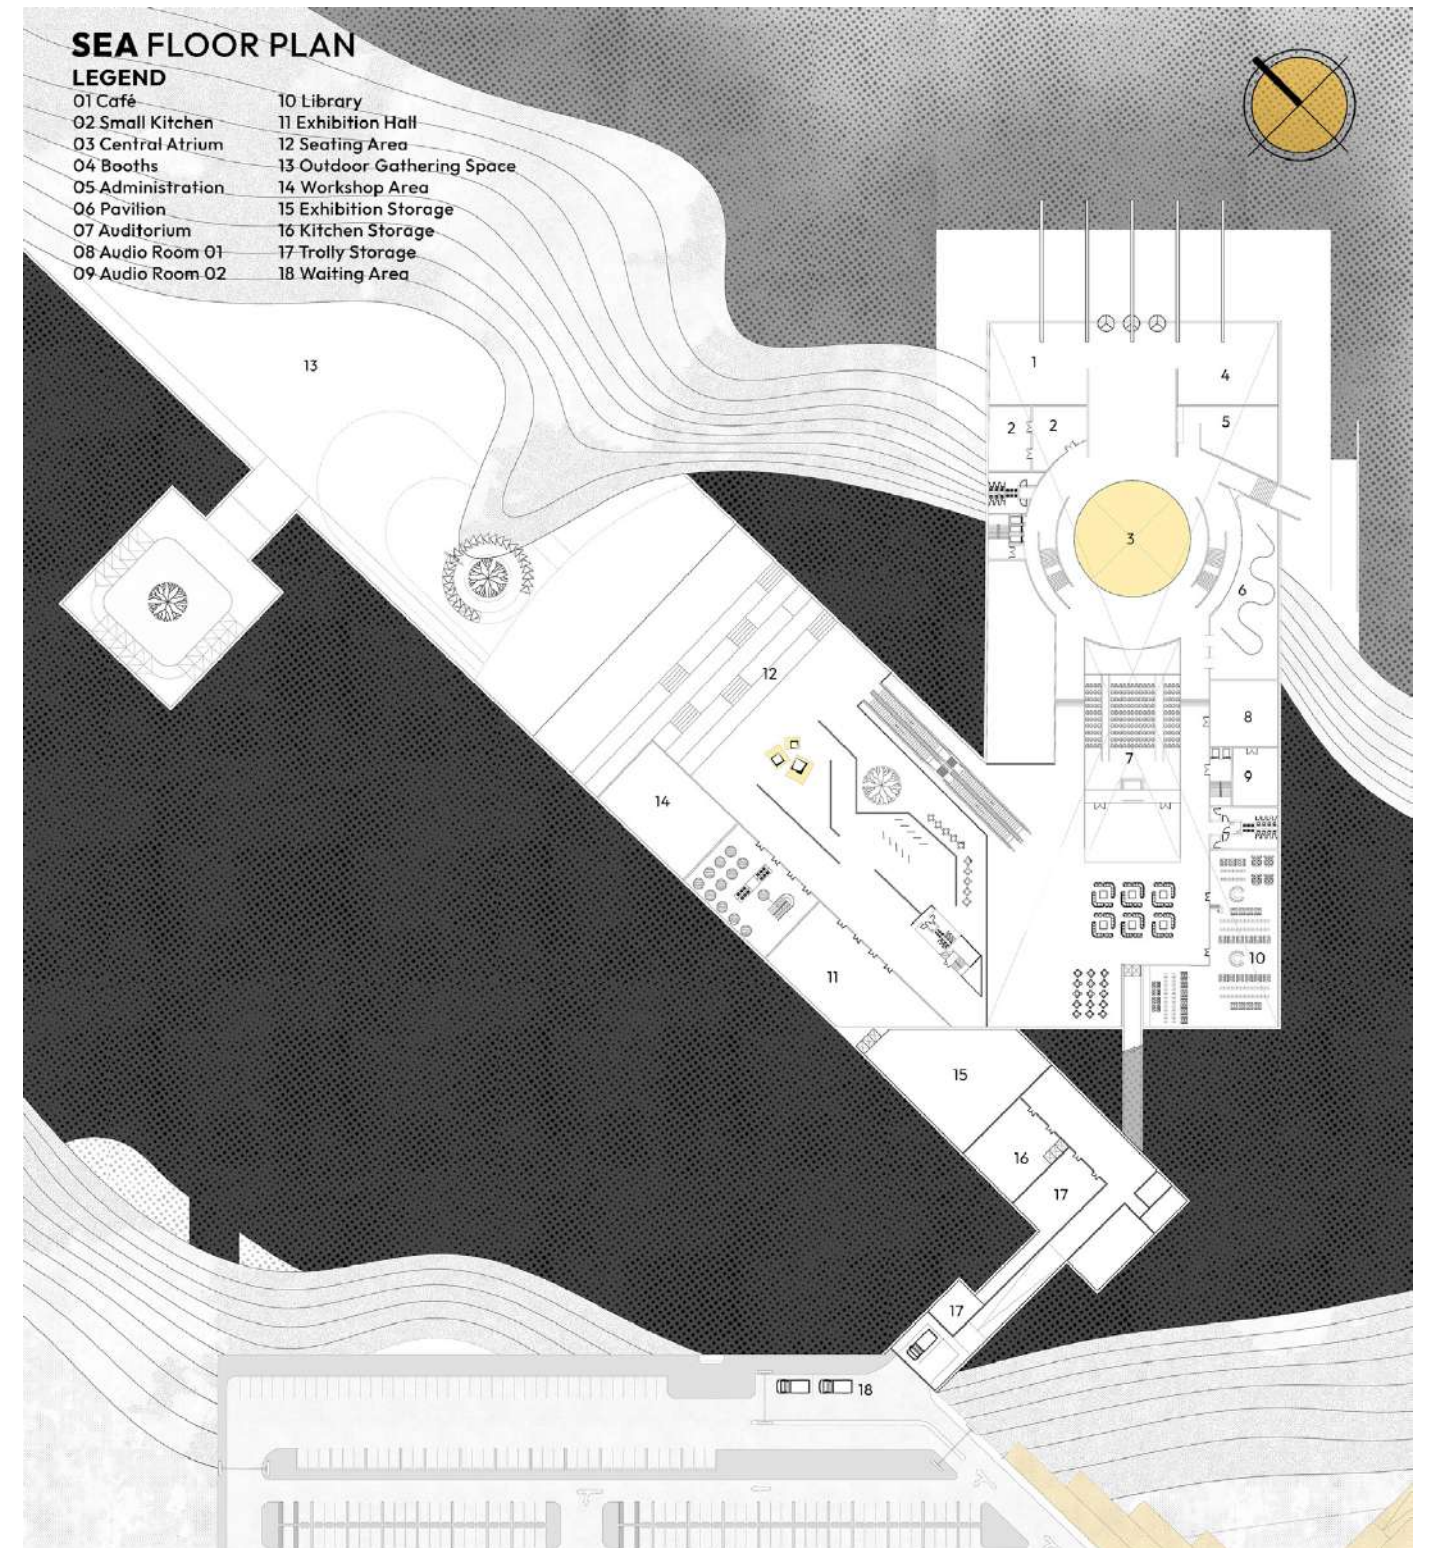

THE DIALOGUE

The project was designed to merge with the surrounding nature rather than stand apart from it. The building form is inspired by the geometry of the mountains, using sharp angles and fragmented masses to create harmony with the landscape.



[Press here for more details](#)

2

ROSETTA HOTEL

ACADEMIC WORK

SMART SYSTEM DESIGN STUDIO

Ain Shams University, Faculty of Engineering

Year: 2025

Location: Rashid, Egypt

Project: Hotel

Softwares: Rhino, 3Ds Max, Corona, Photoshop, Illustrator

Role: (Individual)


CONCEPT

“The Dialogue” is not merely a title — it is the essence of this architectural narrative. The project embodies the unique conversation between land and sea, between structure and flow, between the contained (indoor) and the limitless (outdoor). Inspired by Rashid’s unique geographical and historical context — where the Nile and Mediterranean meet — the design draws from this natural confluence, creating a fluid form that extends bridges out into the landscape, just as the Nile stretches into the sea


THE DIALOGUE




FORM GENERATION

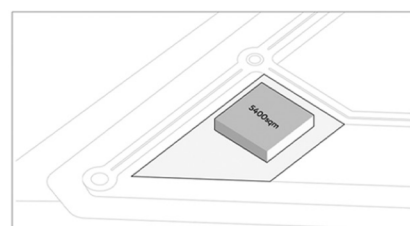


Basic extrusion for the builtup area

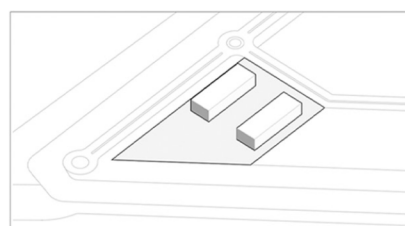


Splitting for better bedrooms orientation

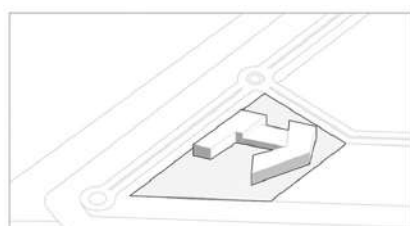


Emphasizing on Entrance

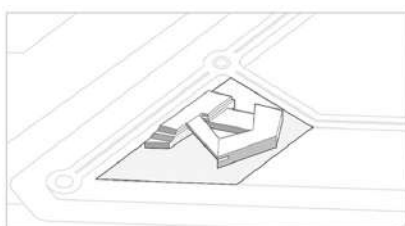

Adding a bridge to make an infinity pool with new experience

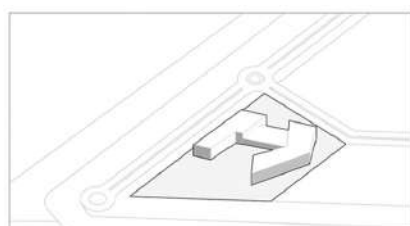



Emphasizing on Entrance


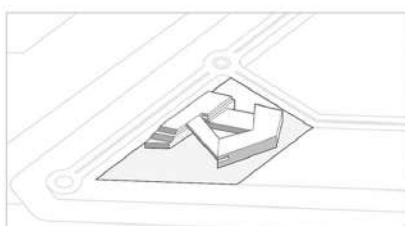





Adding a bridge to make an infinity pool with new experience

pathways don't just link locations; they bridge philosophies. The grounded base holds identity, memory, and rooted culture — while the floating arms invite flow, openness, and movement — just as Rasheed itself stands at the threshold where the Nile meets the Mediterranean, and

WHERE BORDERS DISSOLVE INTO DIALOGUE

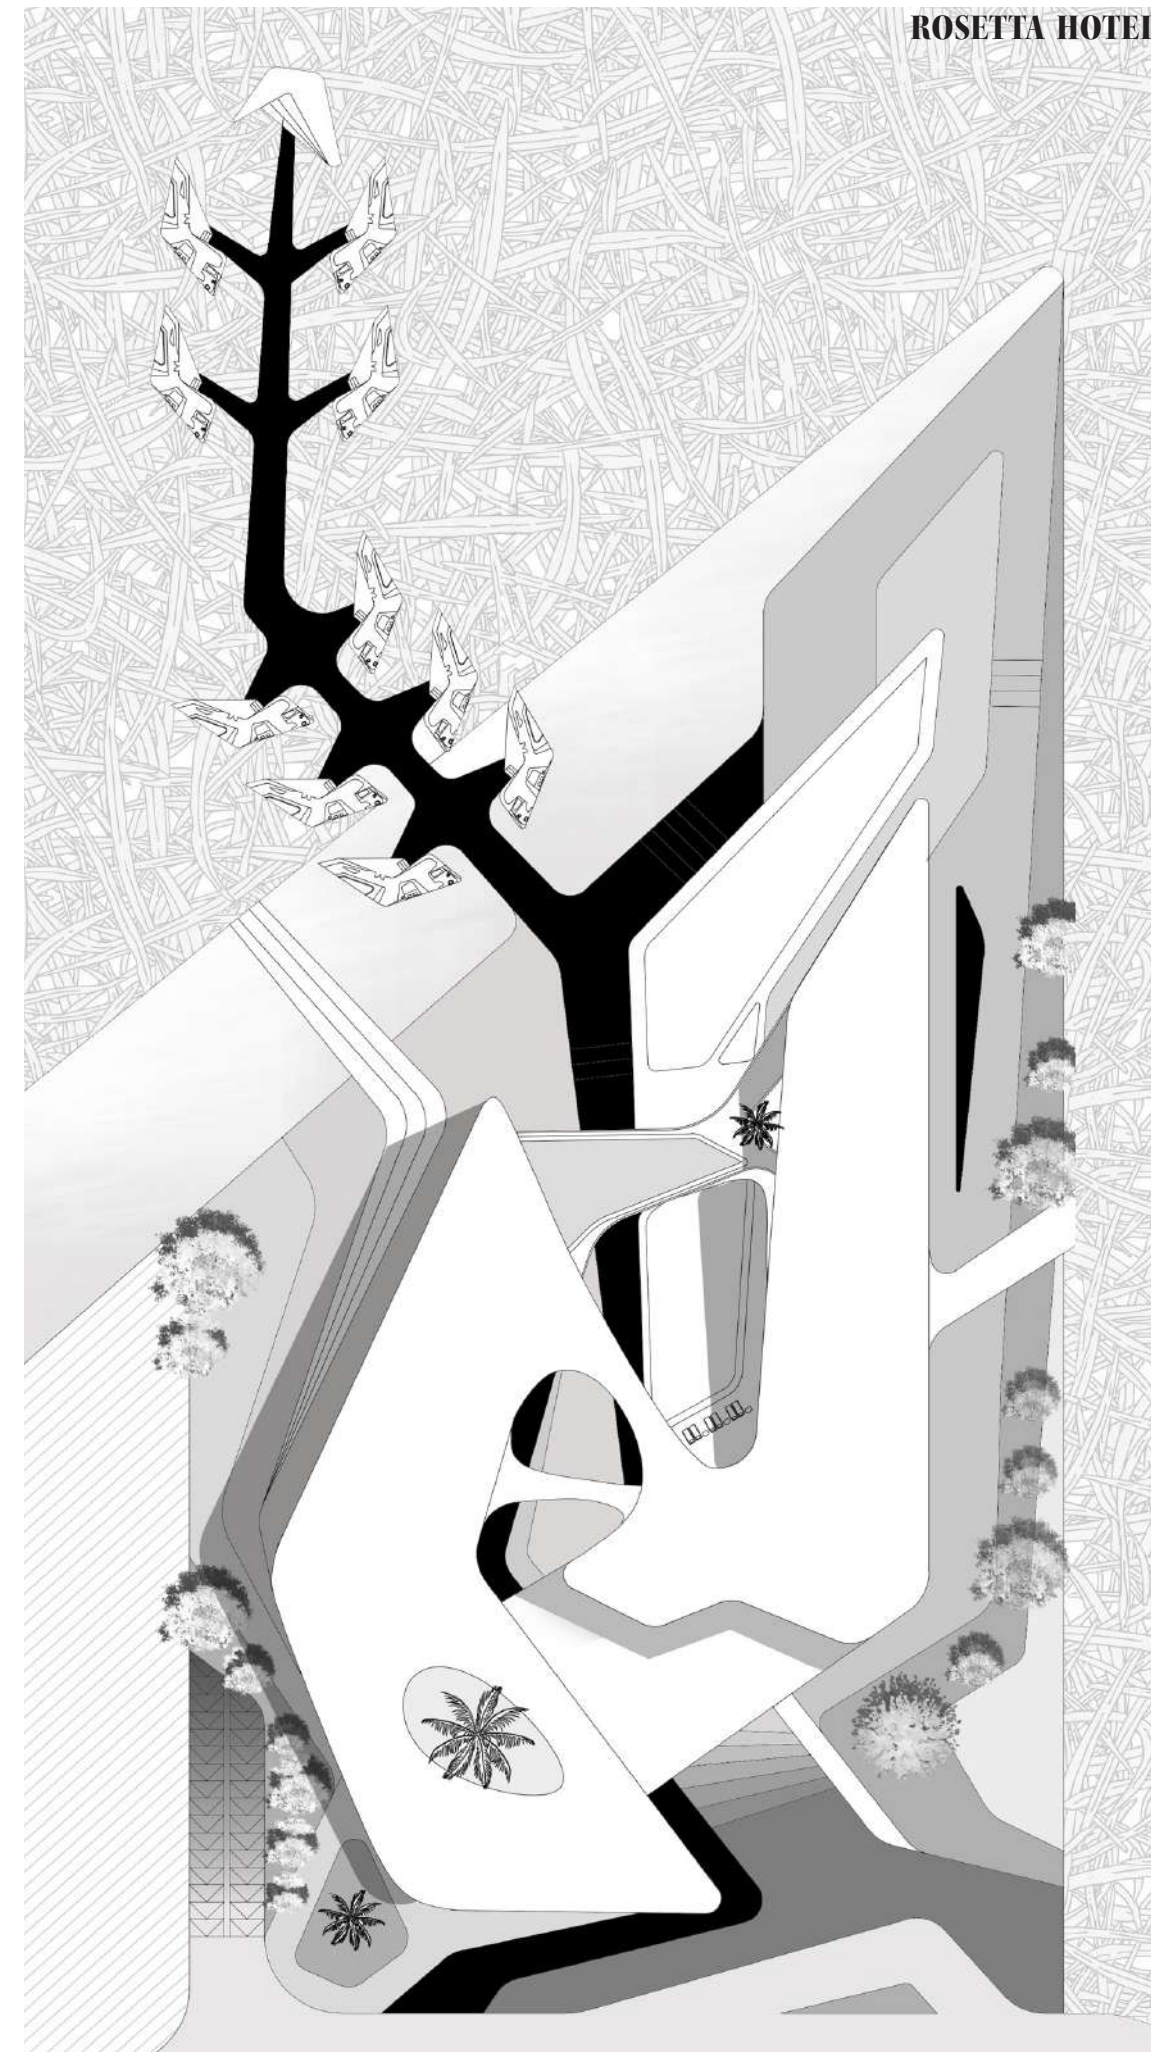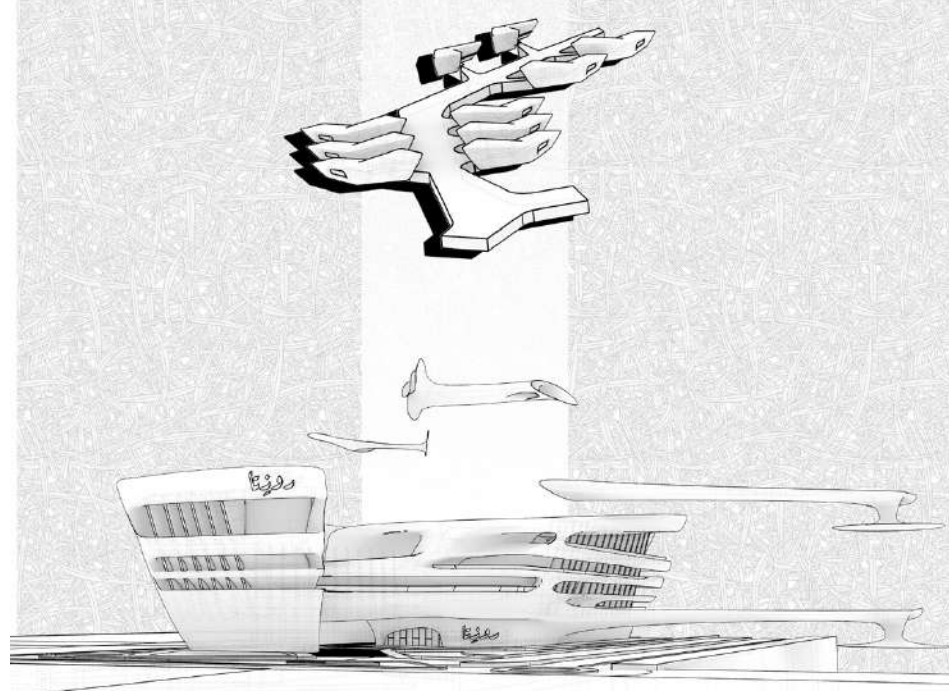

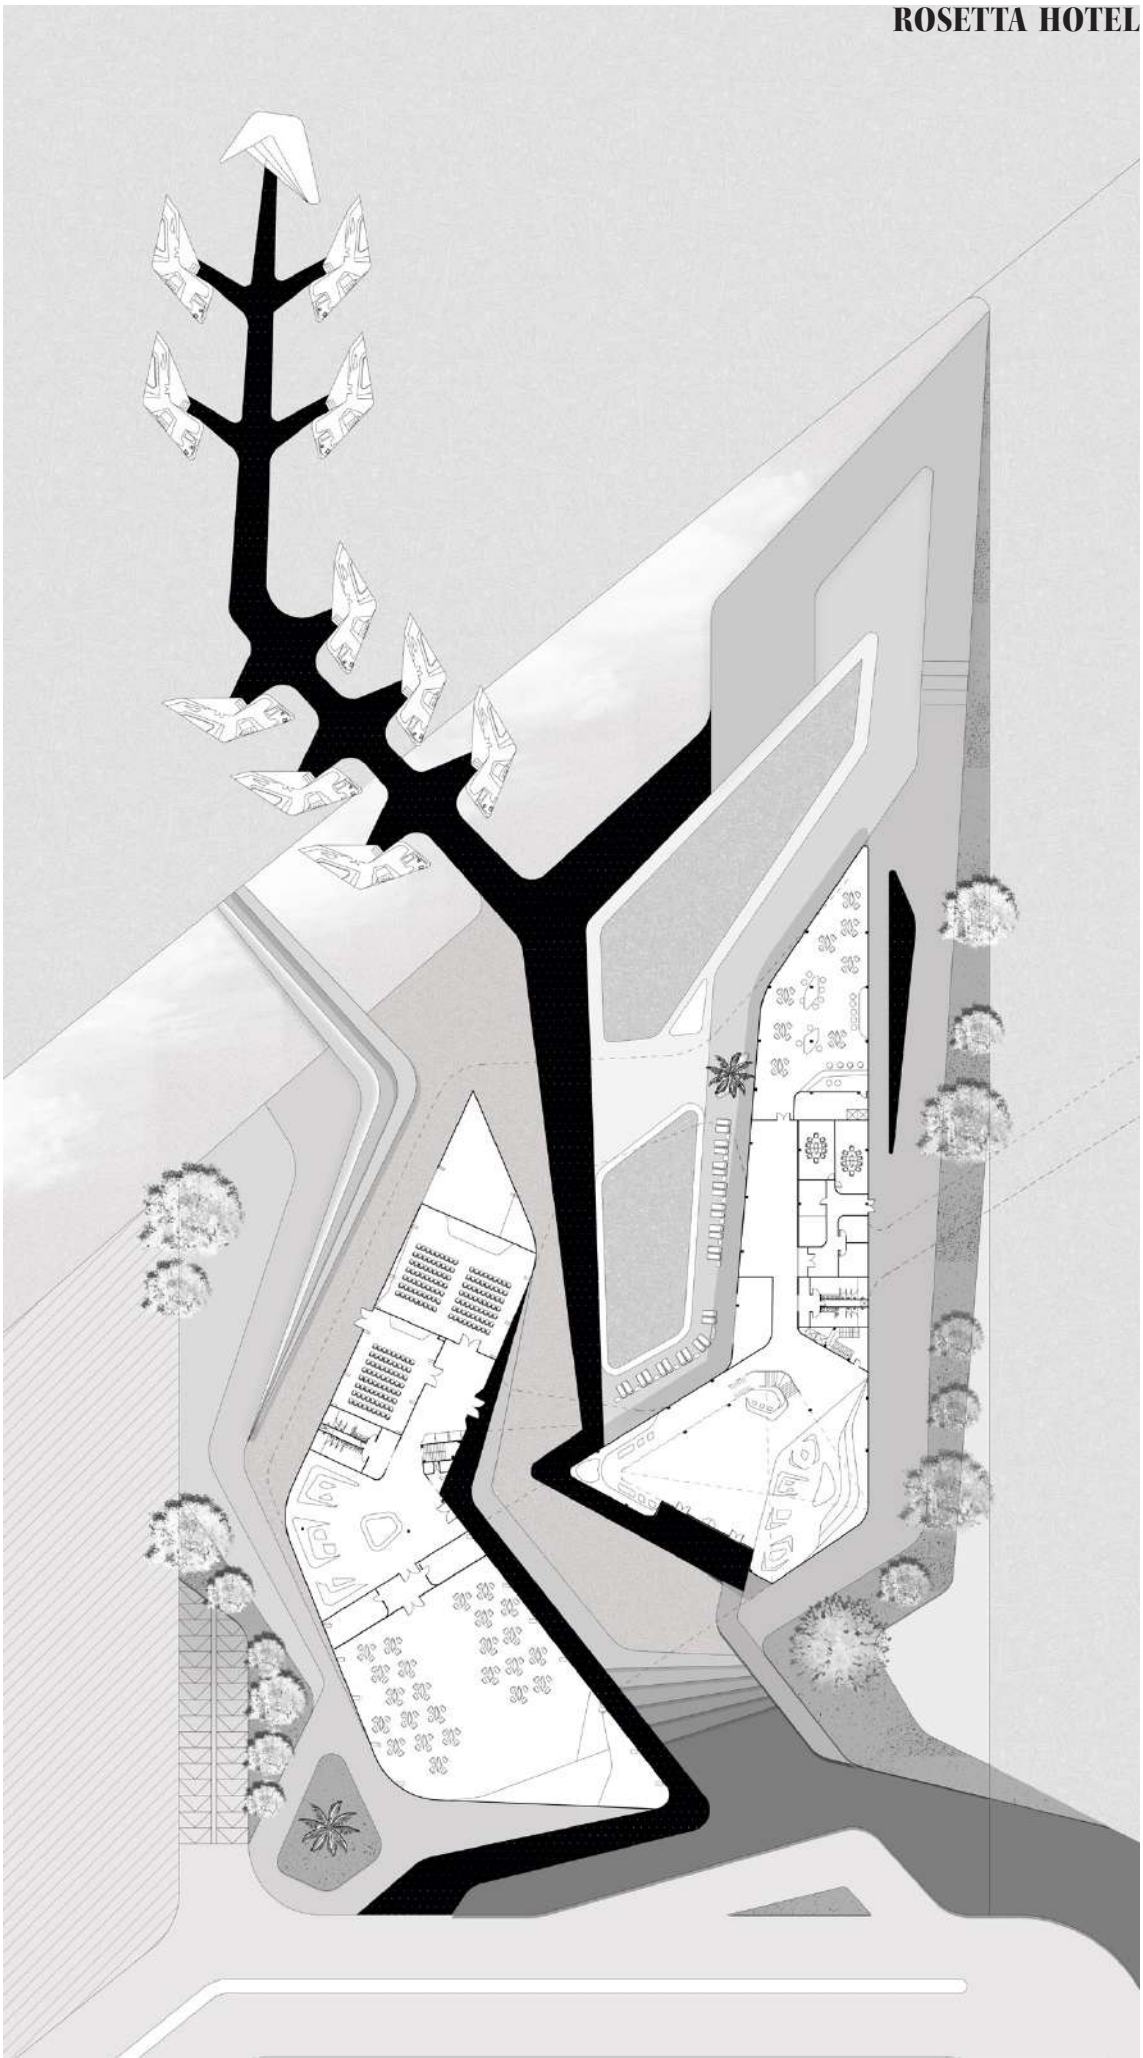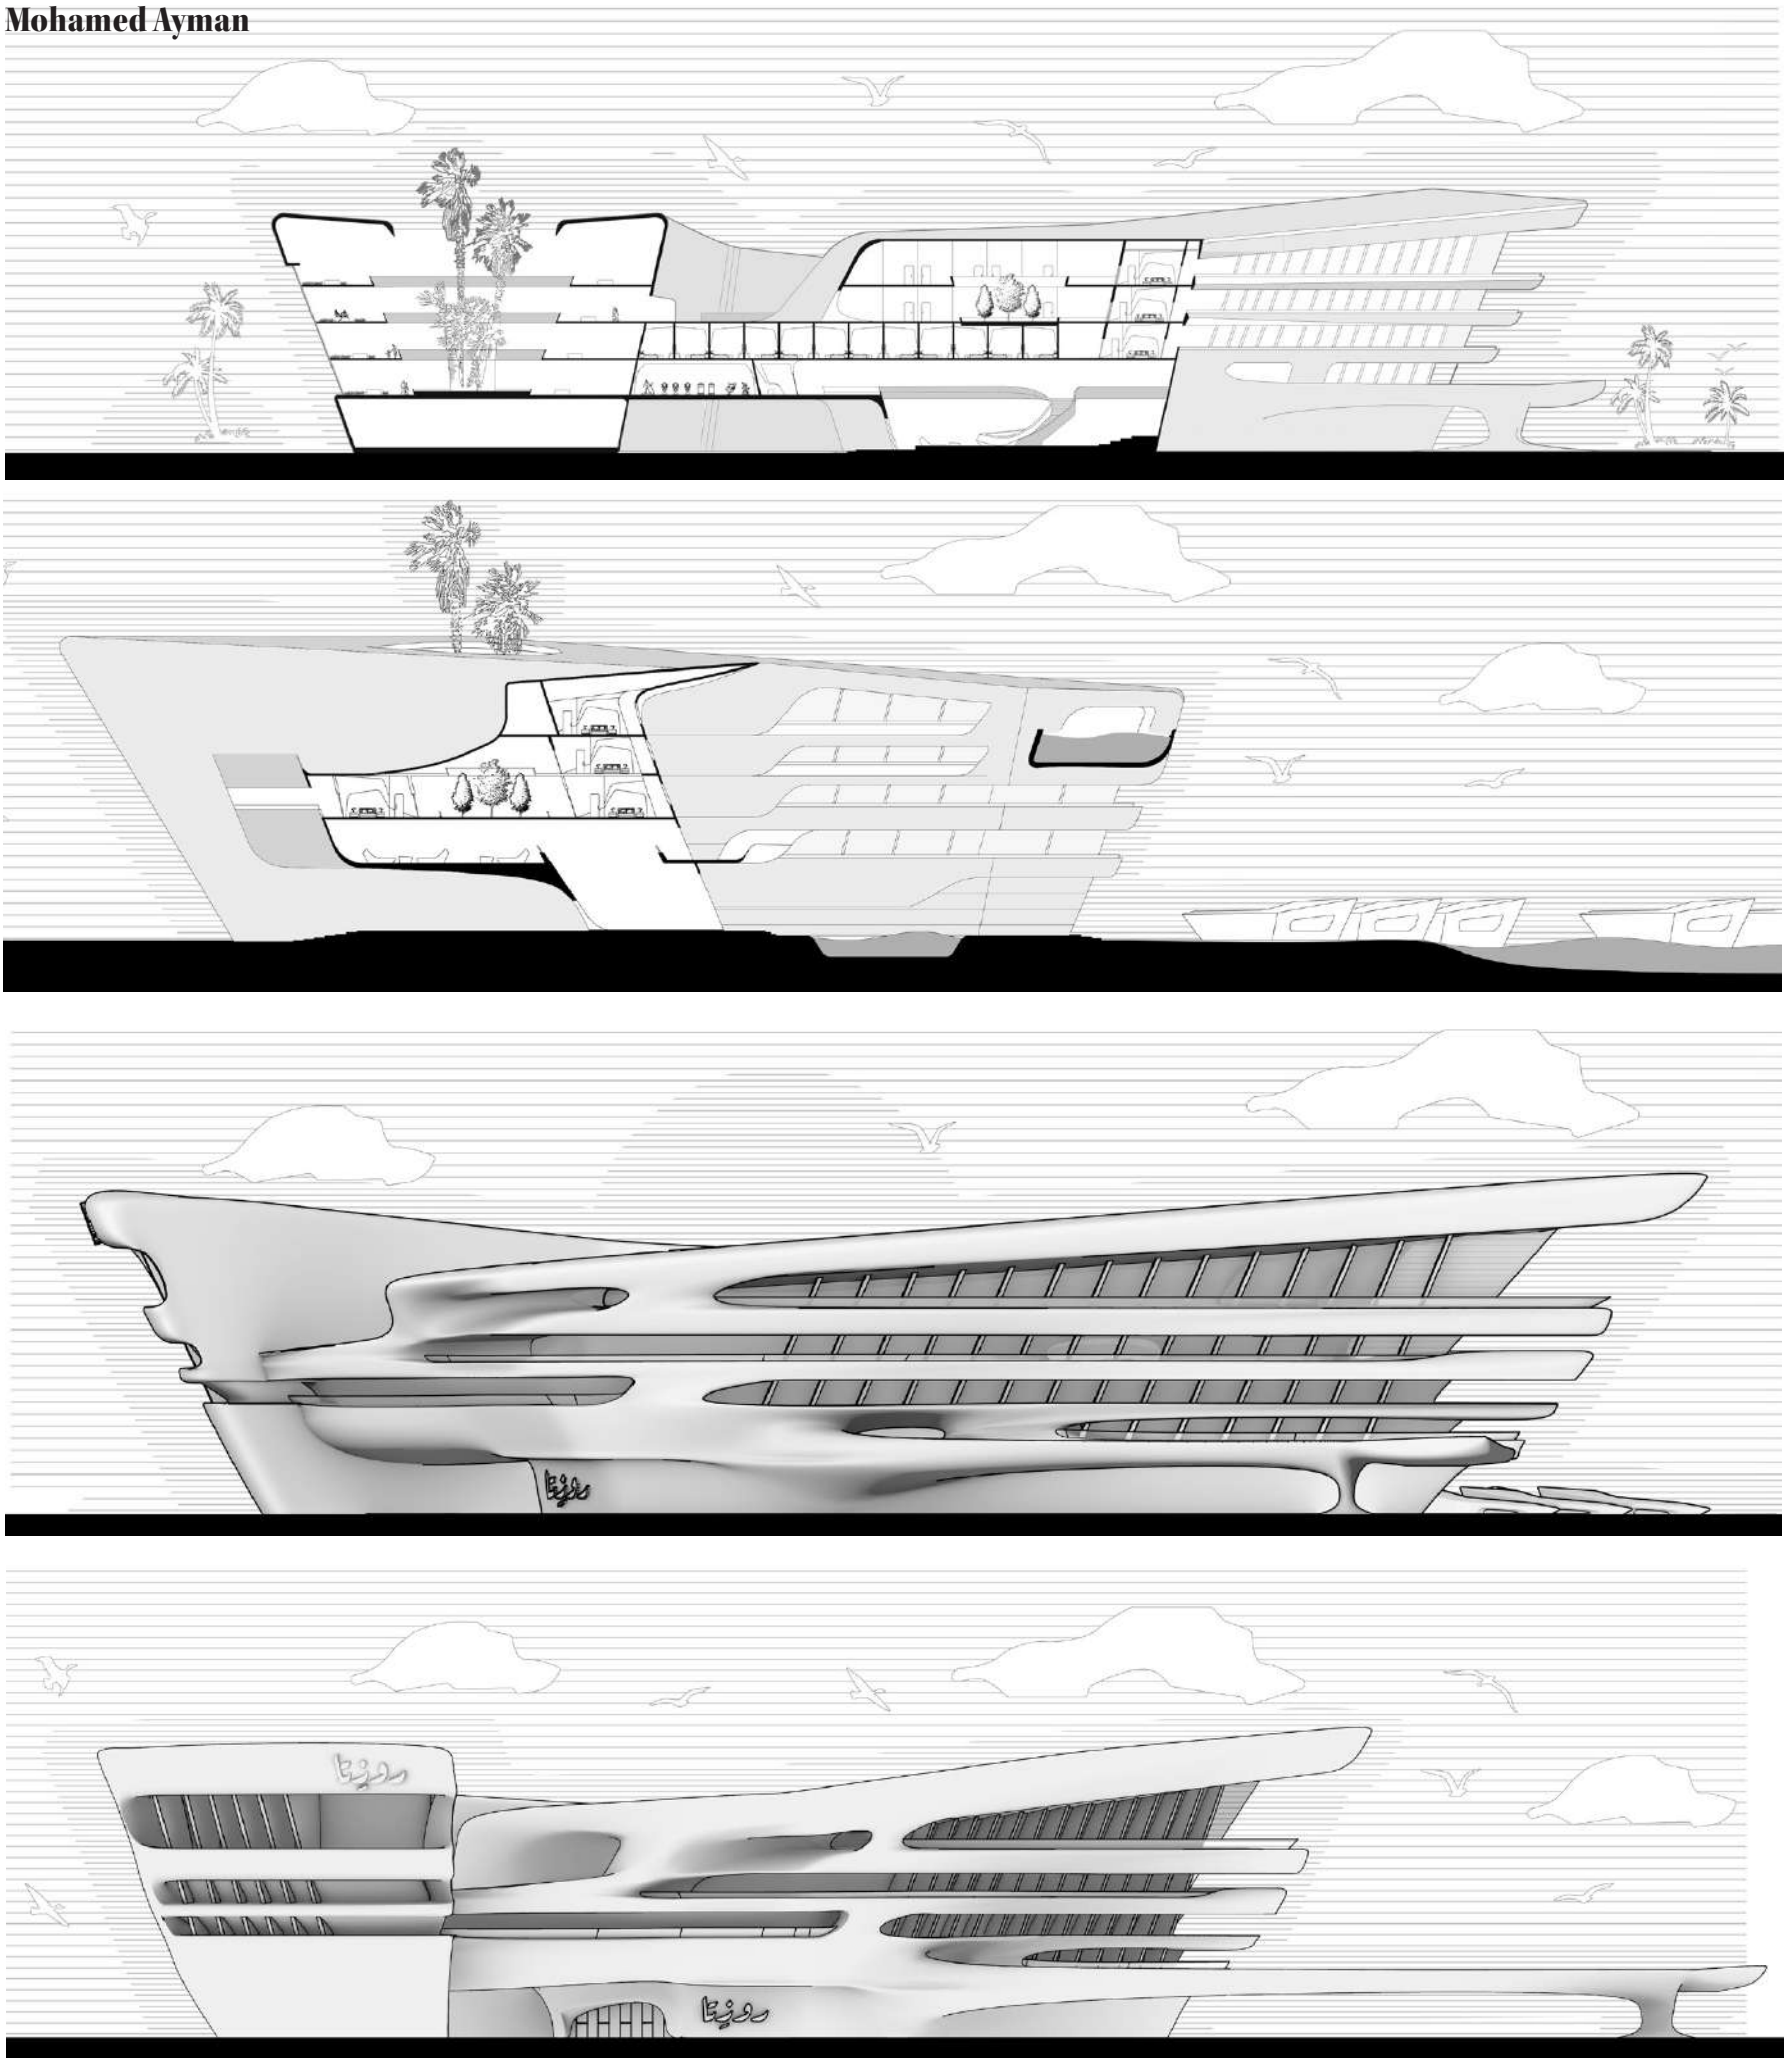

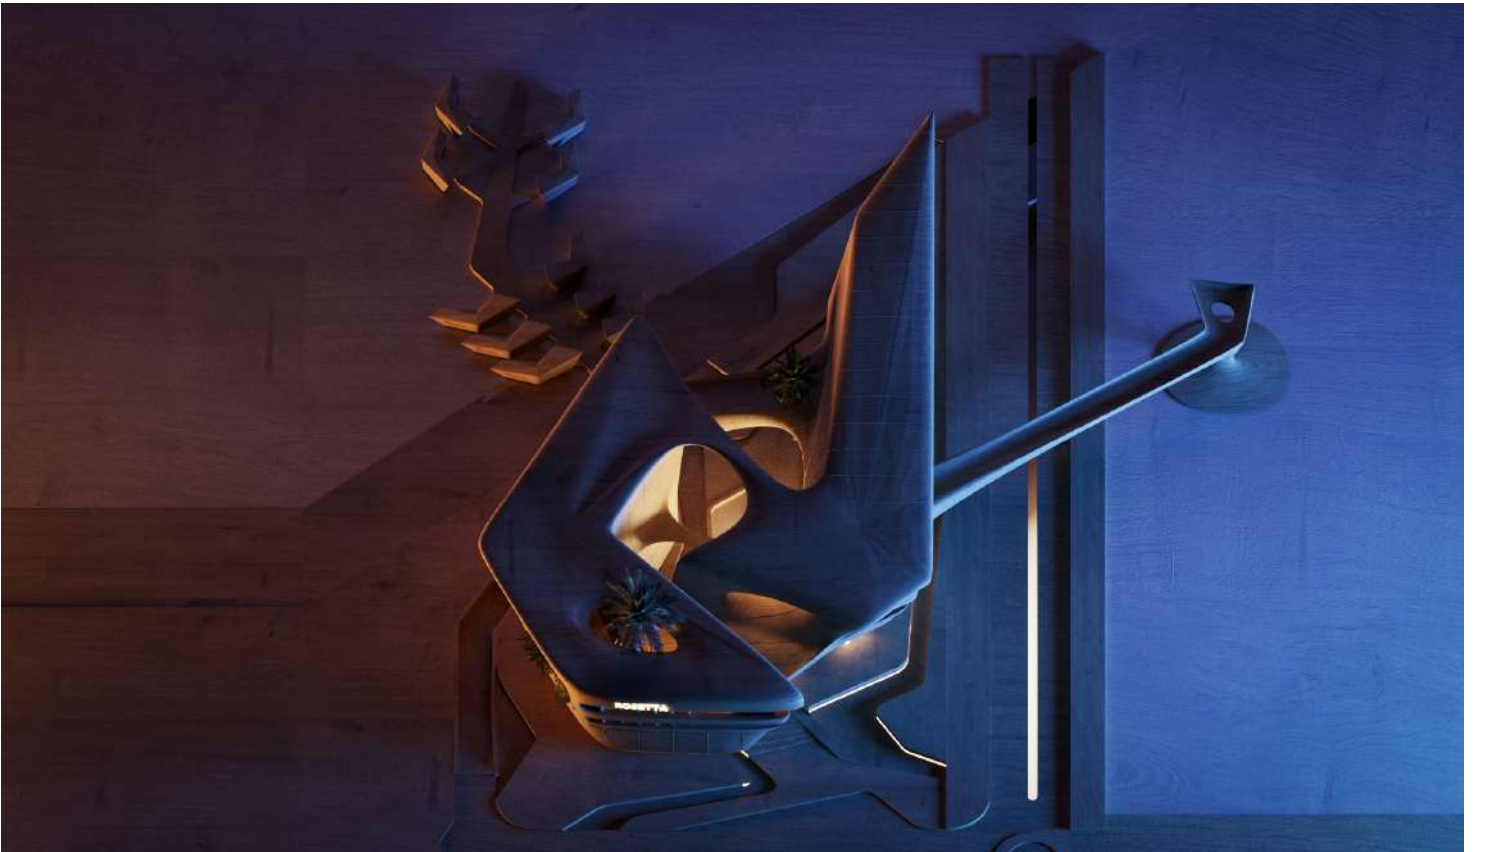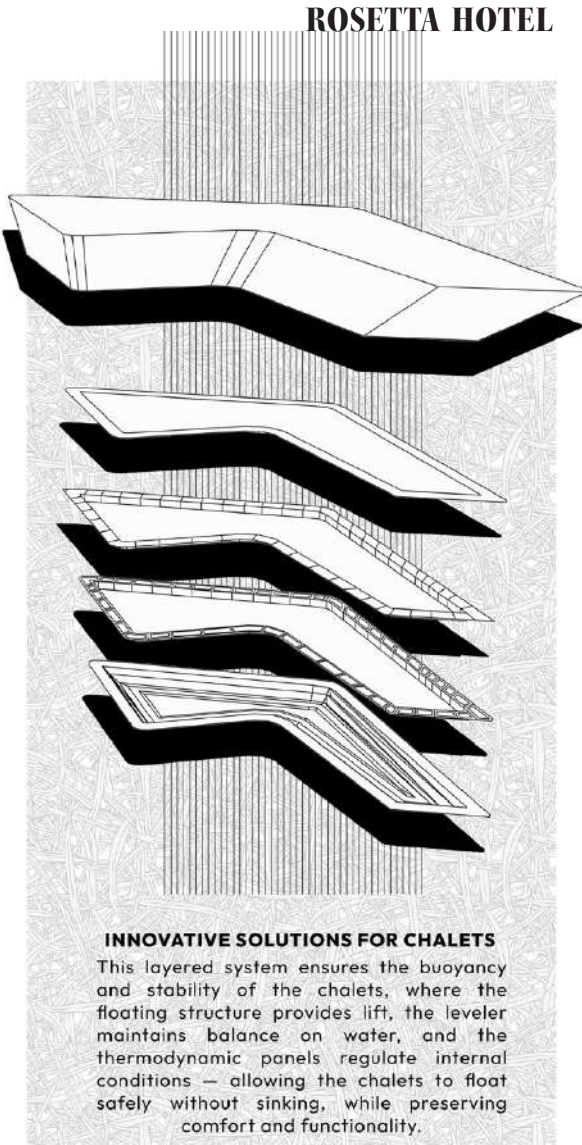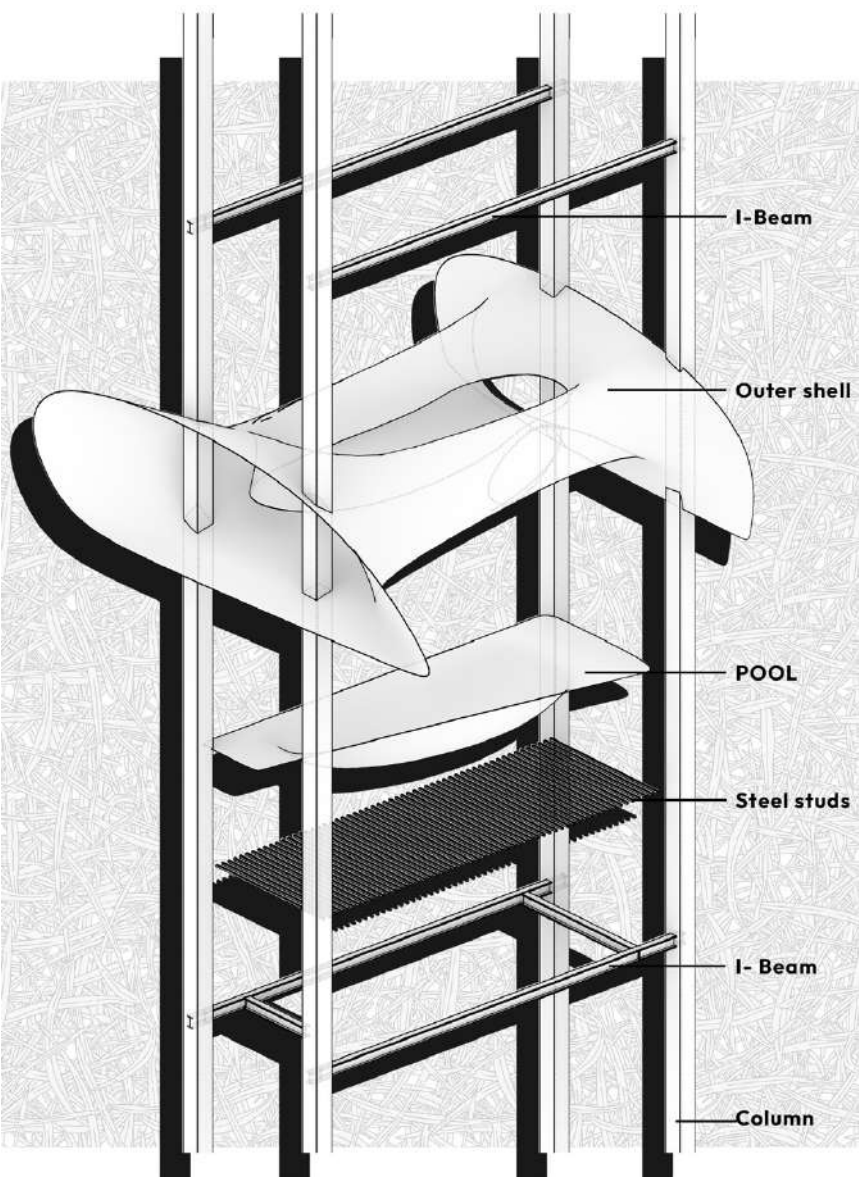



3

MIDAAR LIBRARY

ACADEMIC WORK

GRADUATION PROJECT

Ain Shams University, Faculty of Engineering

Year: 2026

Location: Mustakbal city, Egypt

Project: Hotel



Softwares: Rhino, 3Ds Max, Corona, Photoshop, Illustrator

Role: (Teamwork)

CONCEPT

“The Dialogue” is not merely a title — it is the essence of this architectural narrative. The project embodies the unique conversation between land and sea, between structure and flow, between the contained (indoor) and the limitless (outdoor). Inspired by Rashid’s unique geographical and historical context — where the Nile and Mediterranean meet — the design draws from this natural confluence, creating a fluid form that extends bridges out into the landscape, just as the Nile stretches into the sea

FORM GENERATION

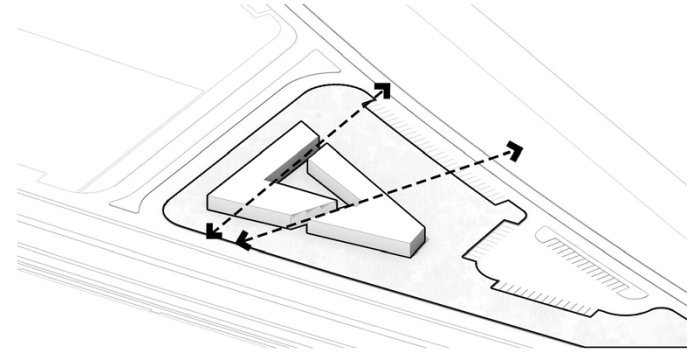
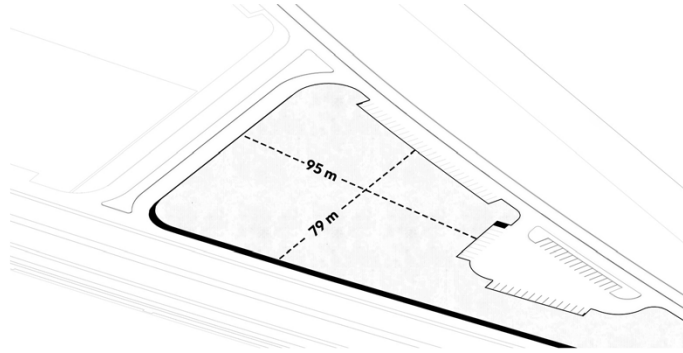


SITE ANALYSIS

Analyzed the site boundaries and dimensions.

FORM ORIENTATION

Oriented the building according to the site's geometry and circulation.

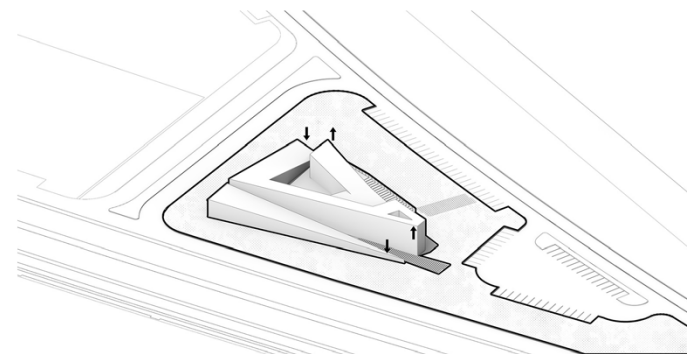
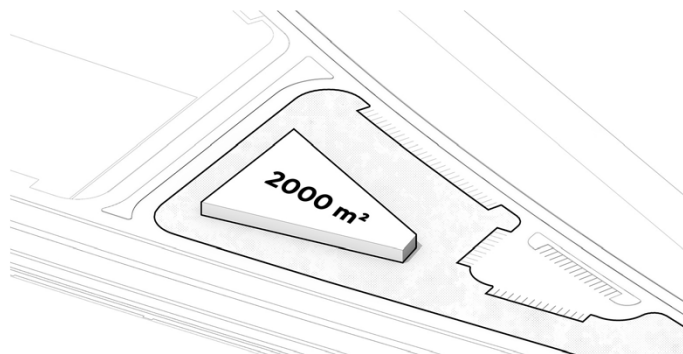


BUILDING FOOTPRINT

Defined a compact 2,000 m² building footprint.

SITE FORCES

Carved the form based on site forces, circulation, and main entrances.

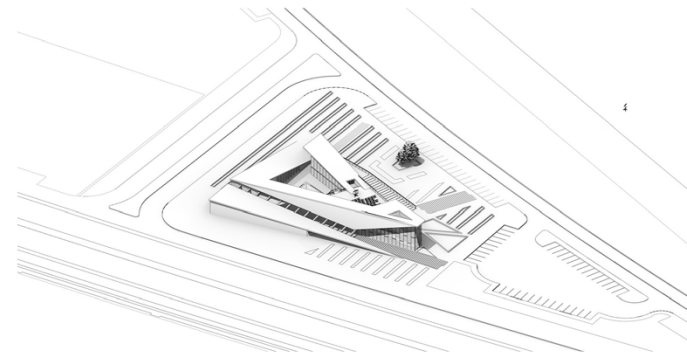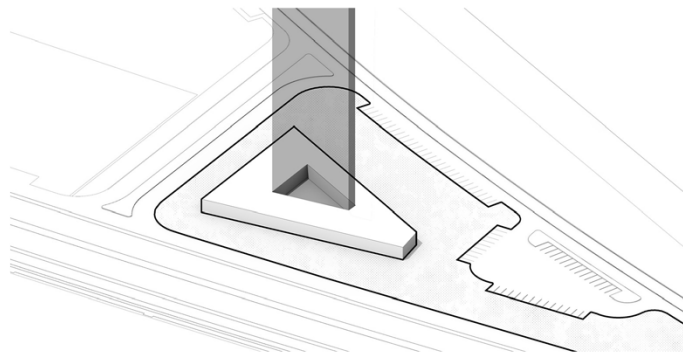

CONCEPT


Created the central void and accessible roof to express the concept and activate the rooftop.

FINAL INTEGRATION

Integrated landscape, circulation, and parking to complete the site design.


FROM CONSTRAINTS COMES CHARACTER

The form generation process responds to the site's geometry, circulation, and environmental forces. Starting from the site boundaries, the mass is shaped into a compact footprint, carved to create a central void, and finalized with an accessible roof that reinforces the project concept while integrating seamlessly with the surrounding landscape.



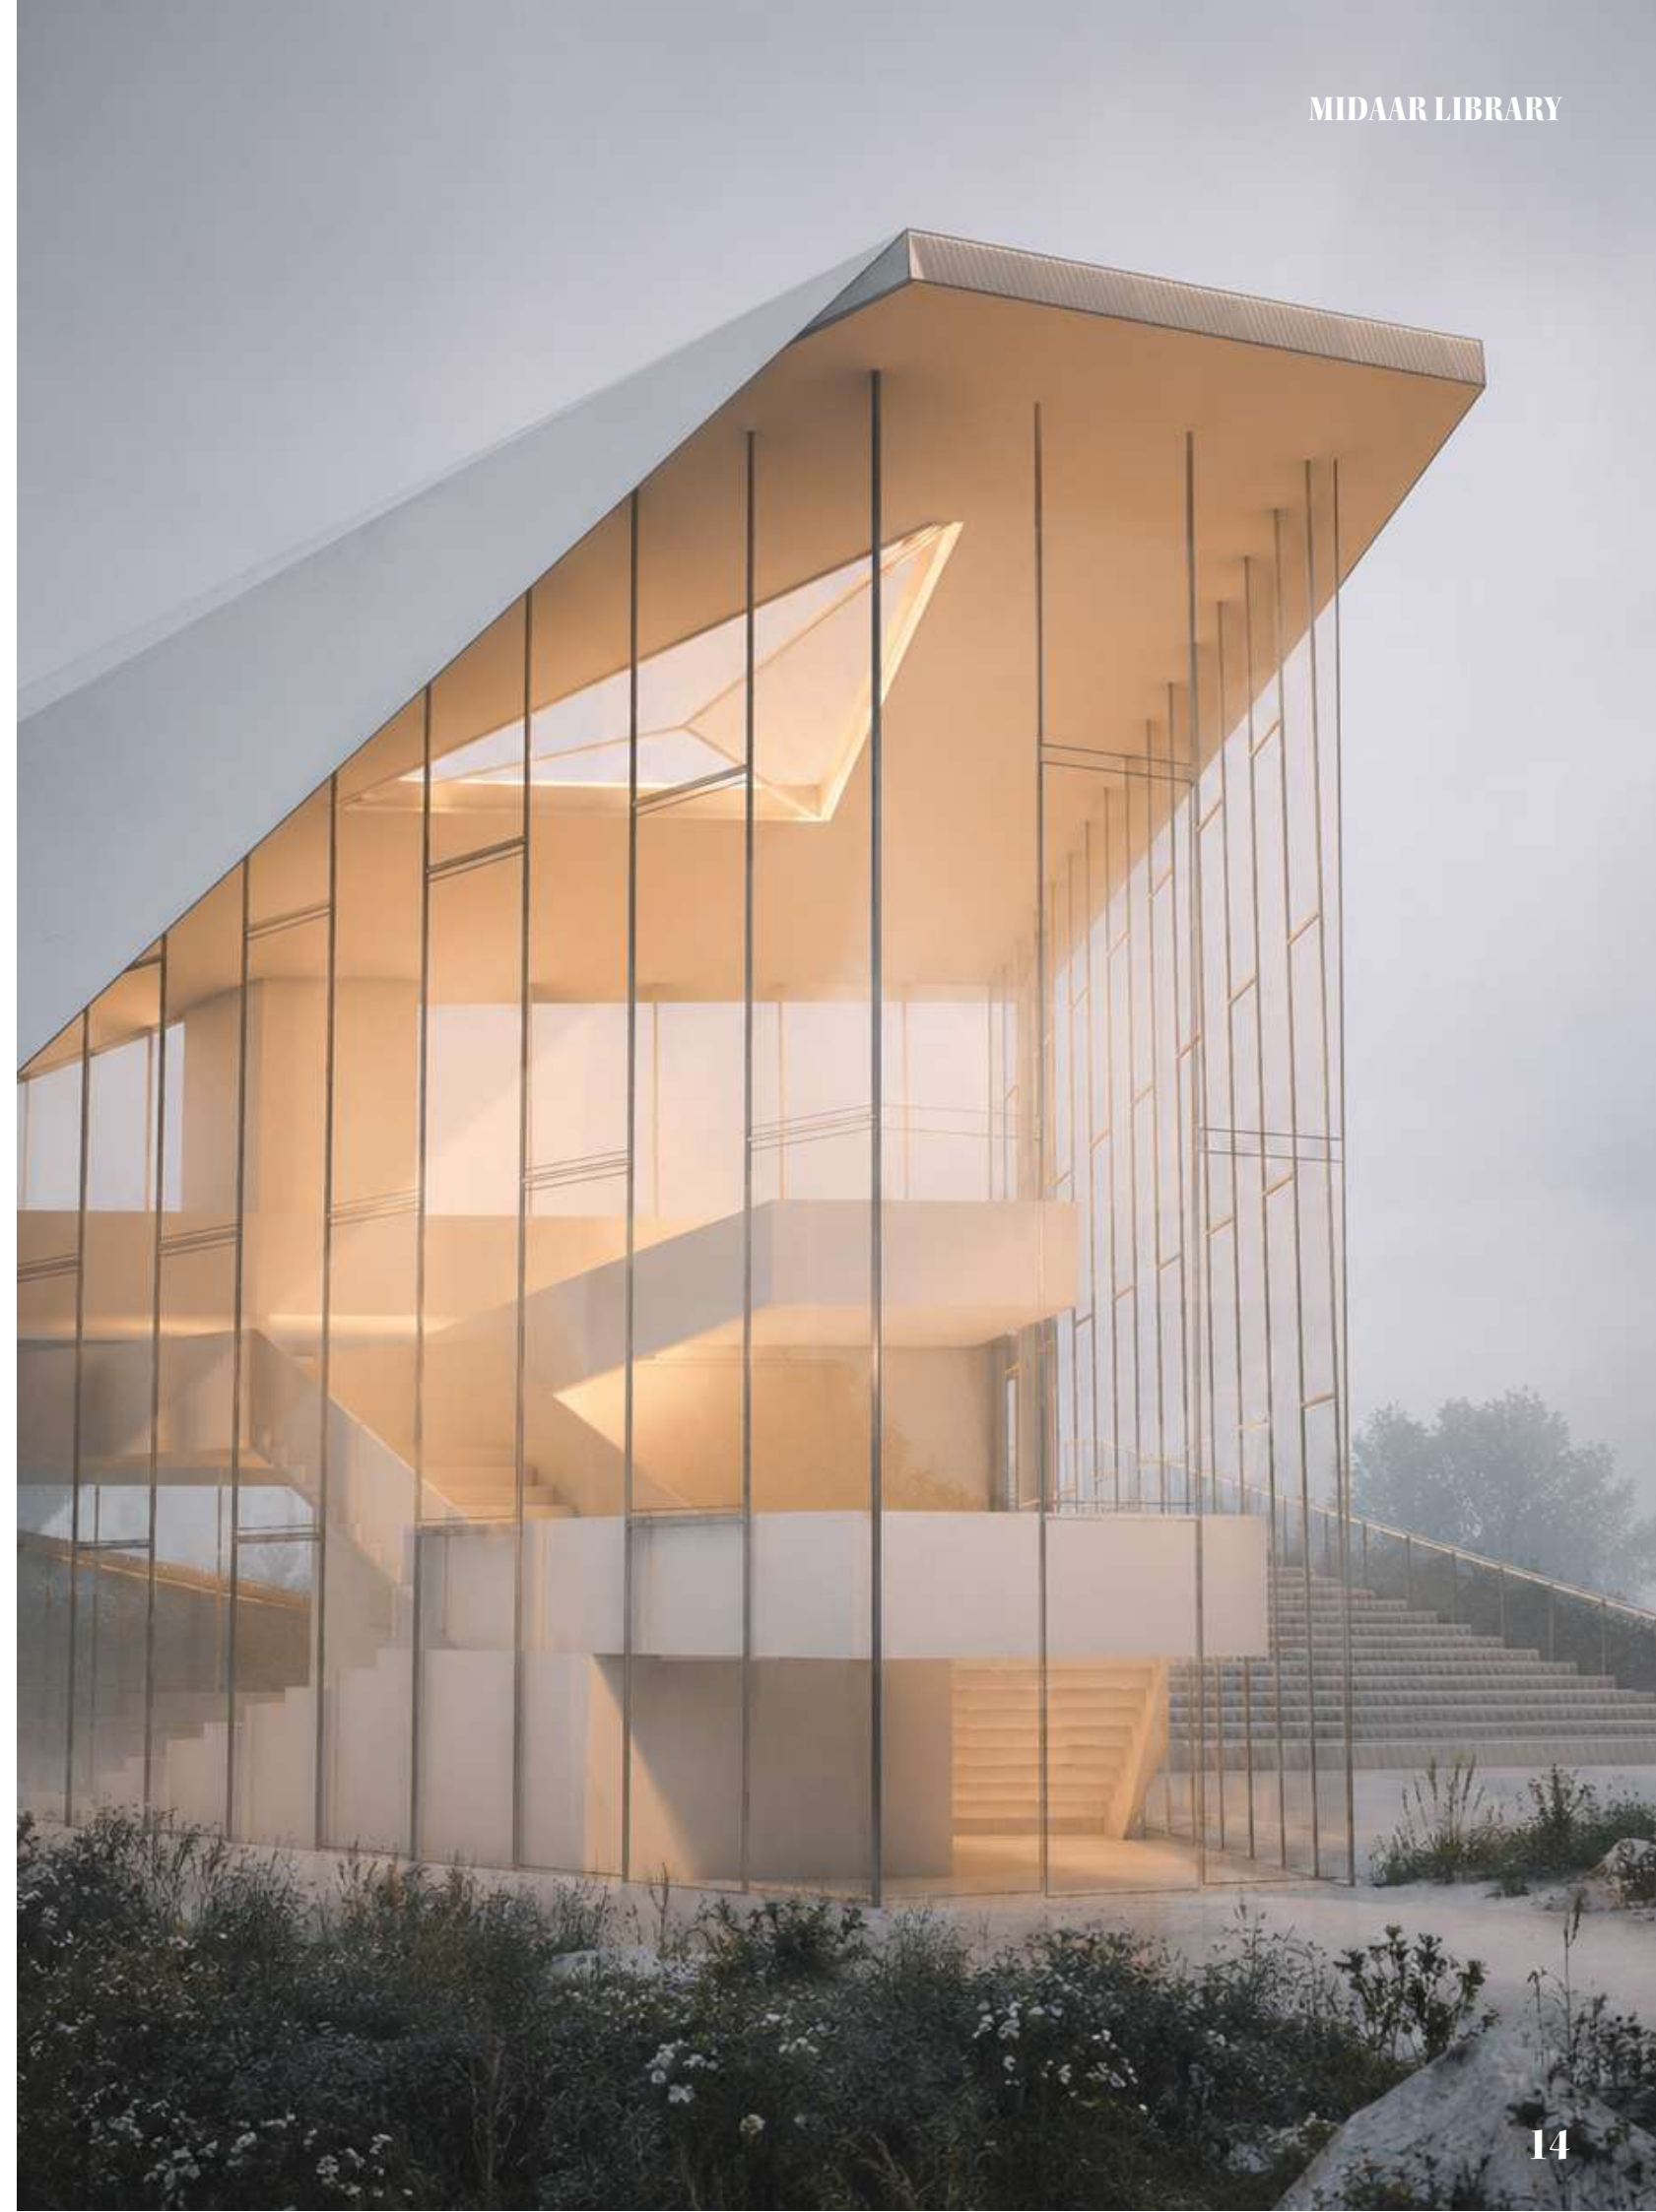





Northern Elevation

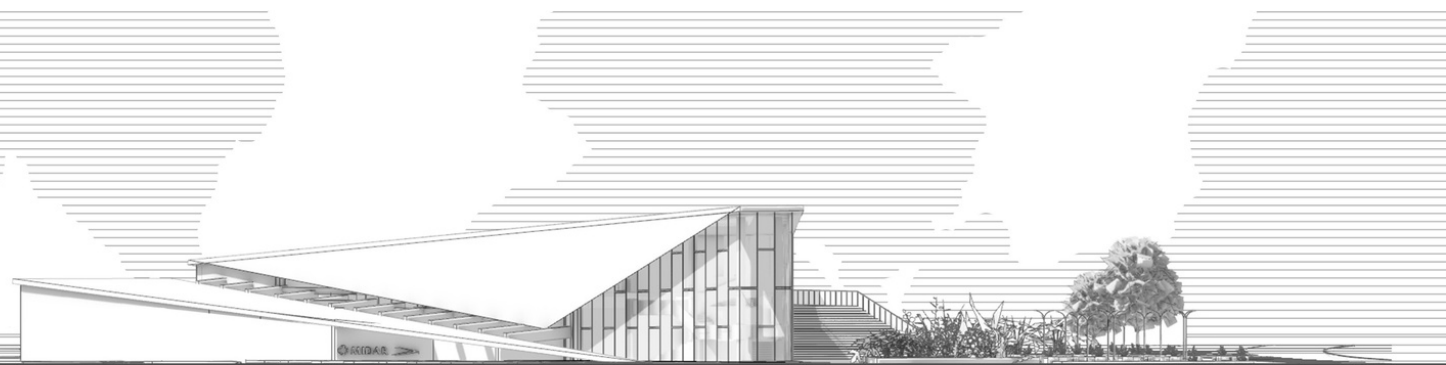


Street Elevation

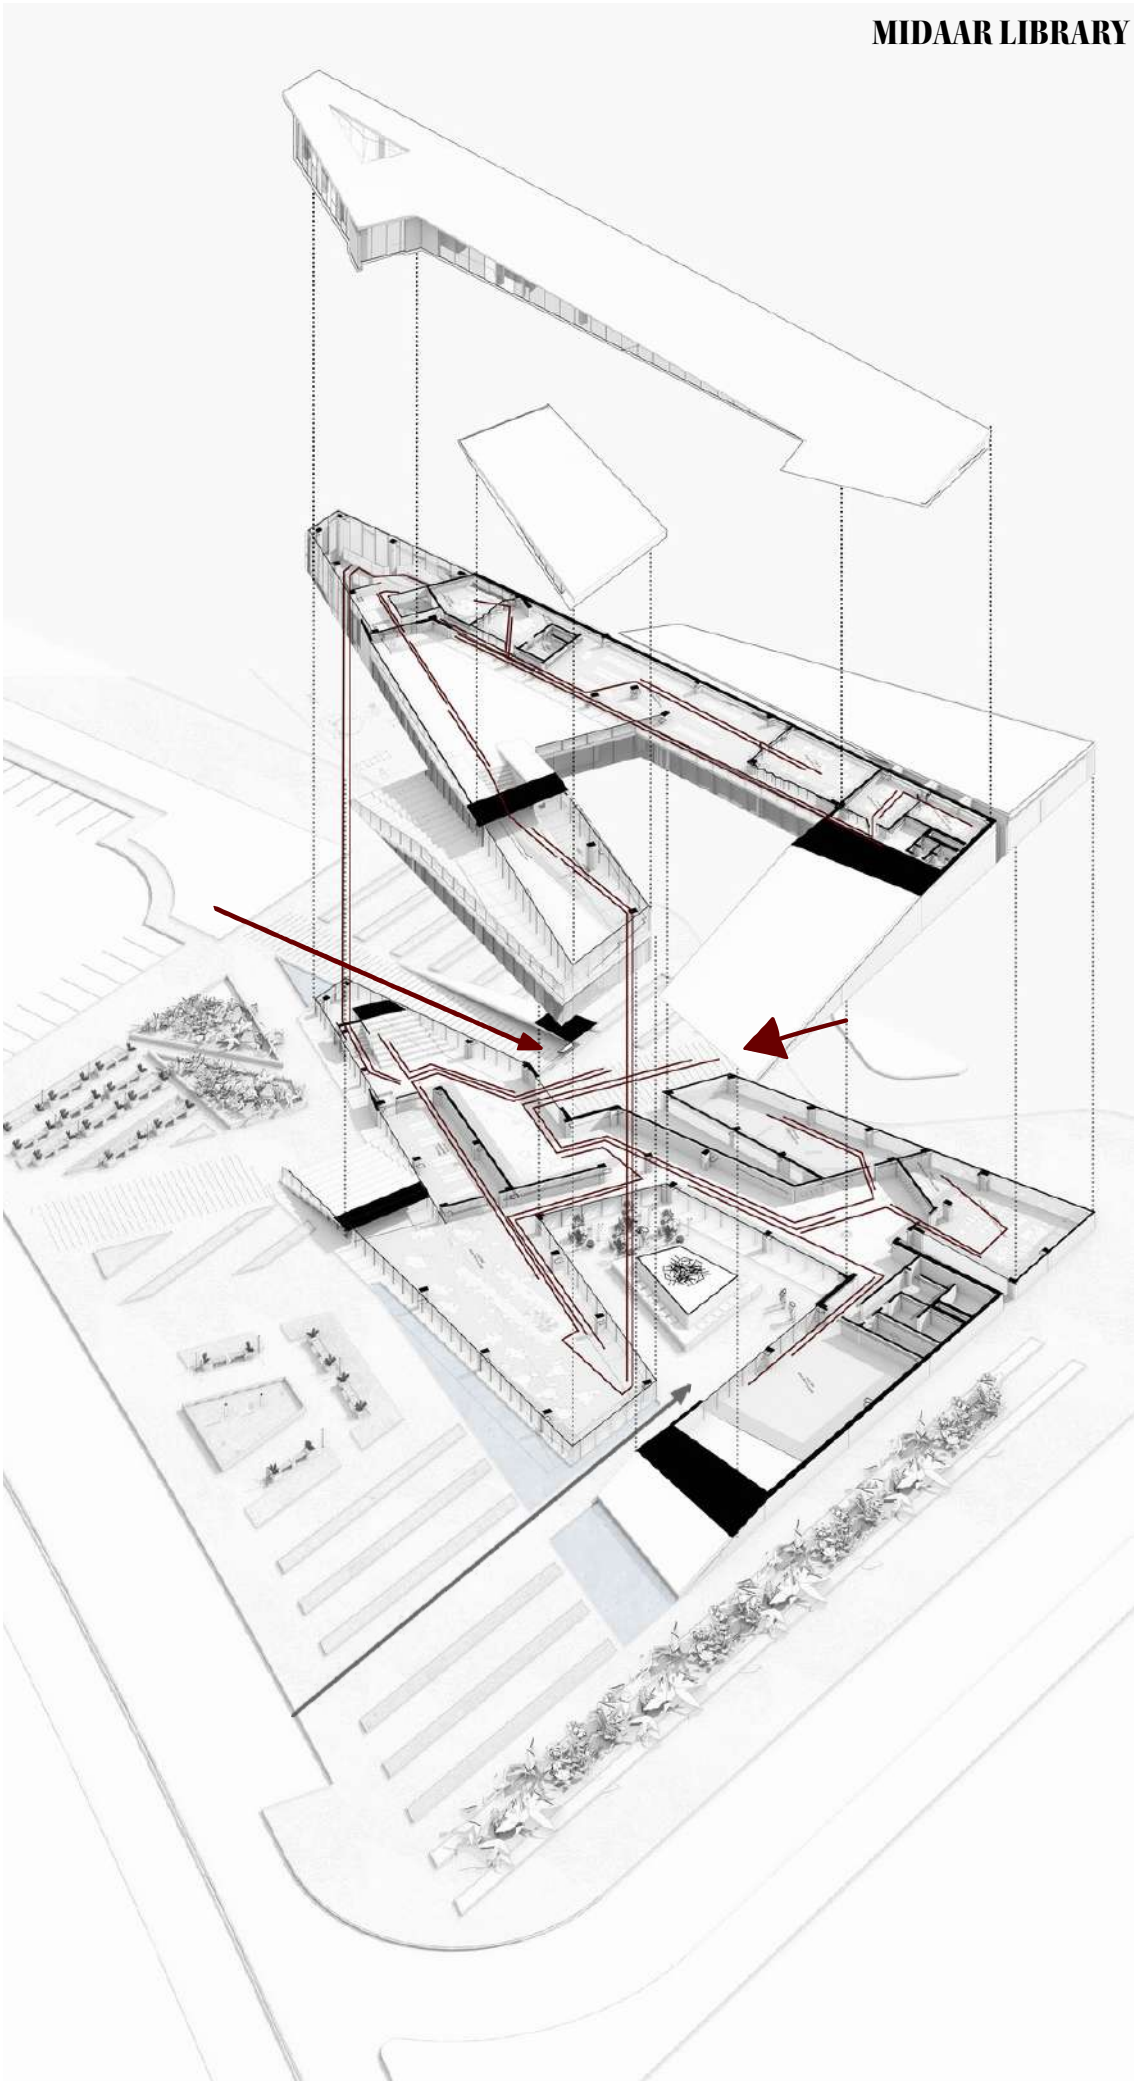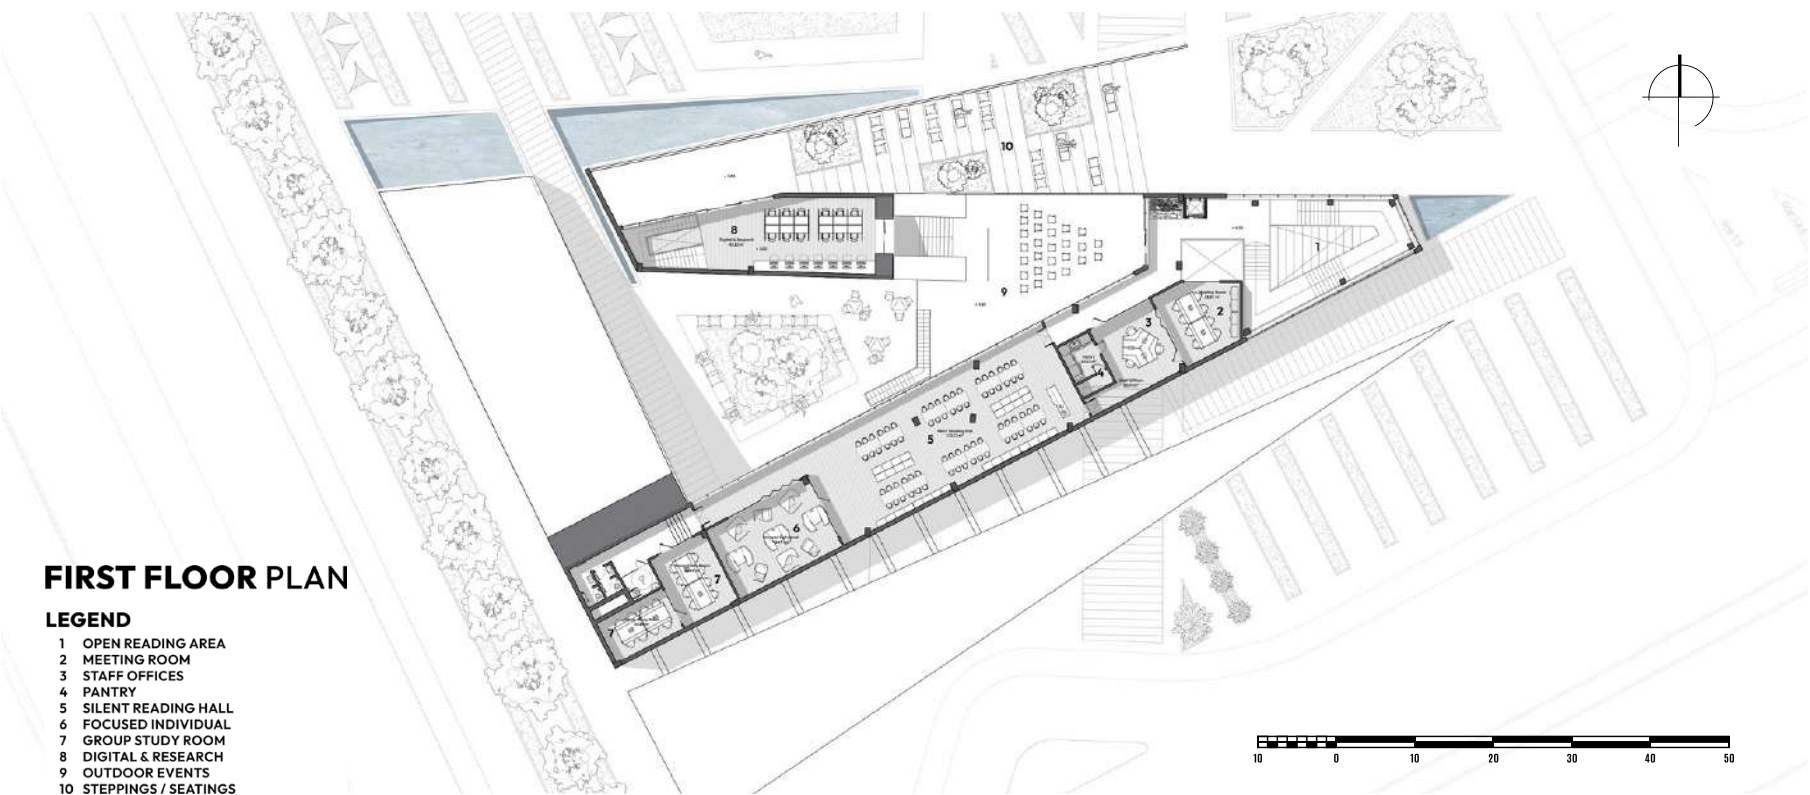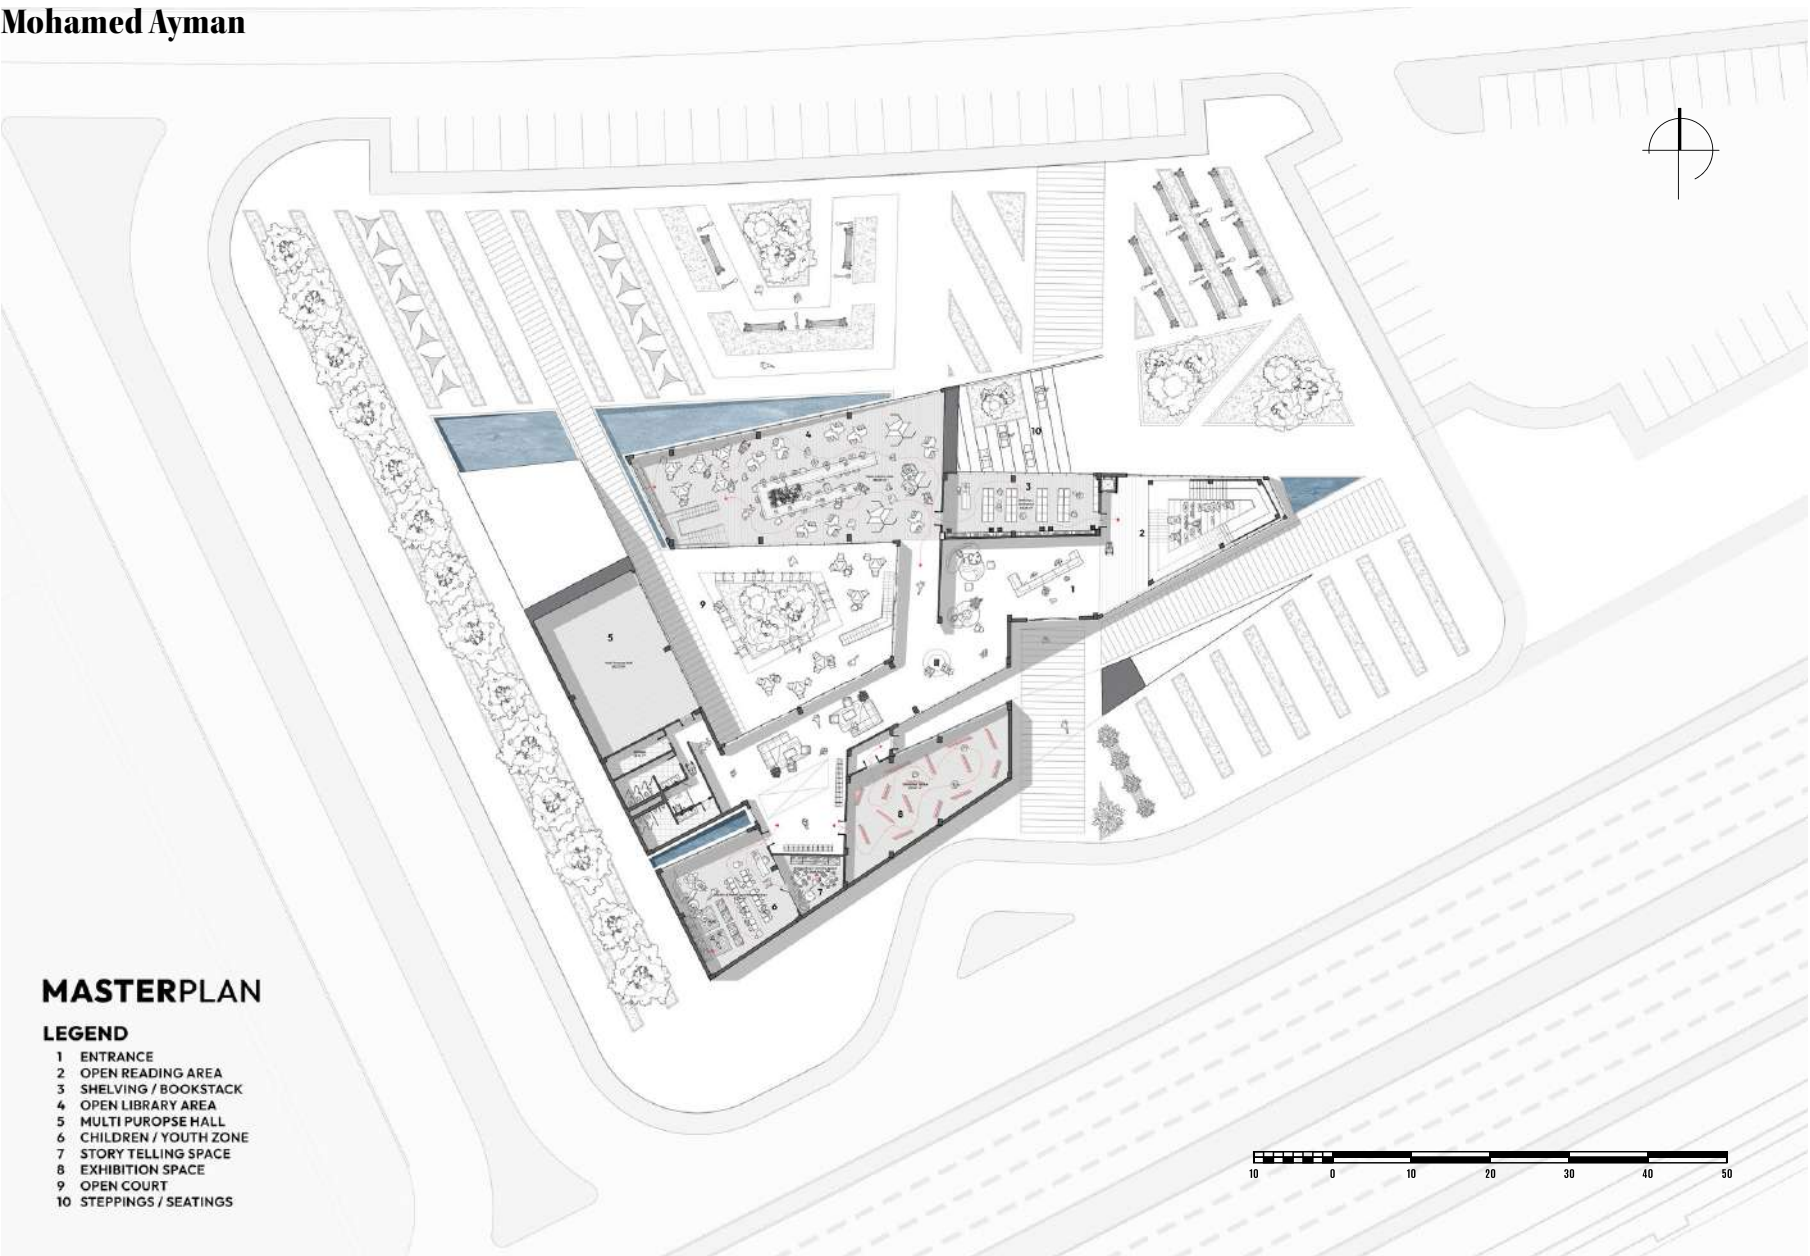

INDOOR STAIR

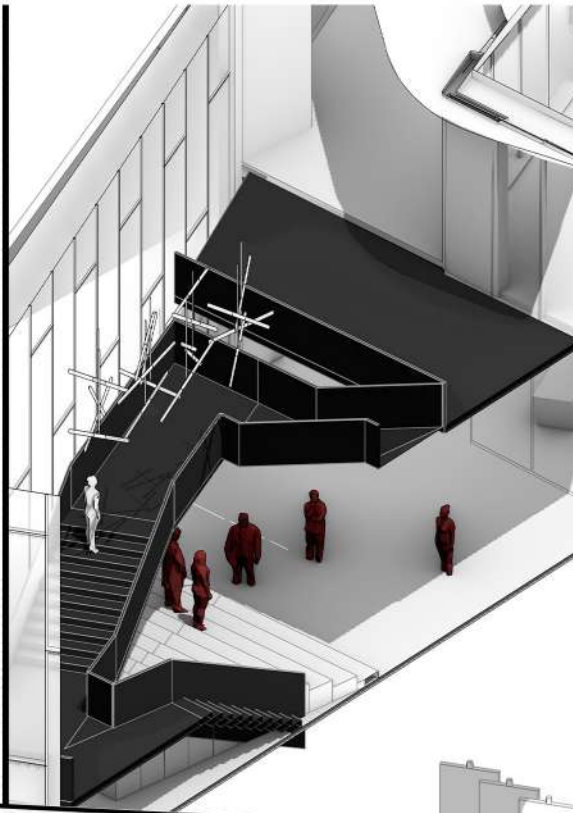


OUTDOOR EVENTS

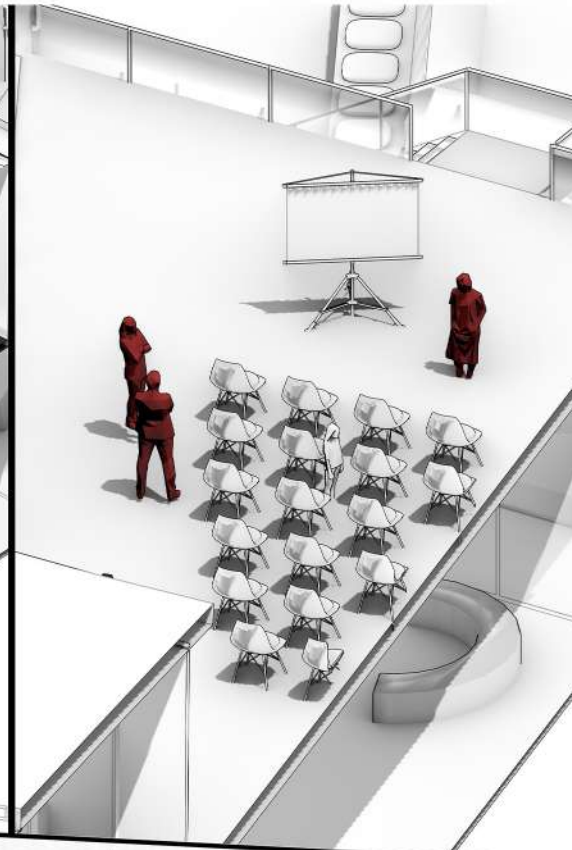

STAIR COURT




COURT

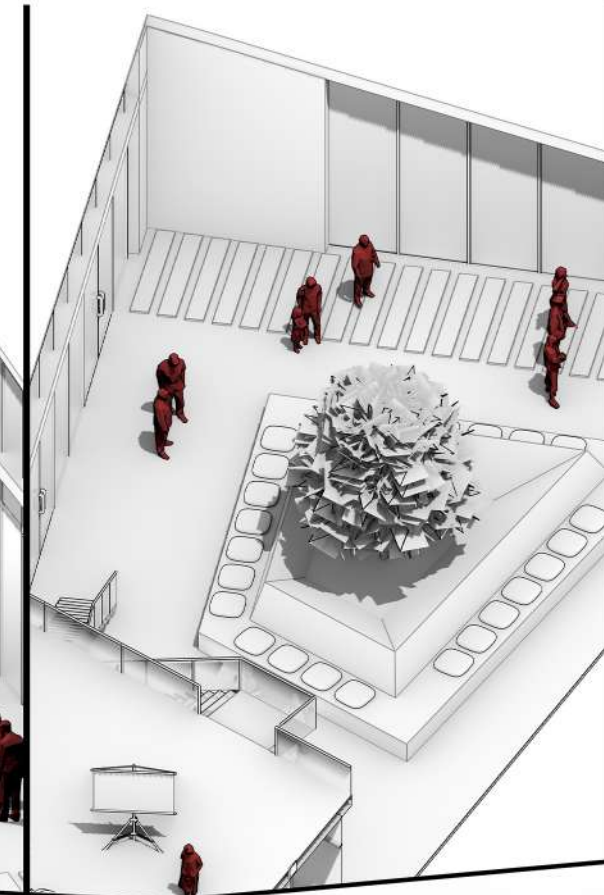


3D SECTION

BEYOND CIRCULATION

The section illustrates a continuous sequence of educational, social, and recreational spaces connected by a dynamic circulation spine. It includes flexible lecture and workshop areas, collaborative gathering spaces, informal lounges, and a central courtyard that introduces daylight and greenery, creating an engaging environment that encourages interaction, learning, and community activities.

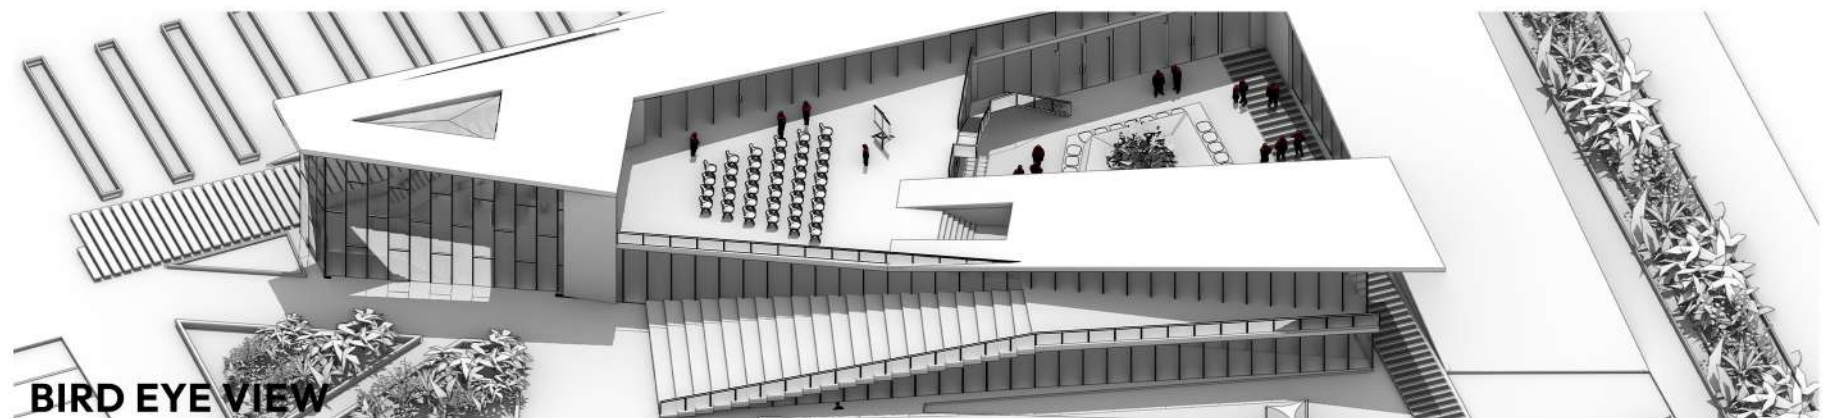

BIRD EYE VIEW

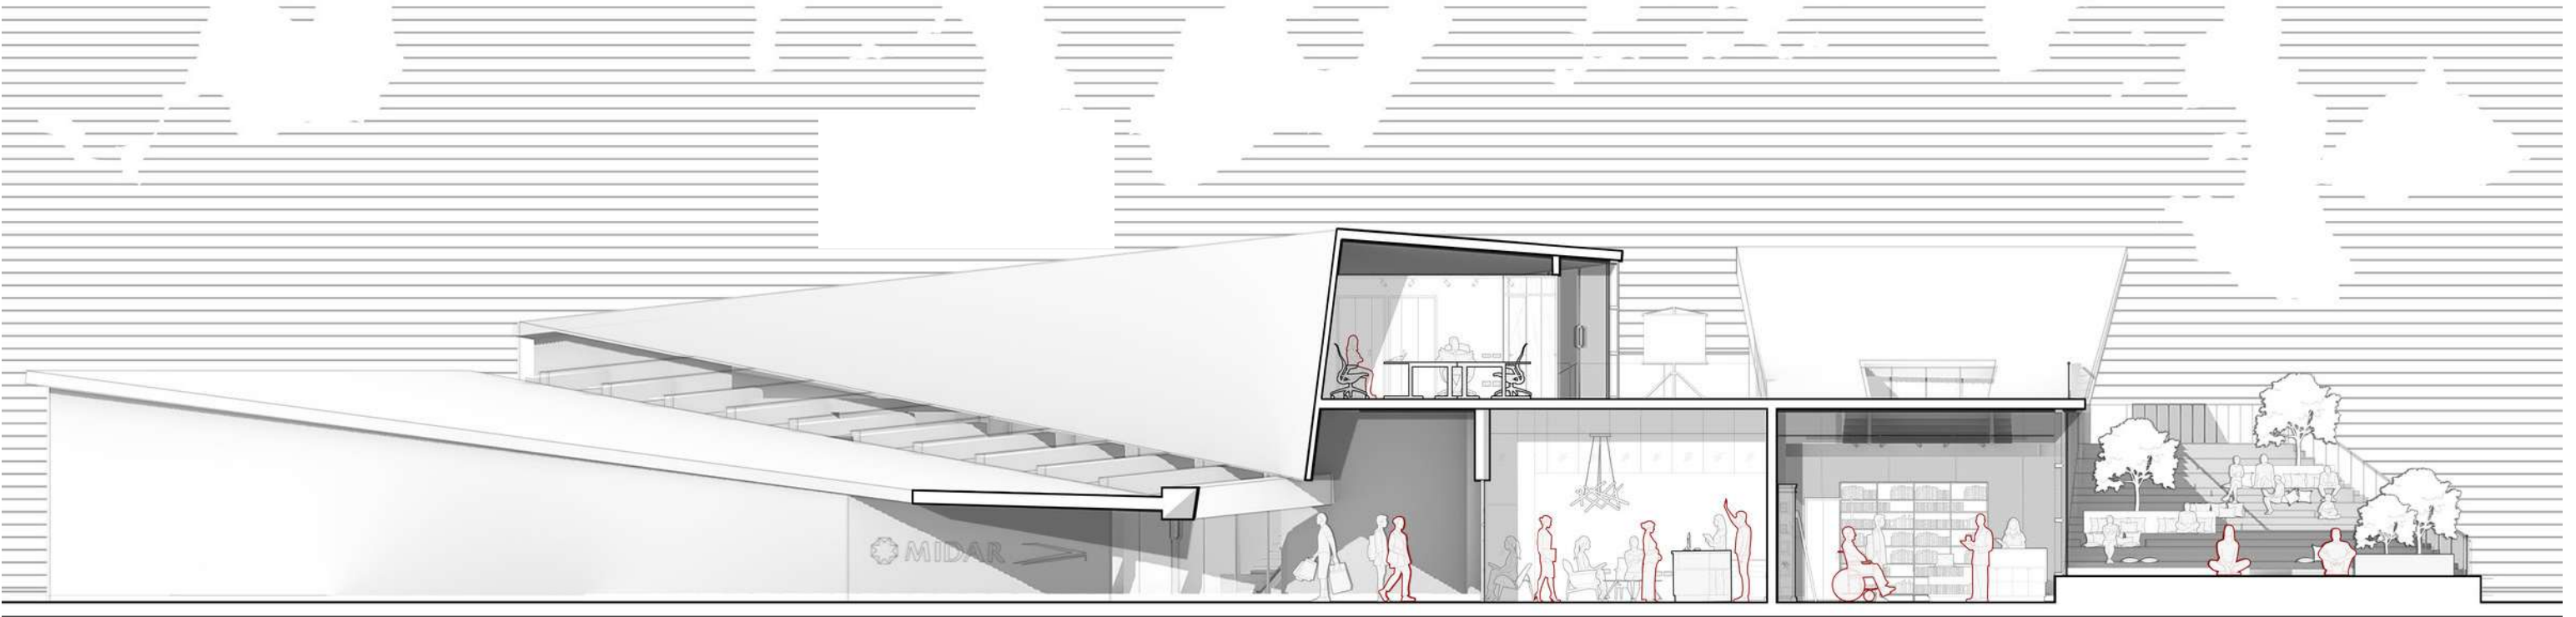



4

AL-GHEYA

FIRST Place, Egypt Urban Oasis Competition
organized by: REC & BASE STUDIO

Year: 2025

Location: Al-Muiz, Cairo, Egypt

Typology: Urban Retreat

Softwares: Rhino, Grasshoper, Corona, Photoshop

Role: (Teamwork)

-Workin on Design and Visualization

BRIEF

In the dense, pulsating heart of historic Old Cairo, where EL Moez Street's vibrant tapestry of tourism, culture, and daily Life strains under pressure and heat, an innovative vertical escape emerges. Facing critical ground-space lack, we transform neglected rooftops into a modular, affordable network of community micro-oases. Inspired by the district's iconic, socially catalytic pigeon towers, our design reimagines this vertical vernacular. We propose lightweight, accessible structures echoing the towers' form and materiality, creating a harmonious yet contemporary landmark.

In the dense, pulsating heart of historic Old Cairo, where El Moez Street's vibrant tapestry of tourism, culture, and daily life strains under pressure and heat, an innovative vertical escape emerges. Facing critical ground-space lack, we transform neglected rooftops into a modular, affordable network of community micro-oases.



Inspired by the district's iconic, socially catalytic pigeon towers, our design reimagines this vertical vernacular. We propose lightweight, accessible structures echoing the towers' form and materiality, creating a harmonious yet contemporary landmark.




Our initiative is based in historic El Moez Street, a culturally rich area facing modern issues like traffic and limited public spaces. We plan to convert neglected rooftops into peaceful areas, working alongside a renovated commercial building to enhance accessibility and success while revitalizing this urban space.



Site Catalysts: traditional; pigeon towers, free and abandoned roofs

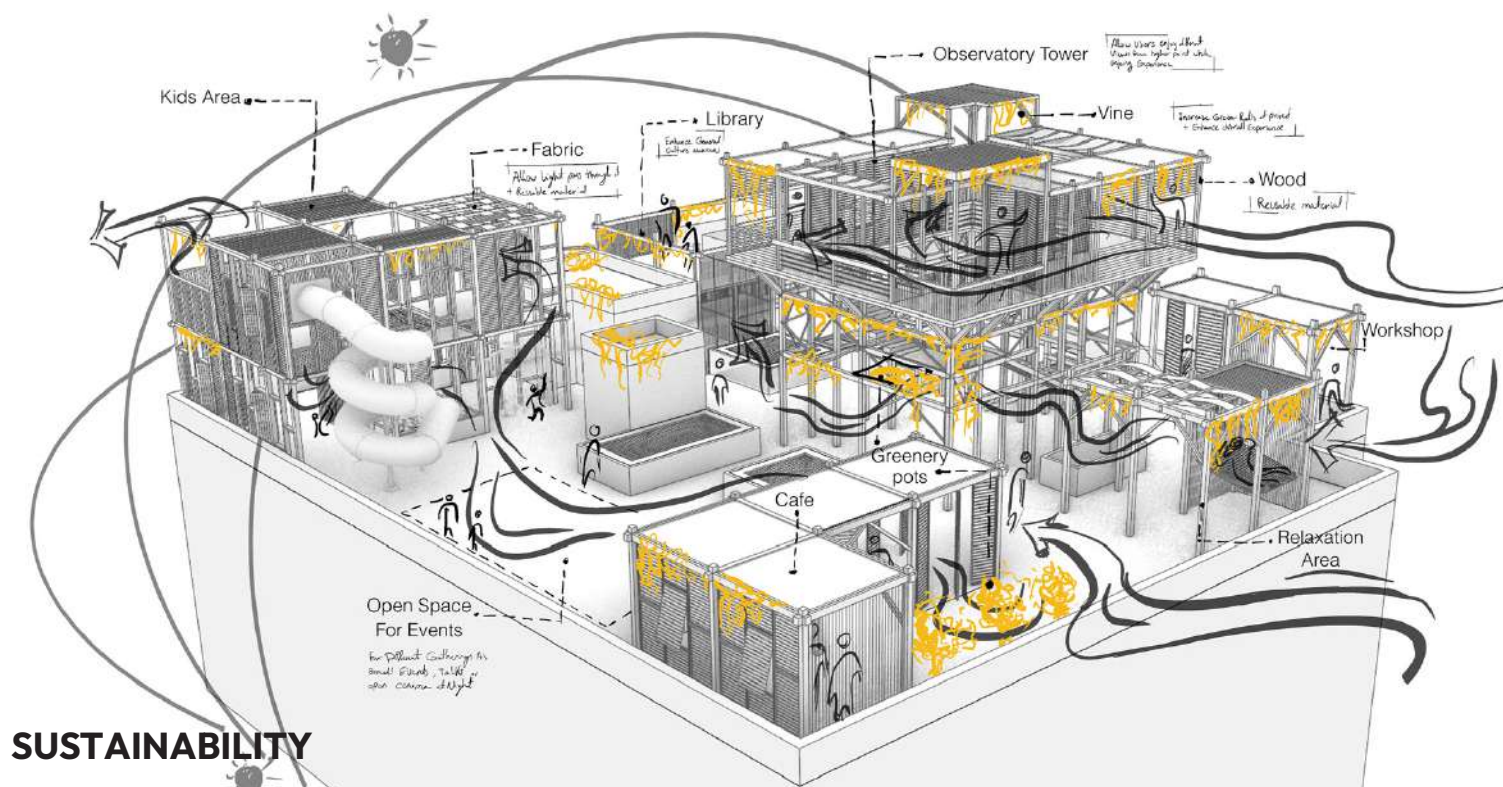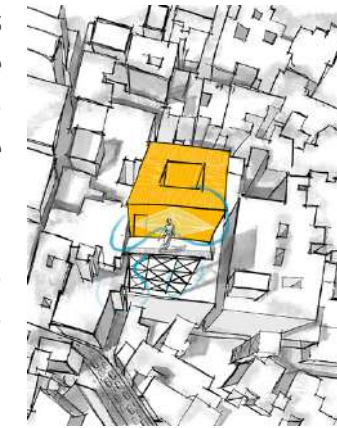


MASTER PLAN

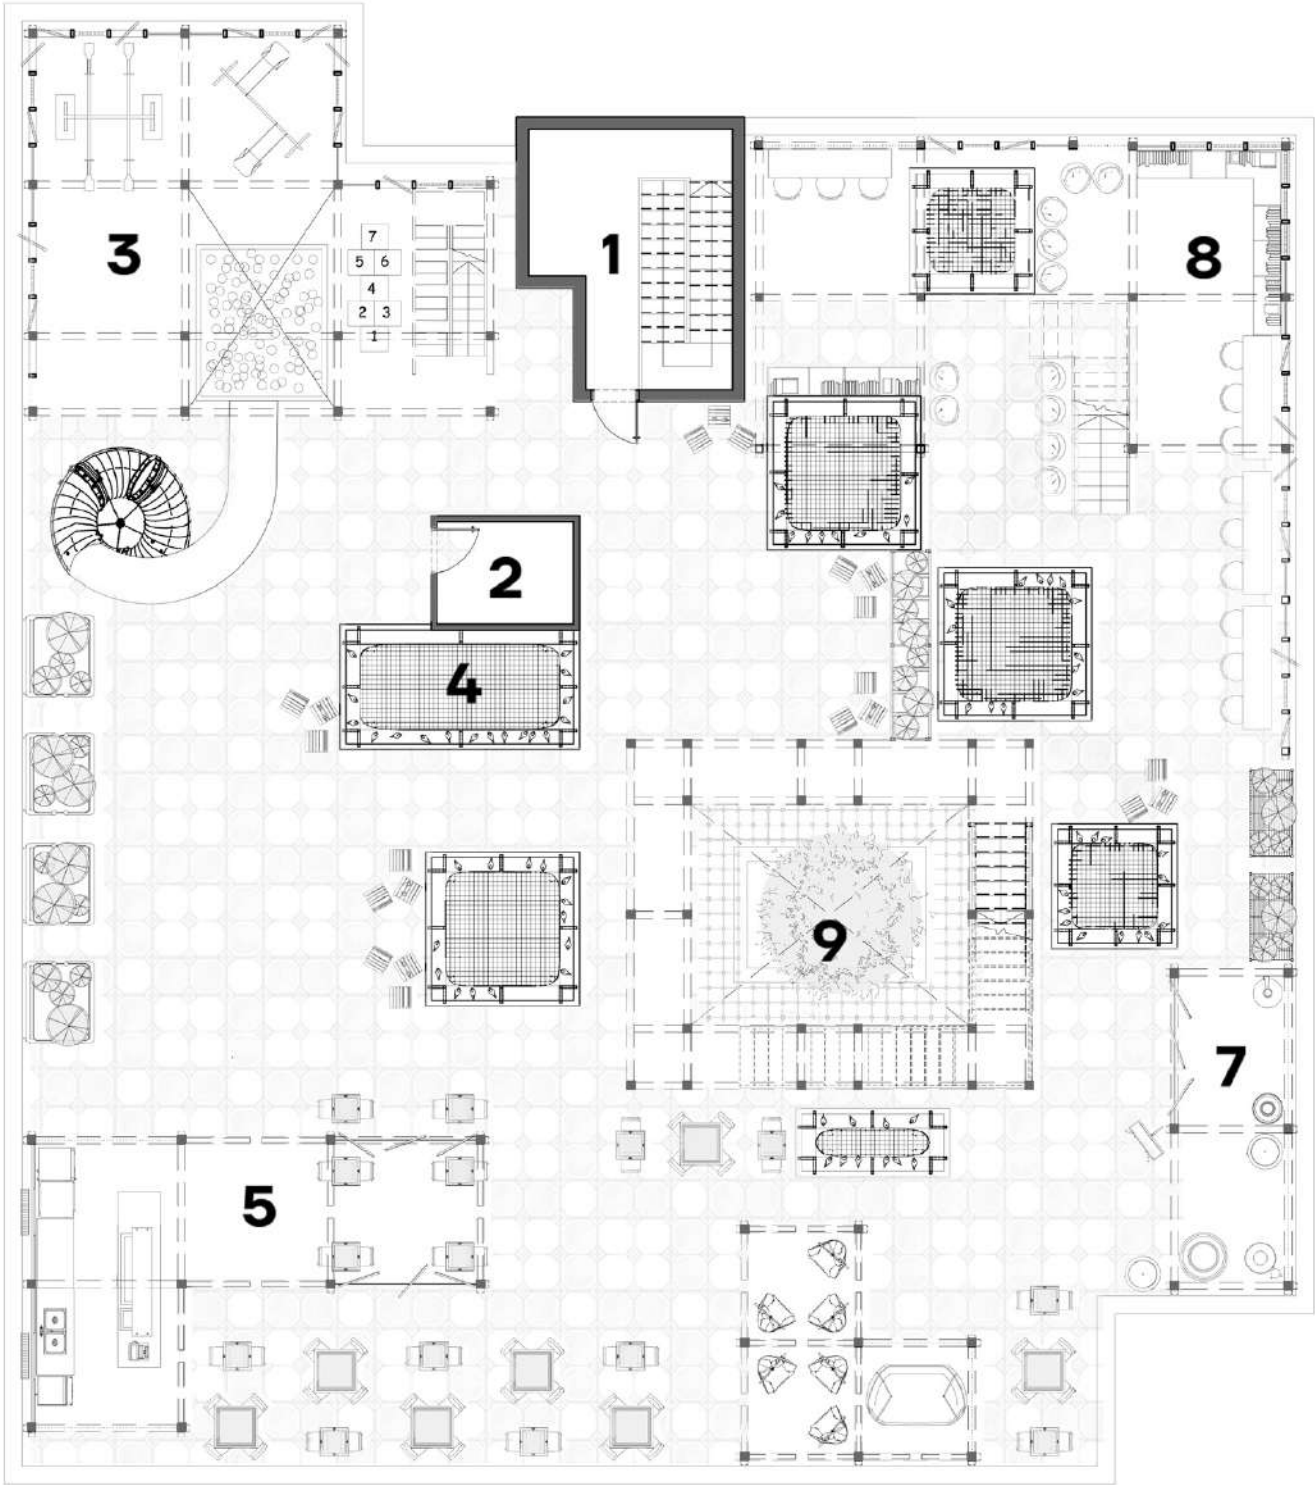



LEGEND

- | | | |
|------------------|------------------------------|----------------------|
| 1. Stair case | 5. Communal Cafeteria | 9. Observation tower |
| 2. Service room | 6. Hanged seatings | 10. Open space |
| 3. Kids area | 7. Pavilion | |
| 4. Pigeon stands | 8. Reading area and workshop | |




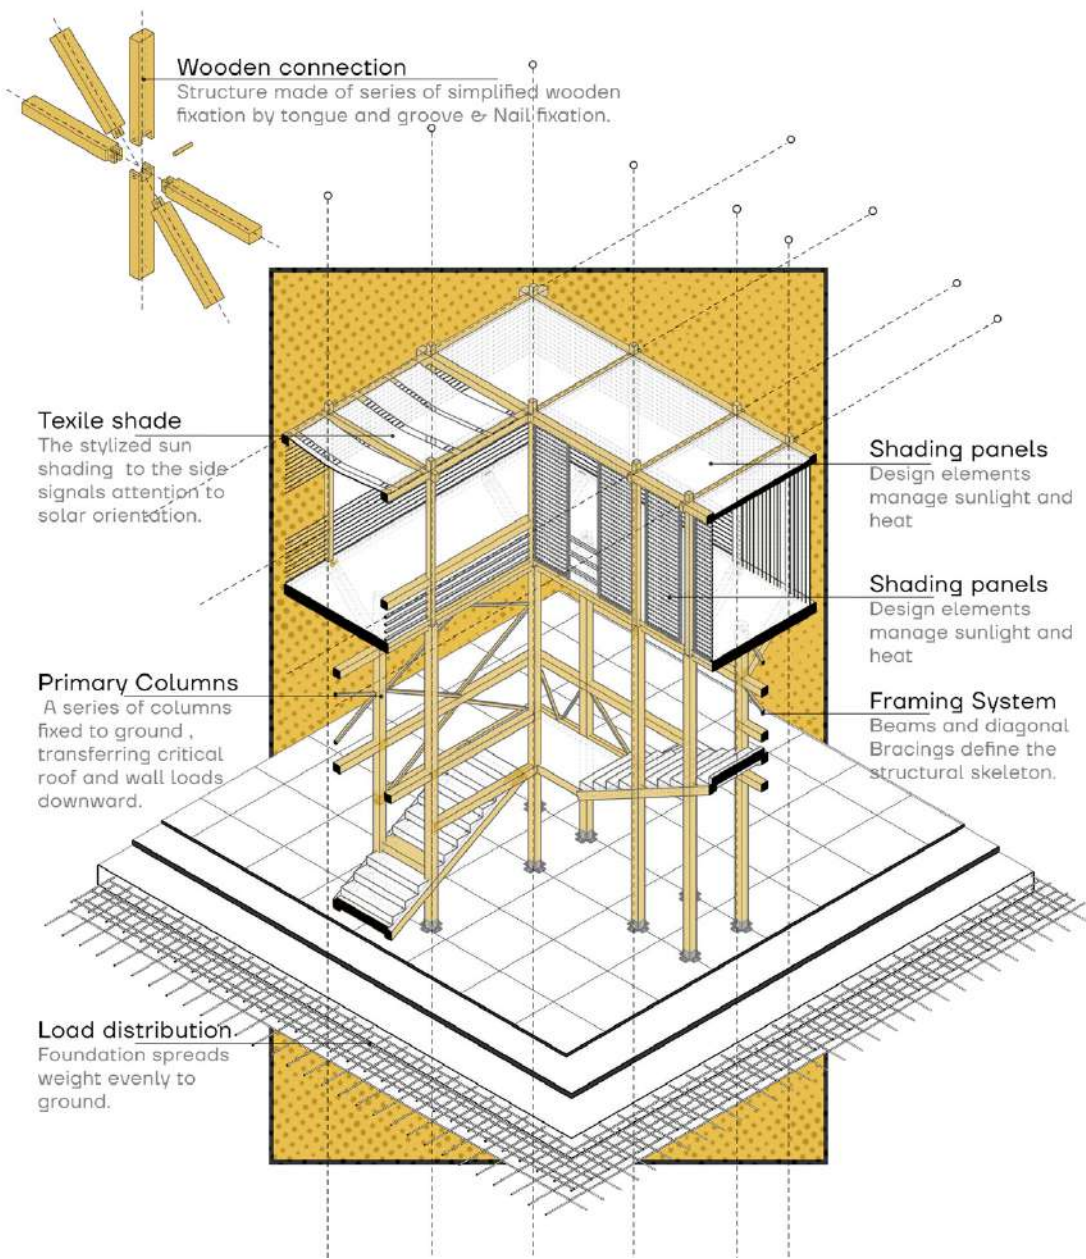

FORM GENERATION

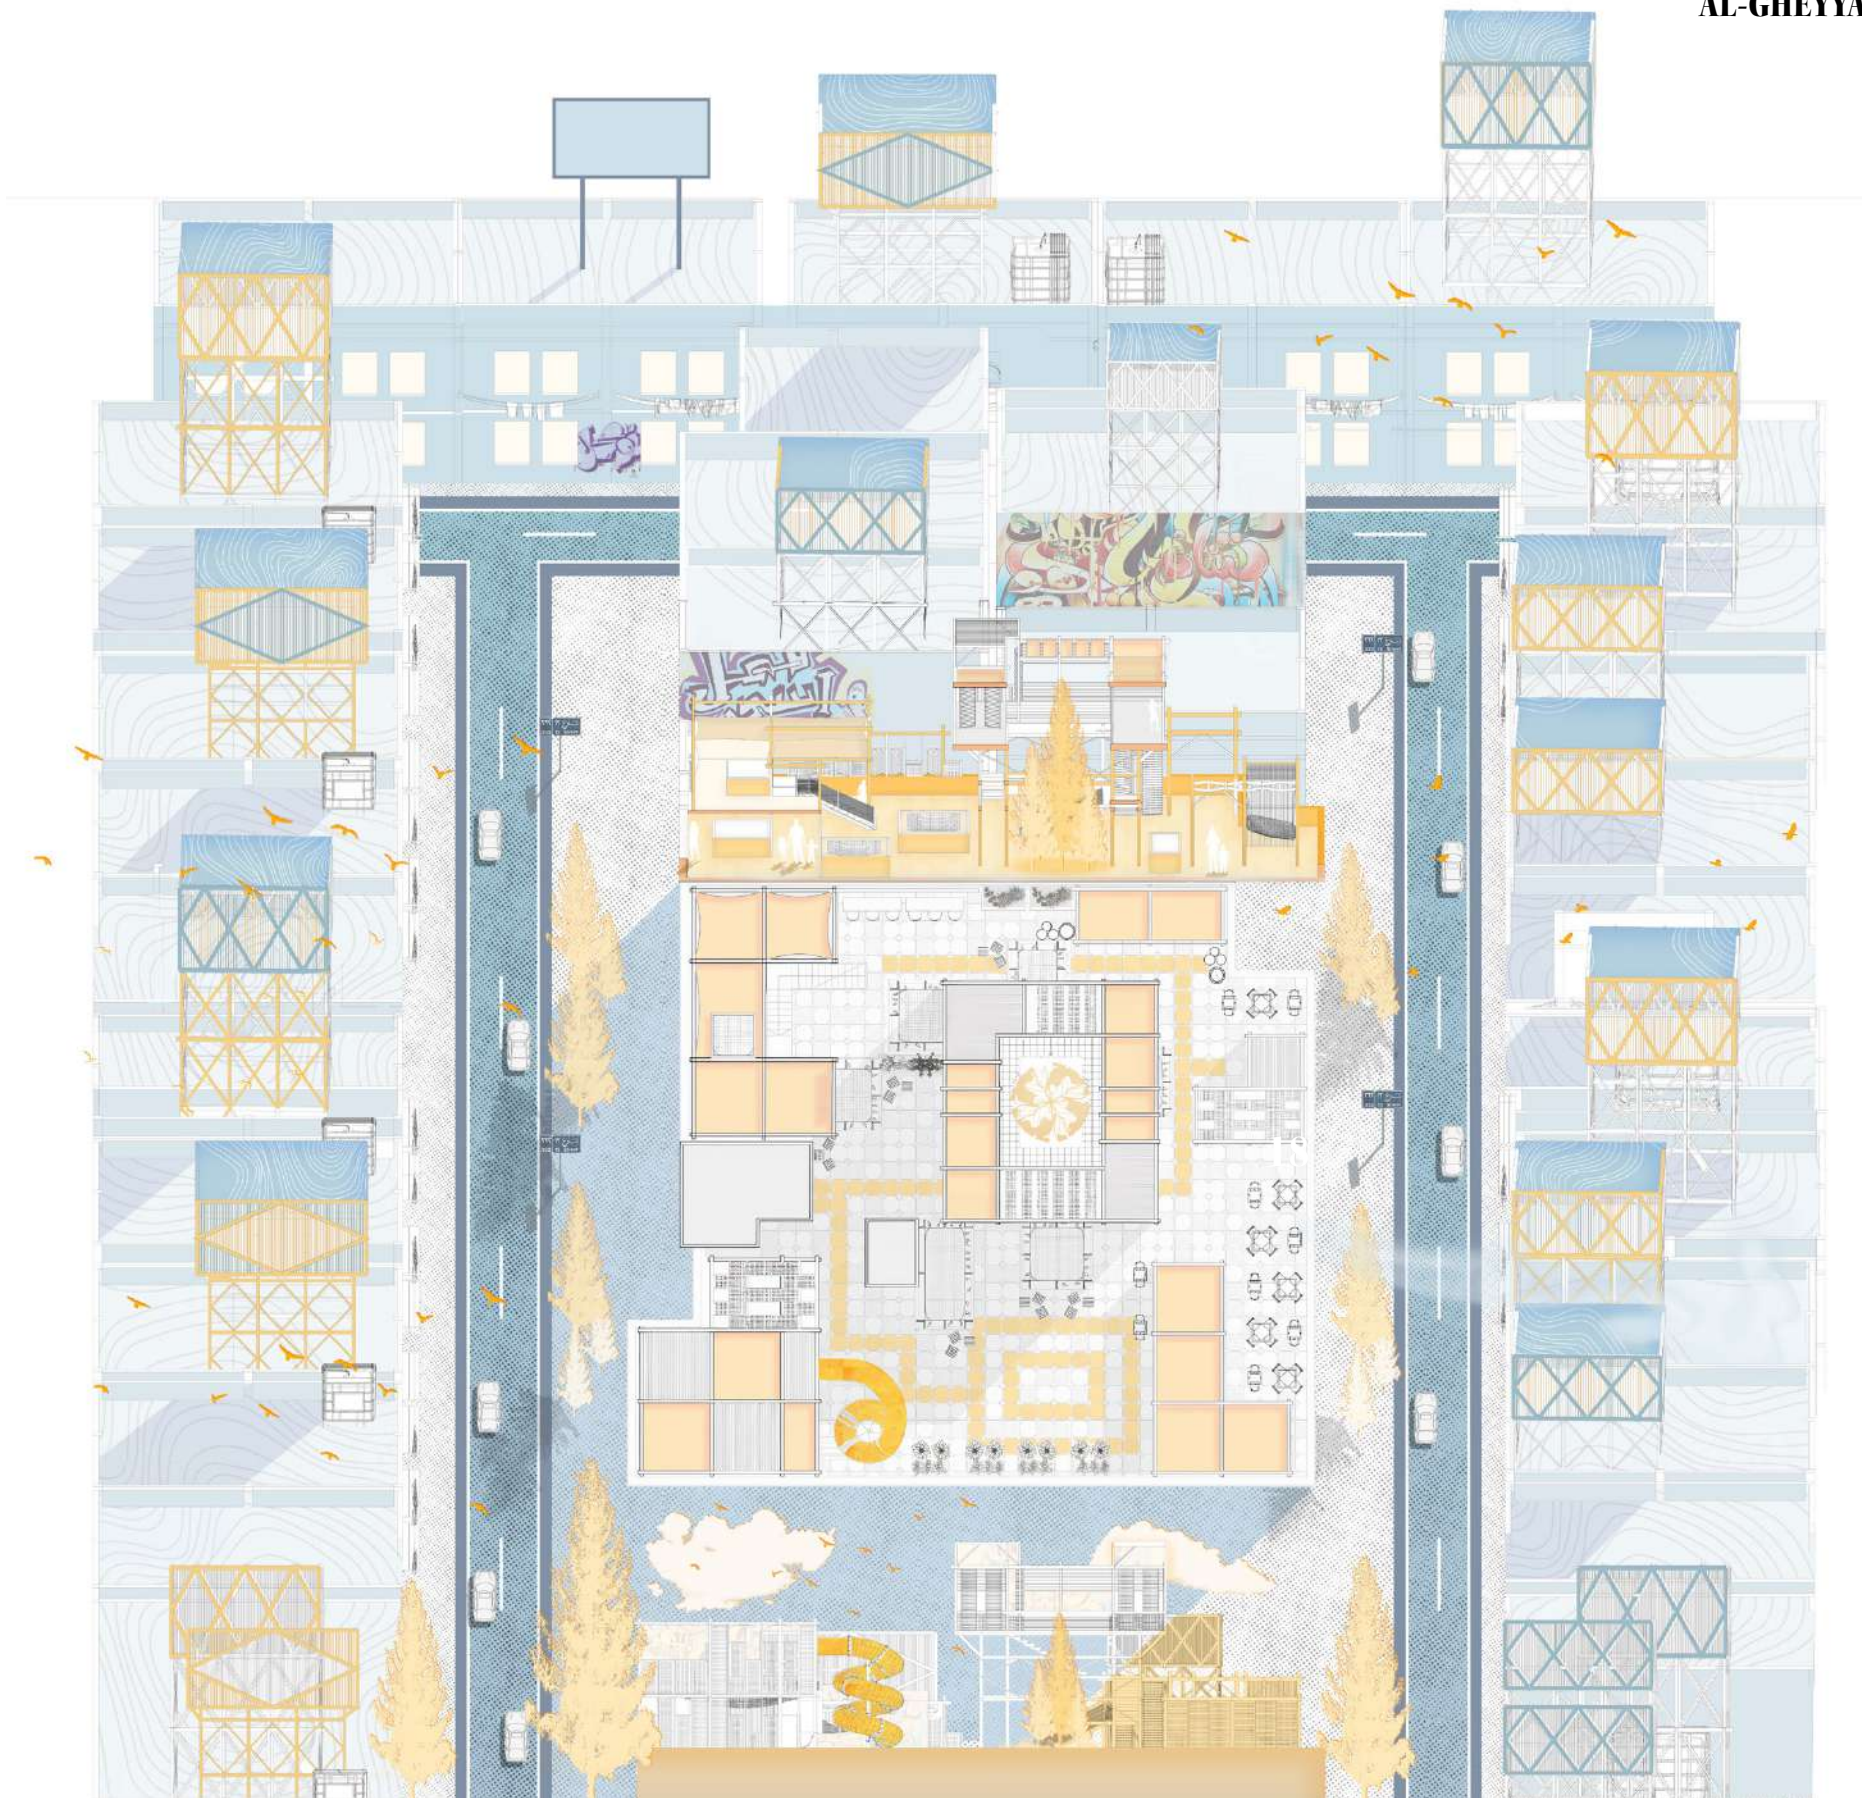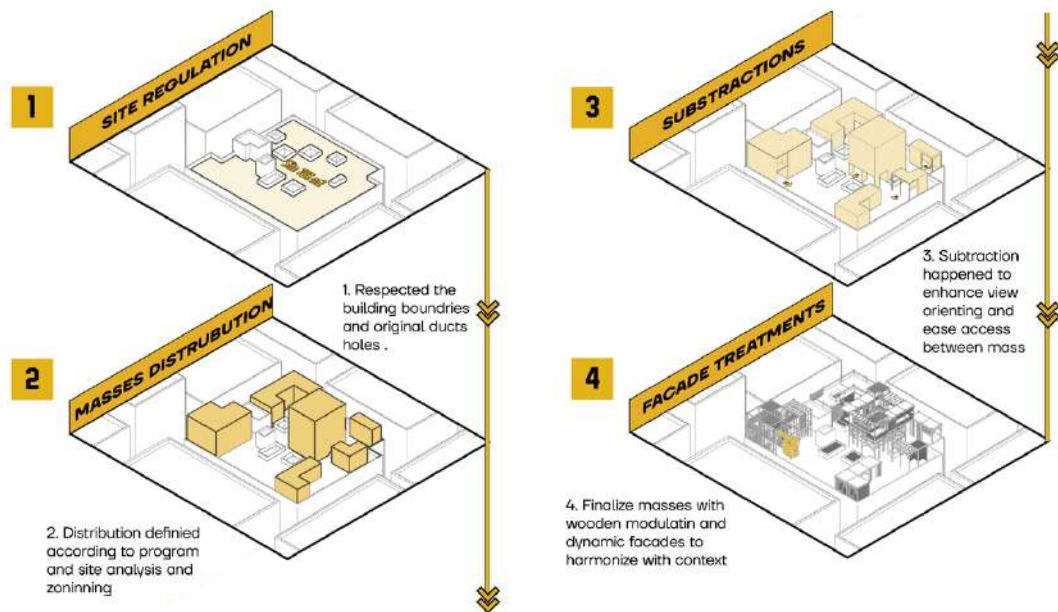

At its heart rises a central Observatory Tower, offering panoramic views of Cairo's majestic skyline and facilitating unique vertical social interaction. This dynamic rooftop realm unfolds with diverse zones: Peripheral seating overlooks the street life below; a Communal Cafeteria serves traditional refreshments and hosts table games; a Crafts Pavilion showcases local artisans and startups; a Quiet Reading/Workshop Area provides infused serenity; and a Safe, lively Children's Zone encourages play. Crucially, a Flexible Open Space accommodates spontaneous gatherings, celebrations, and cultural events.

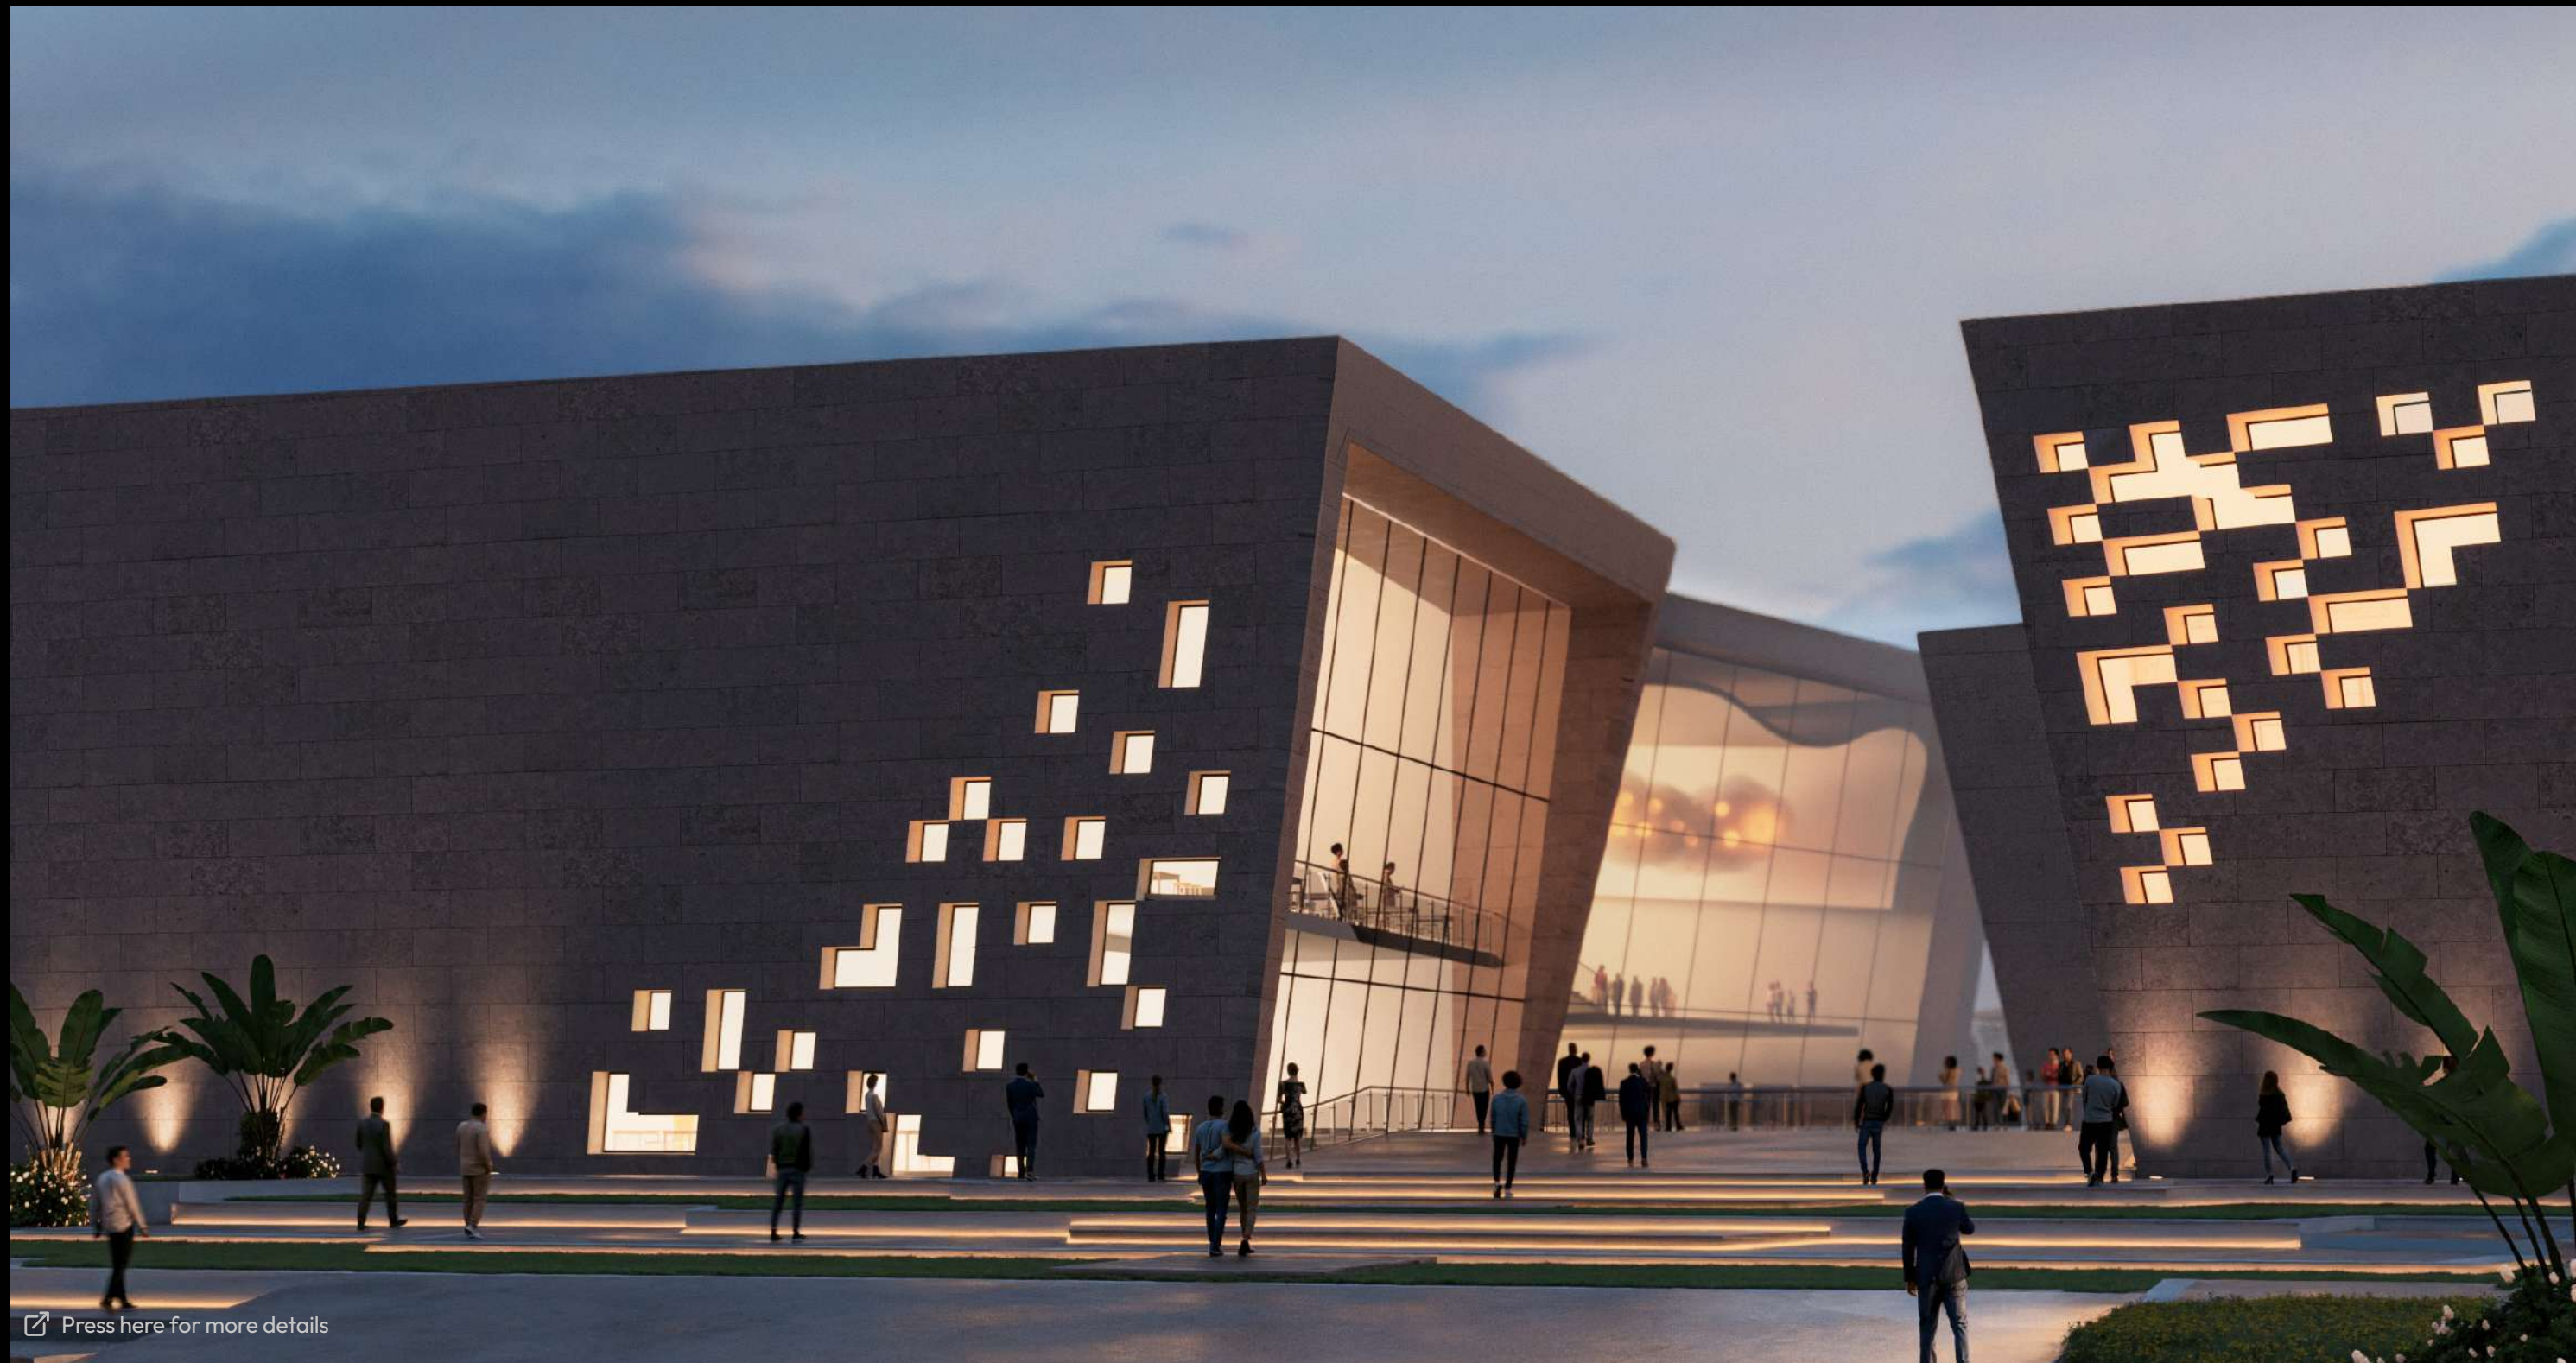

5

WESAL

TOP 10 Tamayouz Award 24 Competition
DEWAN AWARD FOR ARCHITECTURE

Year: 2024

Location: Baghdad, Iraq

Project: Pavilion

Softwares: 3Ds Max, Corona, Photoshop, Illustrator


CONCEPT

Our vibrant city was defined by its unique circular layout, where a vibrant energy at its center captivated everyone around it, inviting them into its comforting presence

This project concepts the old forgotten image. Featuring a garden court symbolize the symphony of movement & presence of the project, surrounded by four resembled blocks that define its enclosure



Role: (Teamwork)

-Workin on Design, Modeling and Visualization

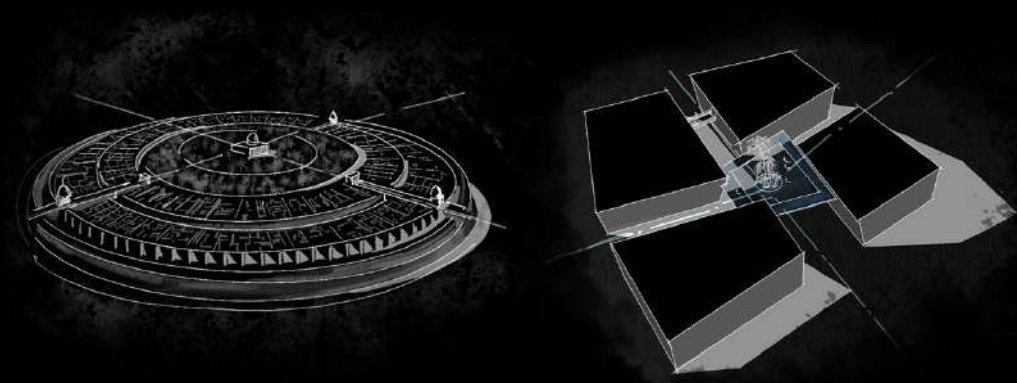


CONCEPT


Our vibrant city was defined by its unique circular layout, where a vibrant energy at its center captivated everyone around it, inviting them into its comforting presence
This project concepts the old forgotten image. Featuring a garden court symbolize the symphony of movement & presence of the project, surrounded by four resembled blocks that define its enclosure

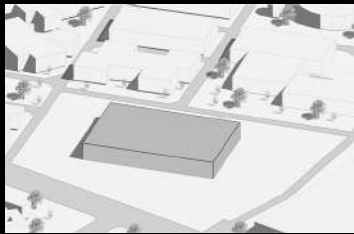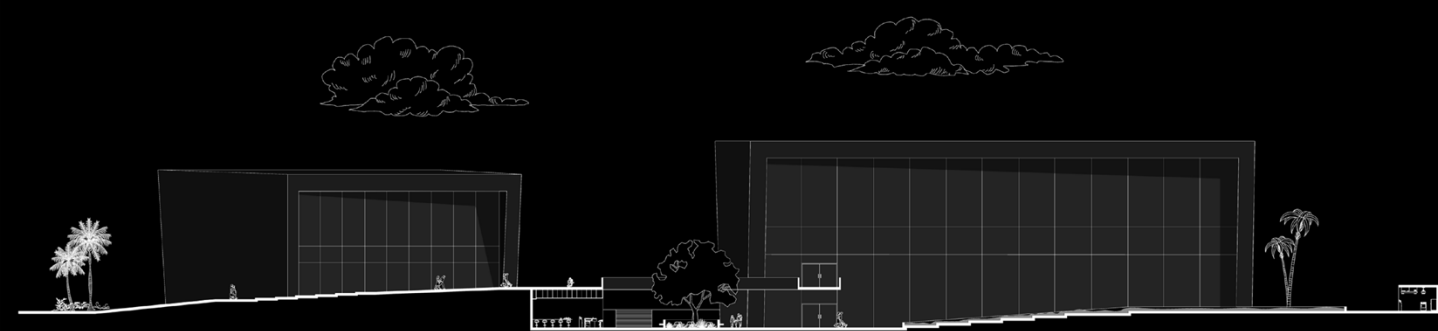

1.Build up area

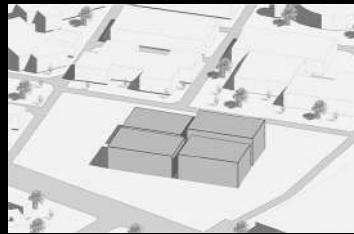


2.Divide masses into 4 masses

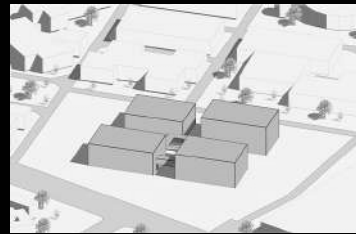


3.Enclosing masses around Central Court



4.Adjust Masses lines based on site and tilt the walls

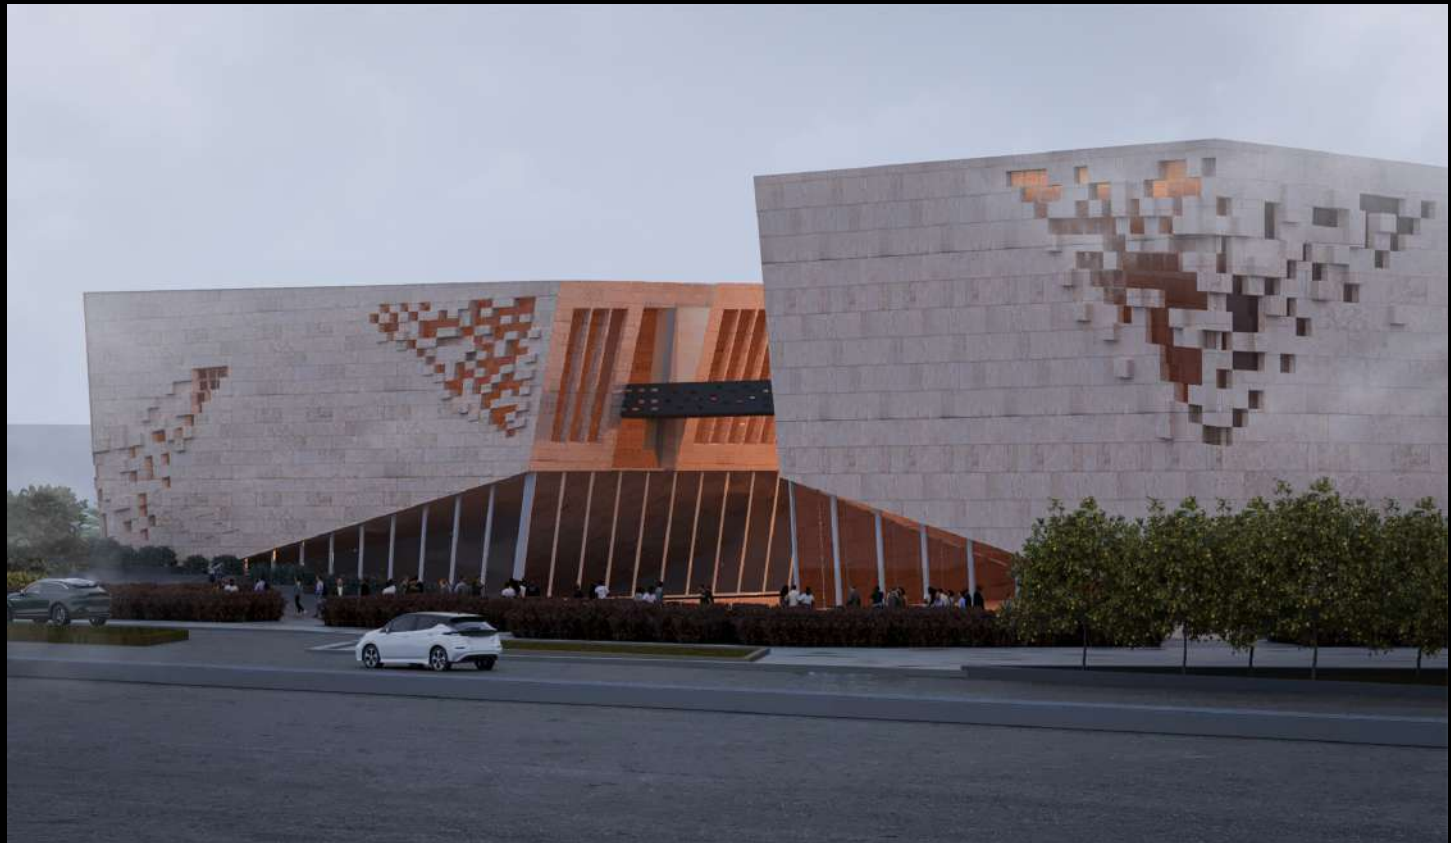


Layout

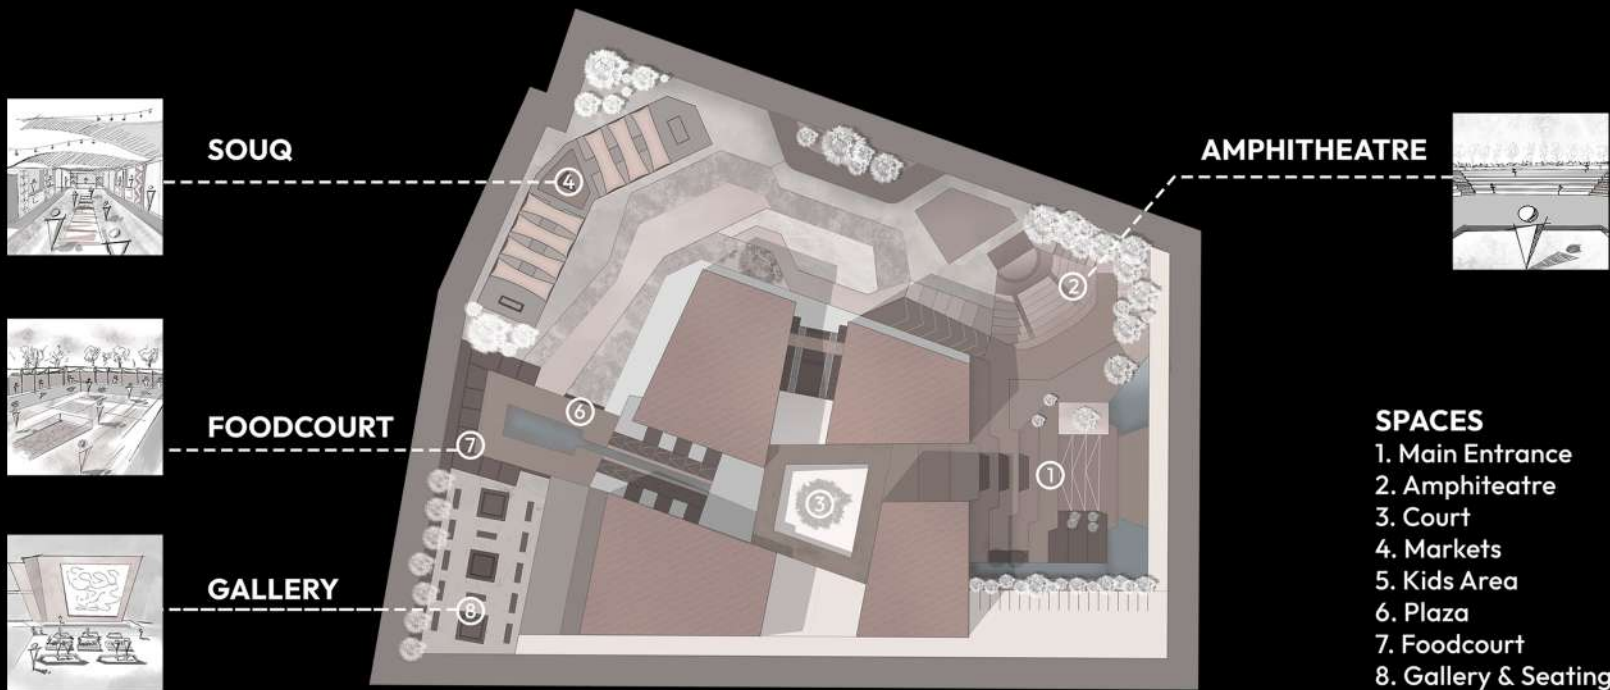


- SPACES**
- 1. Main Entrance
 - 2. Amphitheatre
 - 3. Court
 - 4. Markets
 - 5. Kids Area
 - 6. Plaza
 - 7. Foodcourt
 - 8. Gallery & Seating


Enviromental Analysis

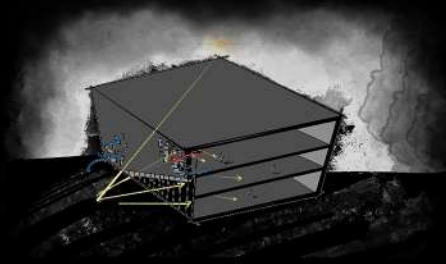


Double skin facades enhance energy efficiency by providing insulation and reducing heat gain

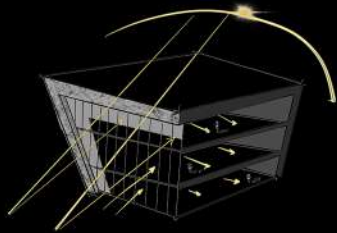

Reveal in facdes allowing natural daylight without solar heat

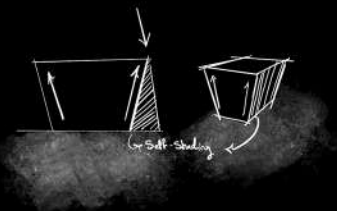


Self-shading masses minimize direct sunlight exposure

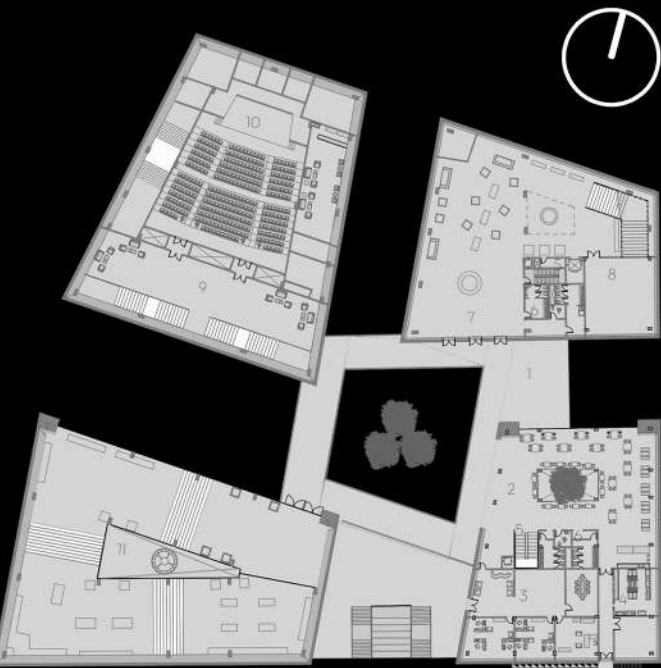


Ground Plan

- 1. Main Entrance
- 2. Foodcourt
- 3. Offices
- 4. Kitchen
- 5. Vertical Circulation
- 6. Toilets
- 7. Hall A

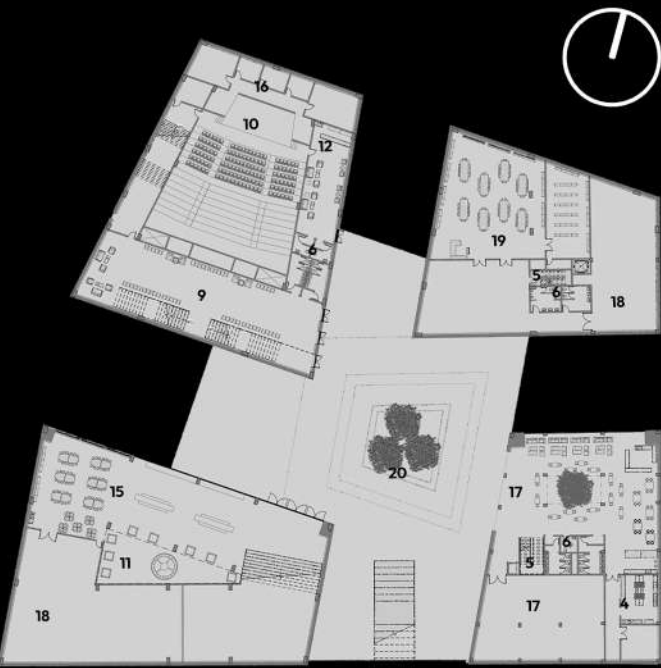

Basement plan

- 15. Worjshop
- 16. Backstage
- 17. Cafetria
- 18. Storage
- 19. Library
- 20. Court

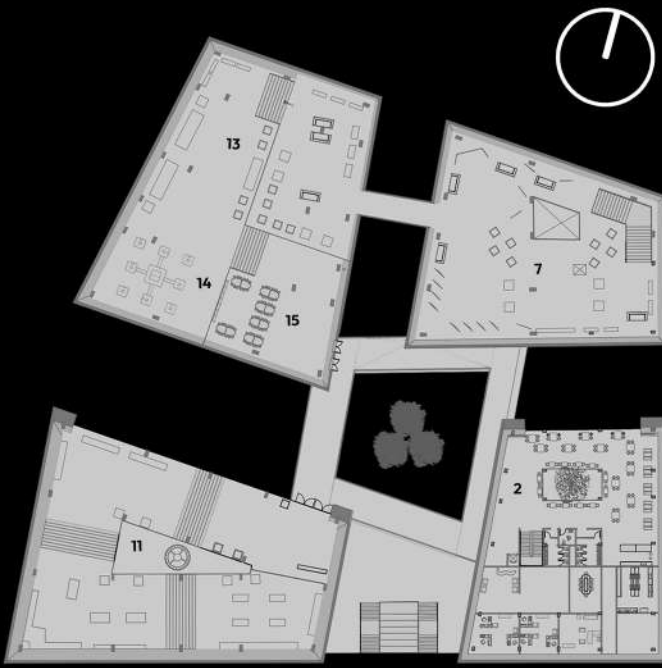

First plan

- 8. Immersive Seminar
- 9. Foyer
- 10. Auditorium
- 11. Hall C
- 12. VIP
- 13. Hall B
- 14. VR Station



6

THE FLUX

ACADEMIC WORK

INTERIOR DESIGN AND ERGONOMICS STUDIO

Ain Shams University, Faculty of Engineering

Year: 2026

Location: Ain Shams University, Egypt

Project: Re-designing the drawing hall


Softwares: Rhino, Grasshoper, Corona, Photoshop

BRIEF

The project reimagines the Drawing Hall at Ain Shams University's Faculty of Engineering. The design transforms a conventional educational space into a dynamic environment where movement, light, and spatial continuity flow seamlessly. By embracing fluid geometries and interconnected volumes, THE FLUX fosters creativity, interaction, and adaptability, turning the act of drawing and learning into an immersive and evolving experience.

Role: (Teamwork)

-Workin on Design, Modelling and Visualization



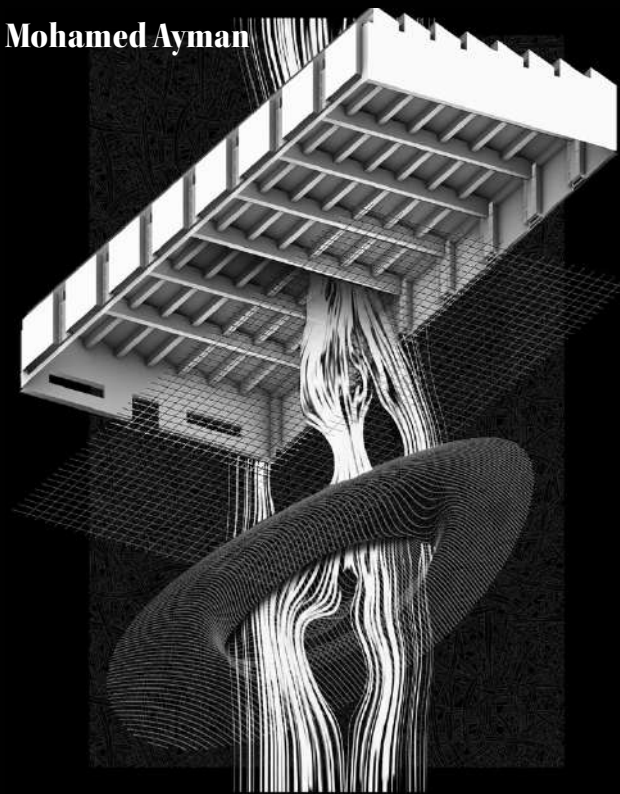


LIBERATING THE RIGID

A fixed structure dissolves into flowing forces, freeing space from past constraints, and opening new possibilities for spatial continuity and experience.




Post production using AI

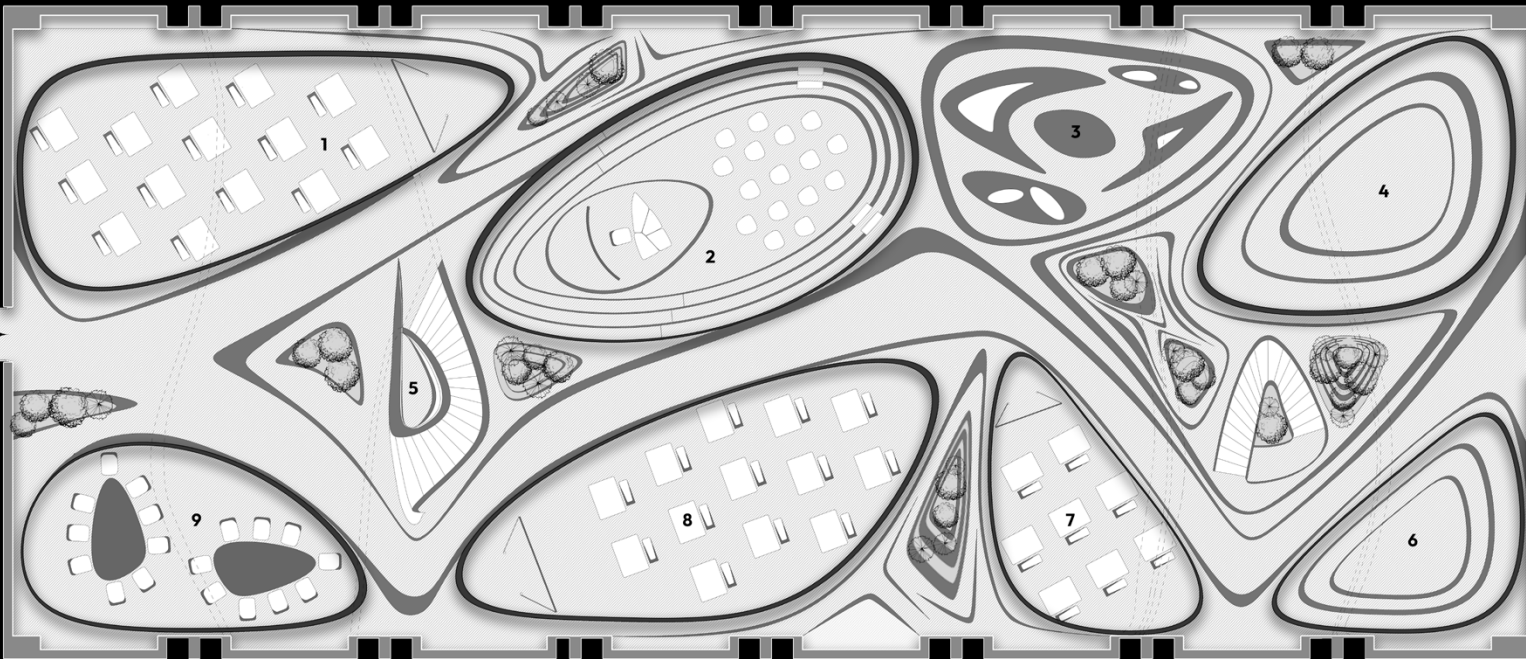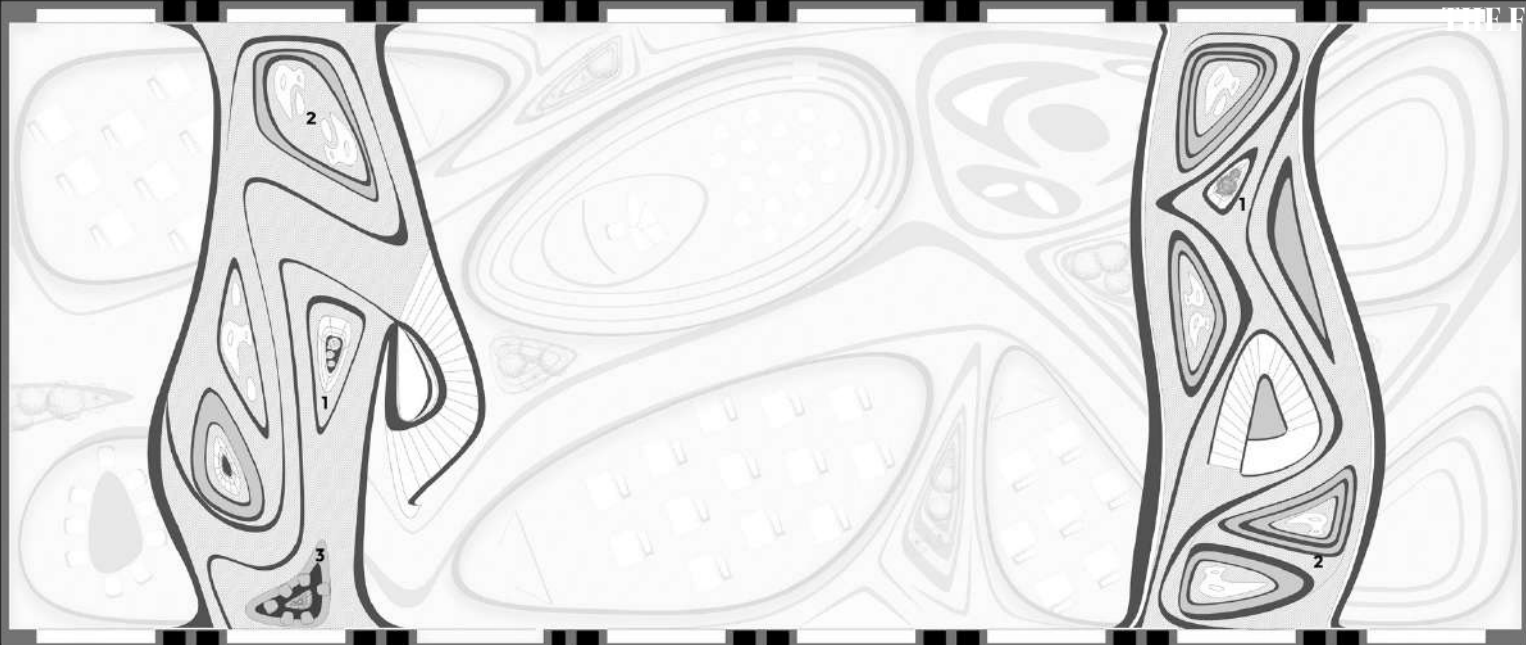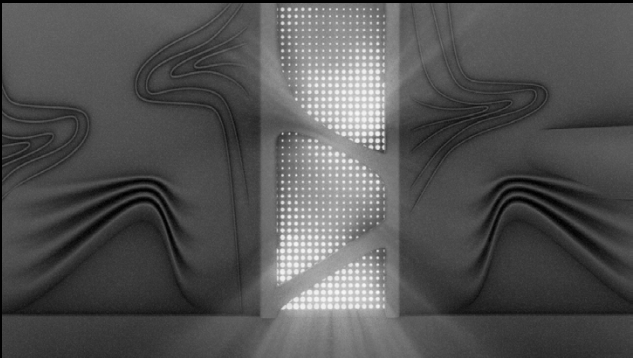


LEGEND
GROUND FLOOR


- 1. DRAWING ZONE
- 2. LECTURE HALL
- 3. GATHERING AREA
- 4. PHYSICAL MODEL ZONE
- 5. STAIR & COFFE CORNER
- 6. VR ZONE
- 7. DRAWING ZONE
- 8. DRAWING ZONE
- 9. MEETING ROOM

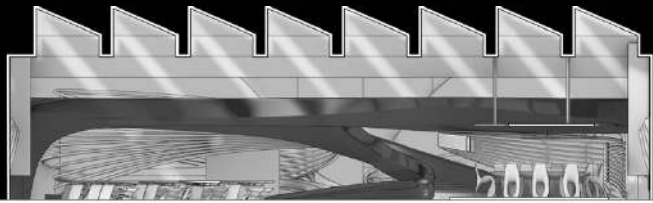

SECTION 1

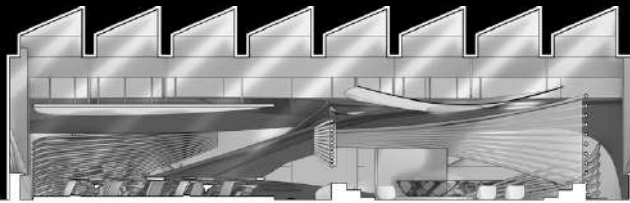

SECTION 2

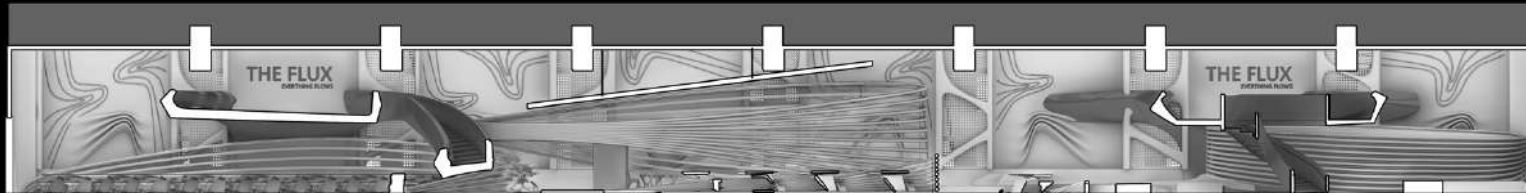

LONGITUDINAL SECTION



[Press here for more details](#)

7

THE CAUSTIC

FIRST Place, Beyond the tide Competition

SMART SYSTEM DESIGN STUDIO

Ain Shams University, Faculty of Engineering

SECOND Place, FLOATING HOUSES COMPETITION

World Architecture competition

Year: 2025

Location: Rashid, Egypt

Project: Smart chalets

Softwares: Rhino, Grasshoper, Corona, Photoshop

BRIEF

The project called for the innovative and sustainable design of a chalet capable of withstanding the challenges posed by rising water levels. This required a forward-thinking architectural approach that integrates resilient construction techniques with environmentally responsible materials and adaptive design strategies. The objective was not only to protect the structure from flooding and water-related damage but also to ensure long-term harmony with the surrounding ecosystem, setting a new benchmark for climate-resilient waterfront living.

Role: (Teamwork)

-Workin on Design and Visualization


CONCEPT


We proposed a chalet concept combines adaptive engineering and sensory immersion, addressing water level rise challenges with a hinged rail mechanism for vertical & Horizontality mobility. The chalets feature water elements, generating dynamic light patterns, and are envisioned as ‘shimmering pearls’, promoting sustainable shelters and immersive sensory retreats.




FORM GENERATION

- 

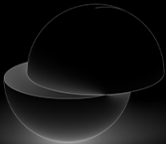
1. A basic sphere for footprint
- 

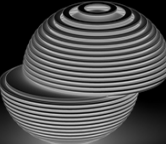2. Simple shift to richen the experince
- 


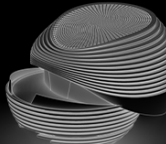
3. Circular rings to preform caustic effect
- 

4. Adding dynamic roof and finalizing mass.



RAILING DETAILS

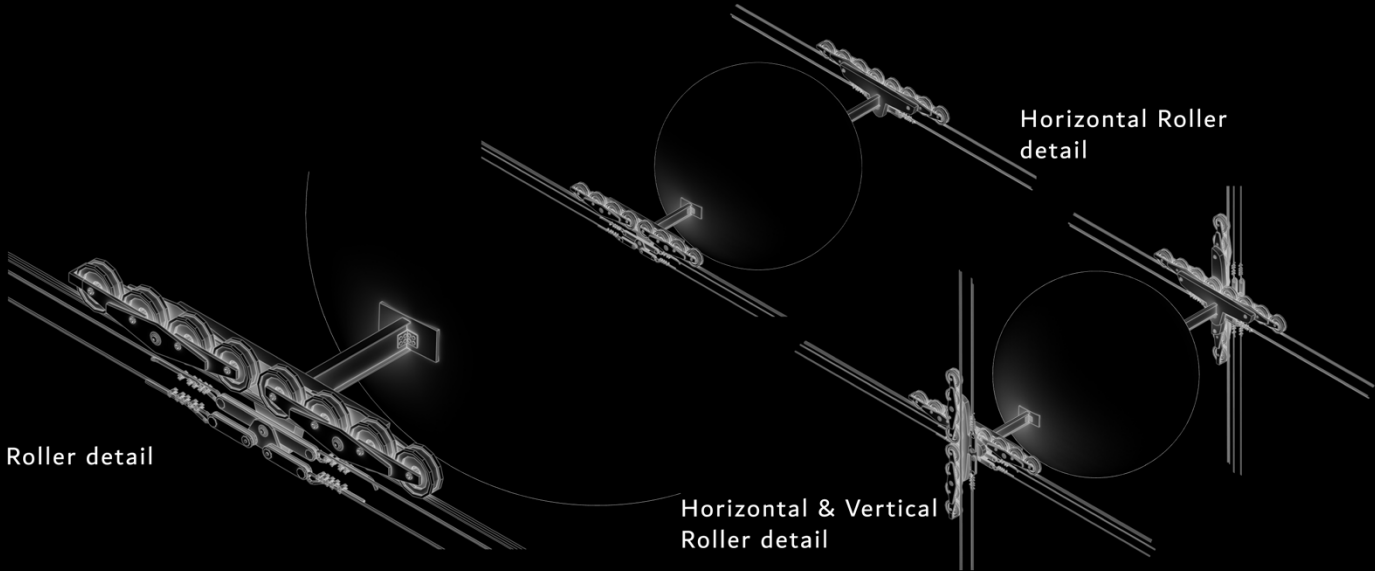

STRUCTURAL ANALYSIS

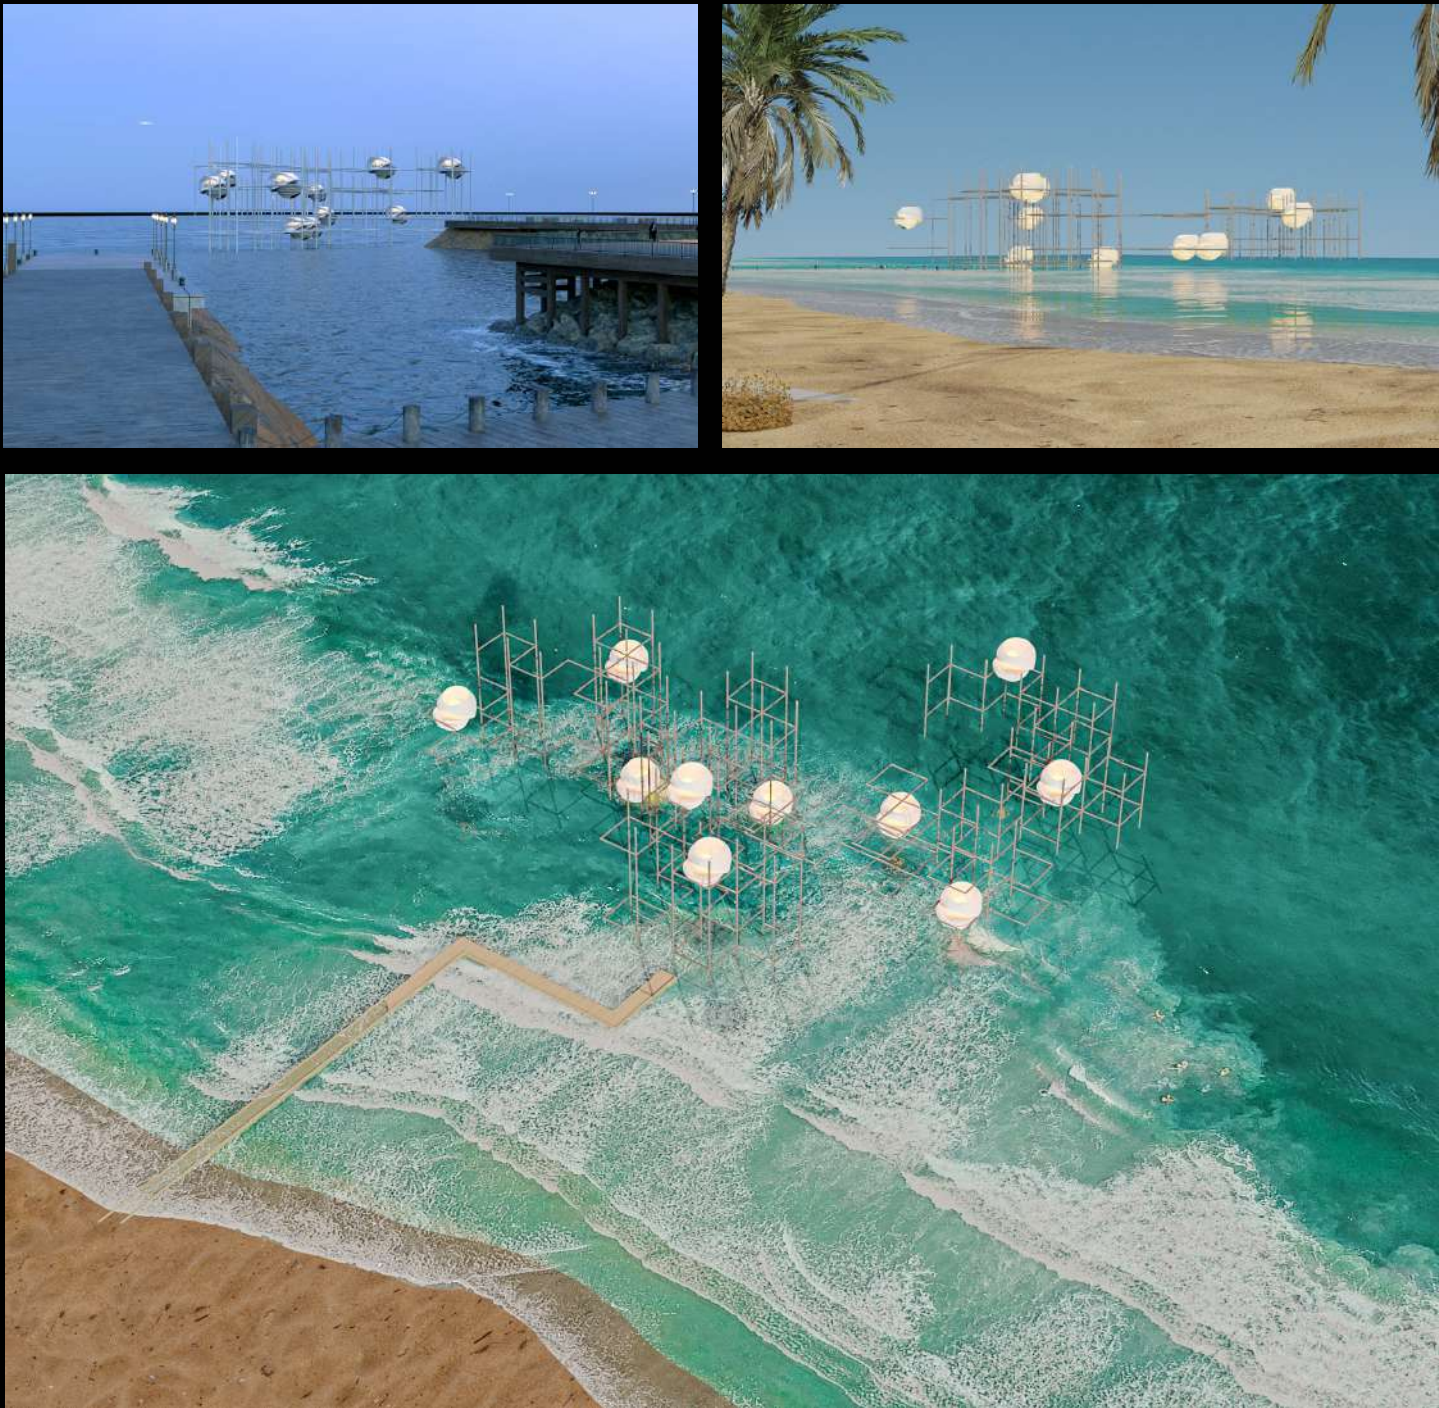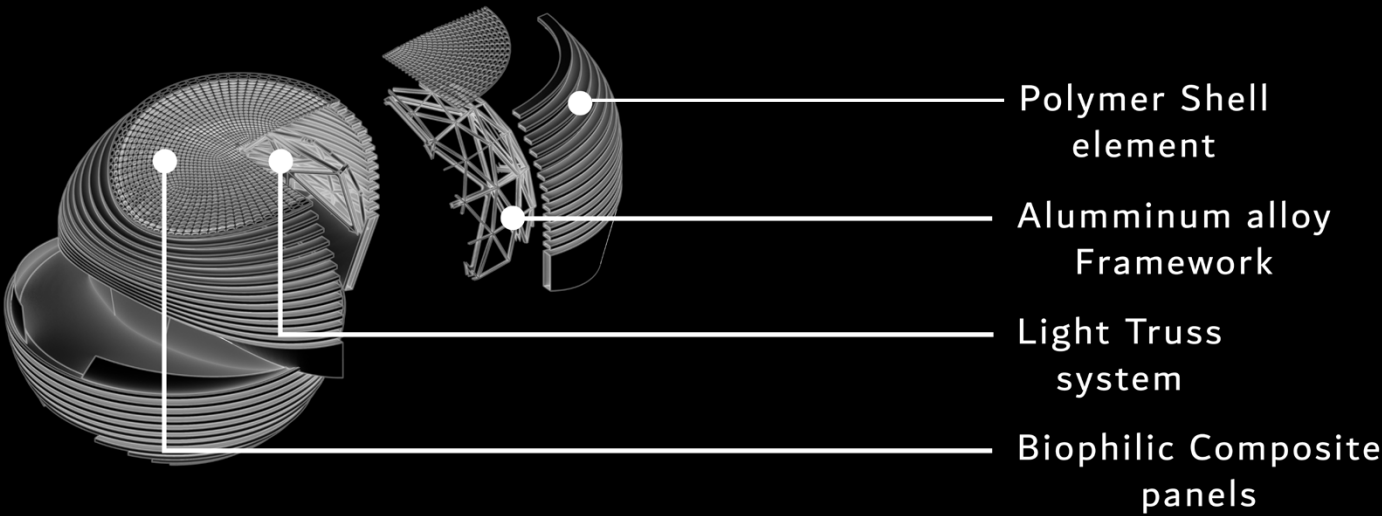


ARCHITECTURAL DRAWINGS

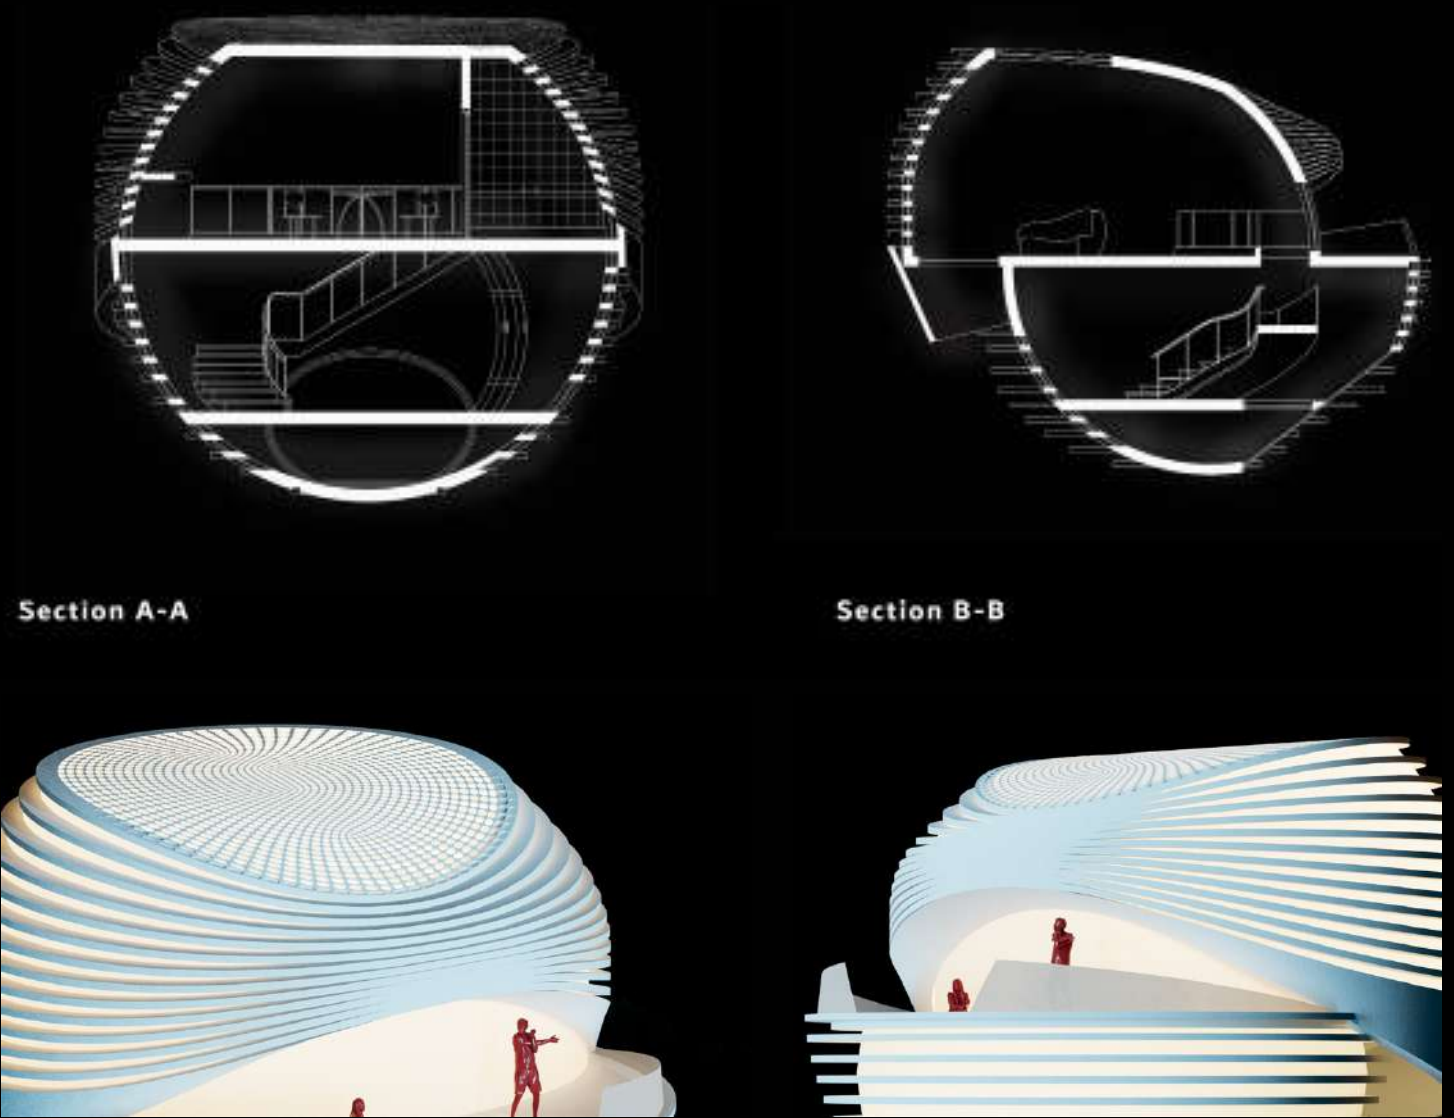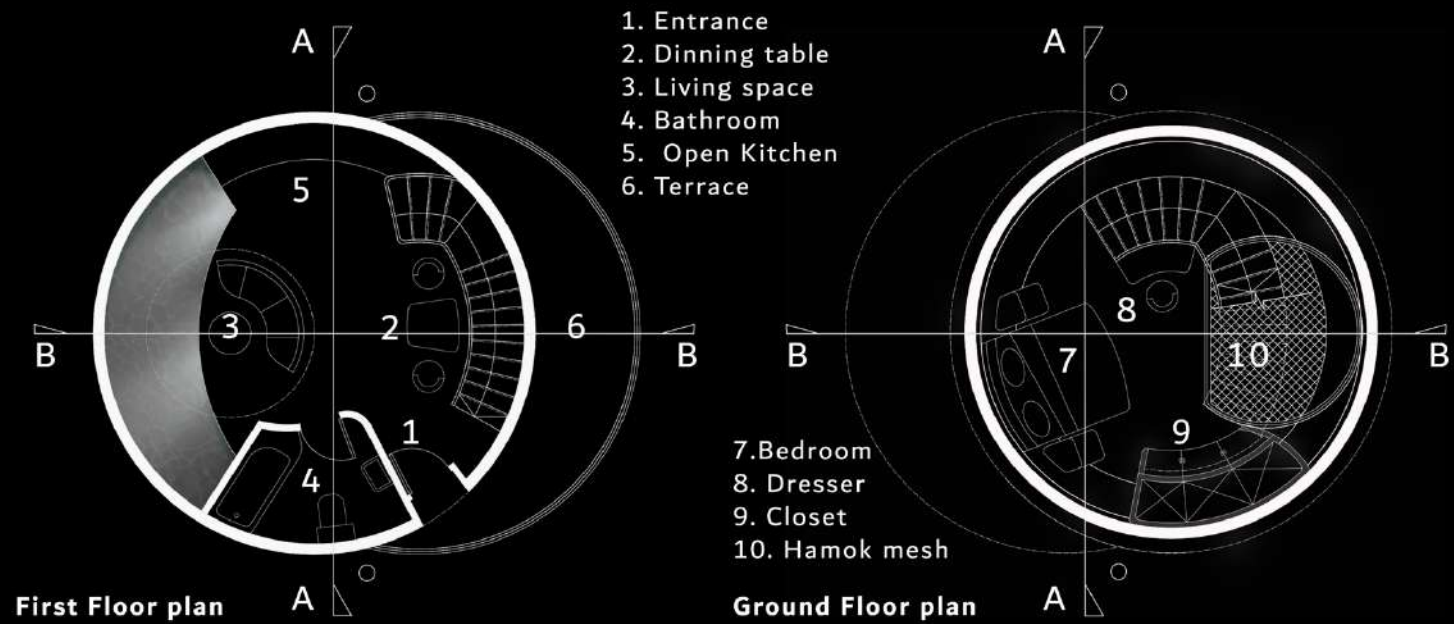

MODULATION

By transforming water caustics into fractal patterns, we harness the complexity of fractals for innovative engineering and future expansions. Using the dragon curve, we redefine spaces between modules to create dynamic gathering areas that enhance community interaction.

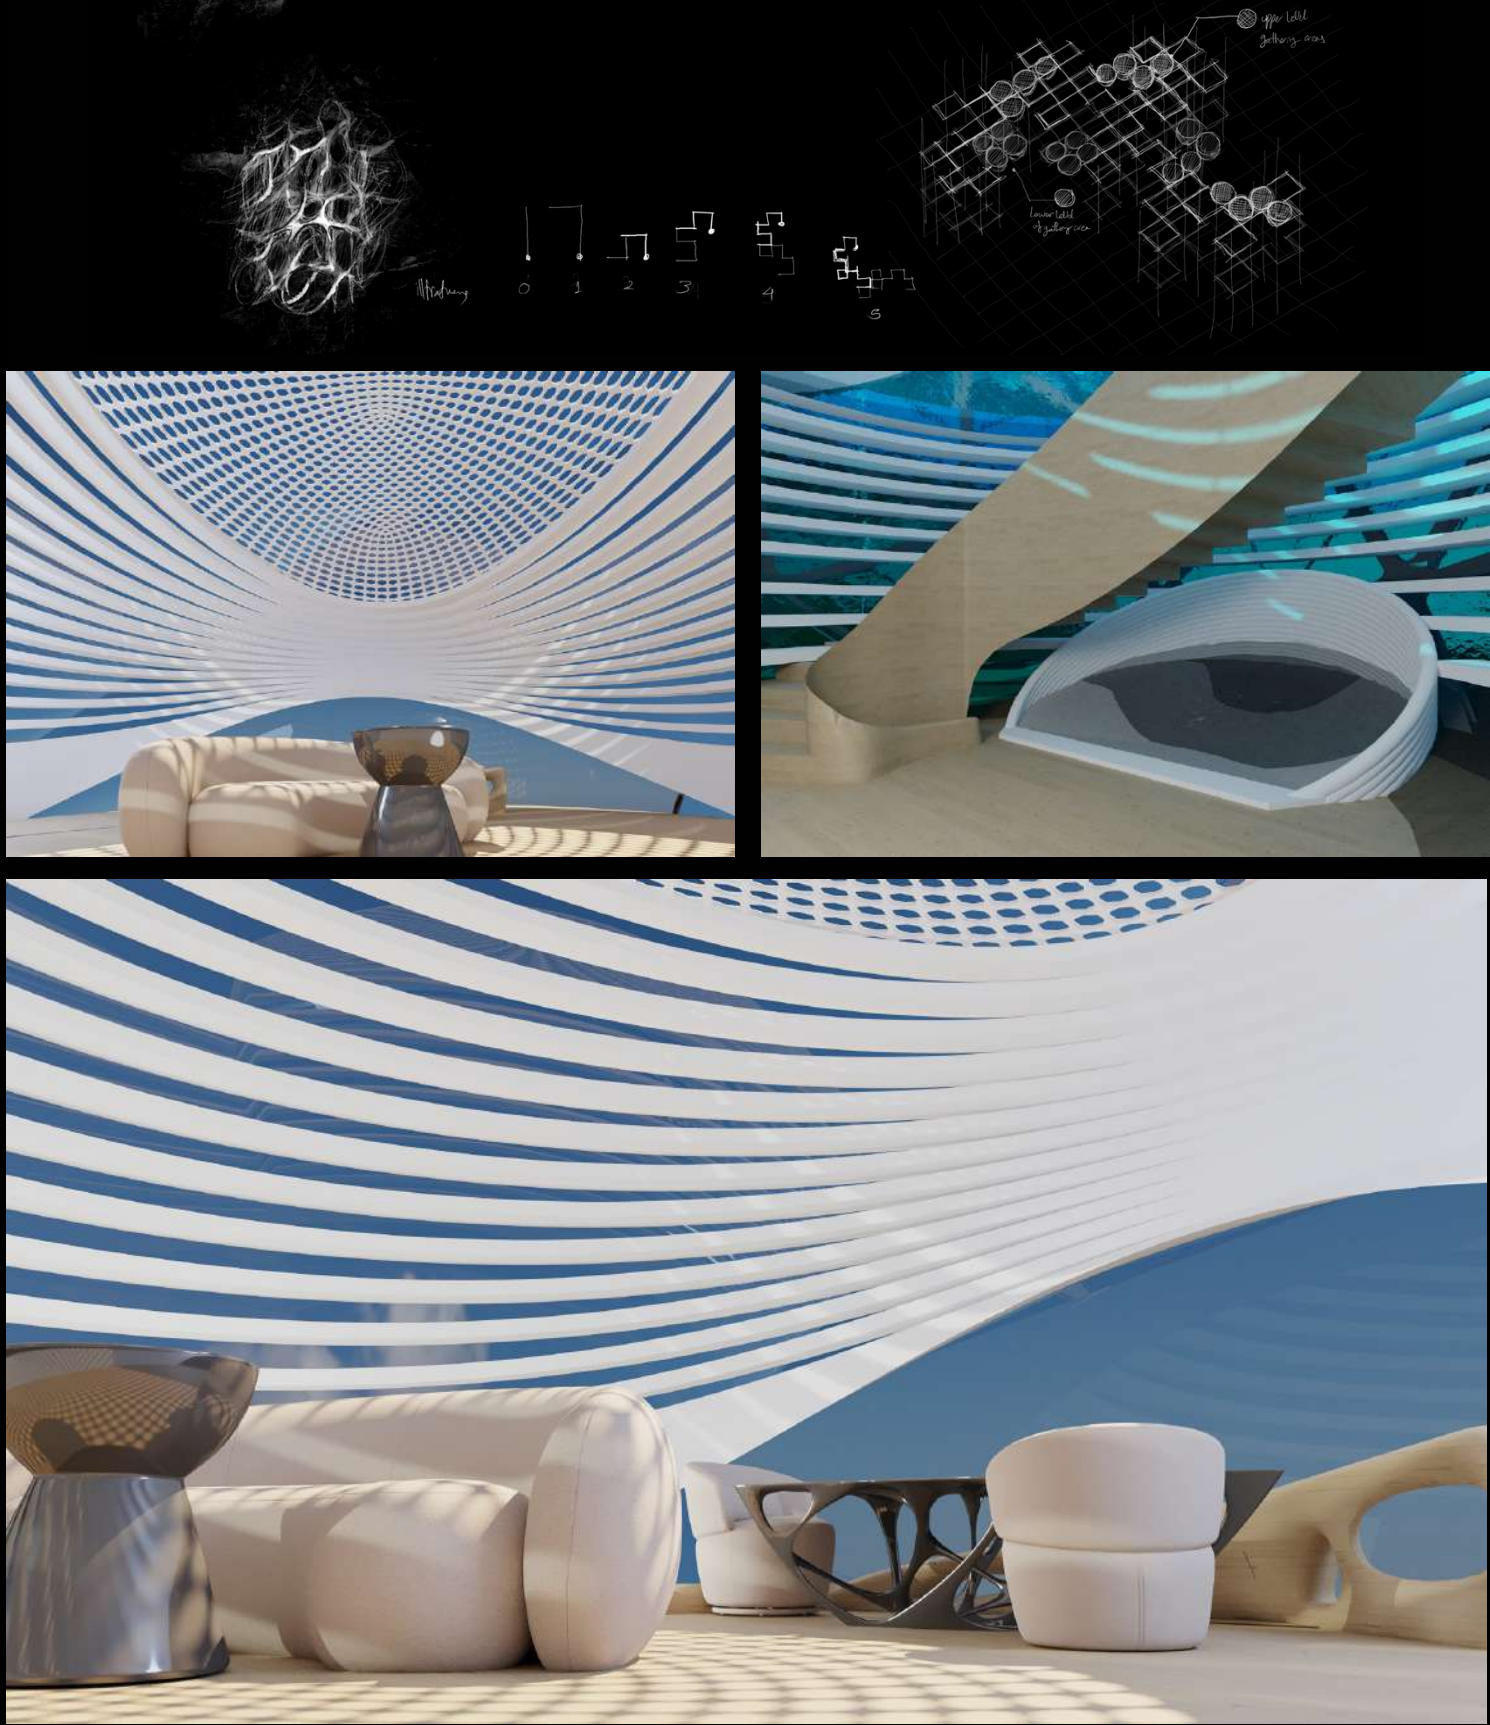



8

EHYAA

2nd term, 2nd year, Ain-shams School of Architecture
Course: Context and place design studio

Year: 2024

Location: Gouna, Redsea, Egypt

Project: Community center



Softwares: Revit, Lumion, Photoshop

CONCEPT

Inspired from our context El-Gouna that integrates between the natural and the building, so we designed the building to be: integrated with the natural, so we made the urban space contained with the building and seeing the view with natural ventilation natural, low energy consumption.



SCENARIO

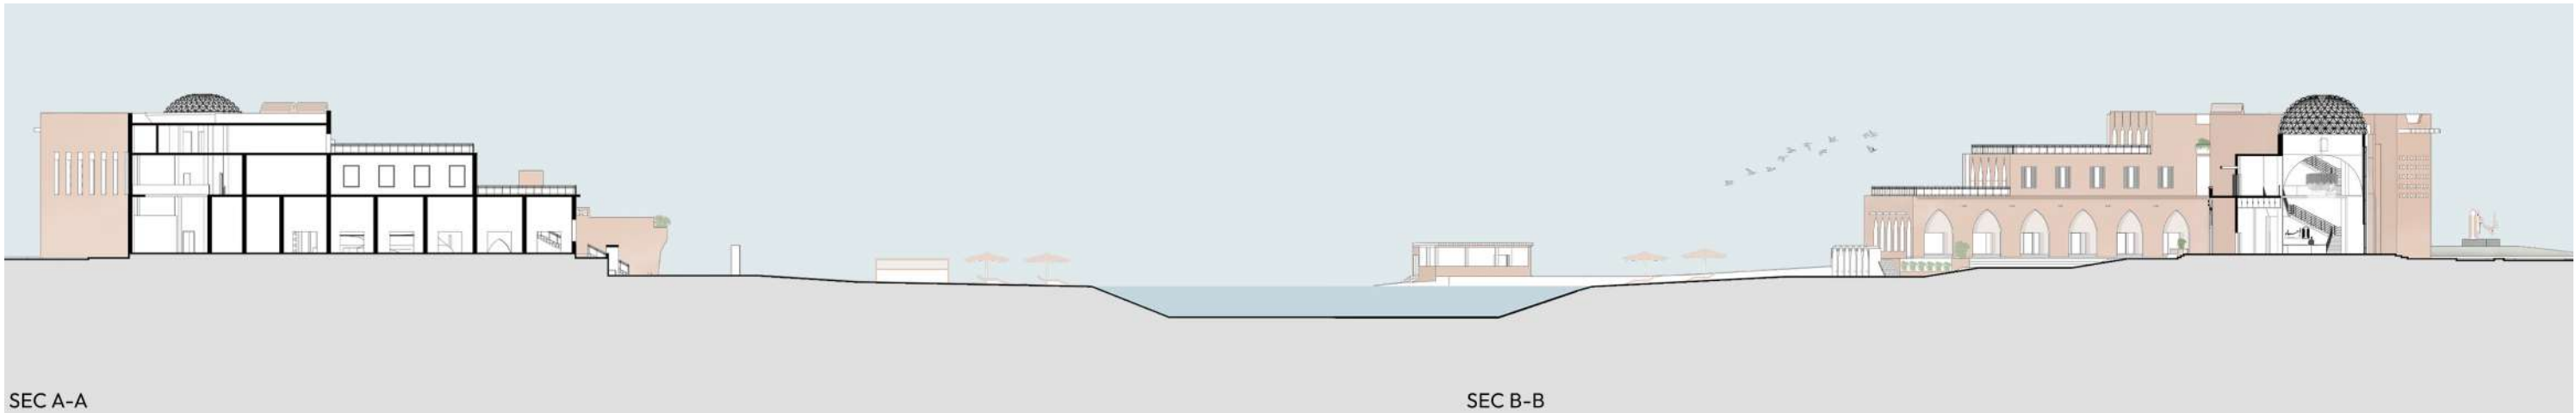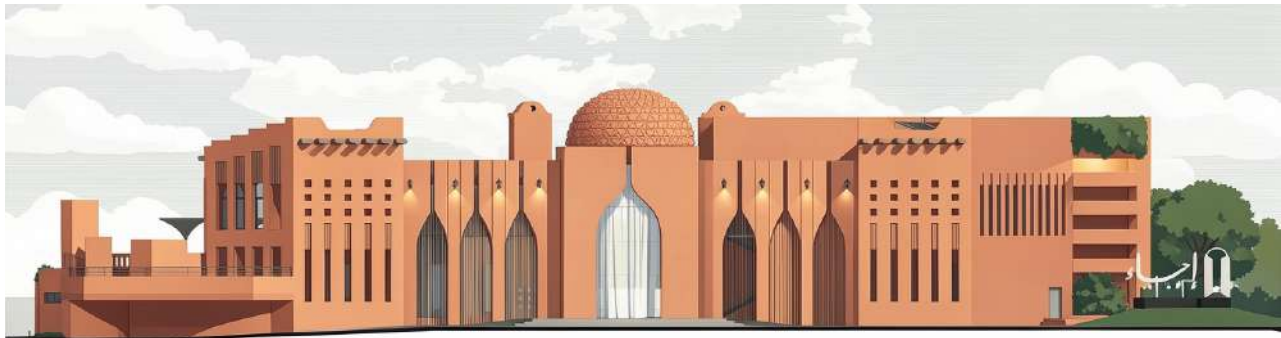


SEC A-A

SEC B-B

MASTER PLAN





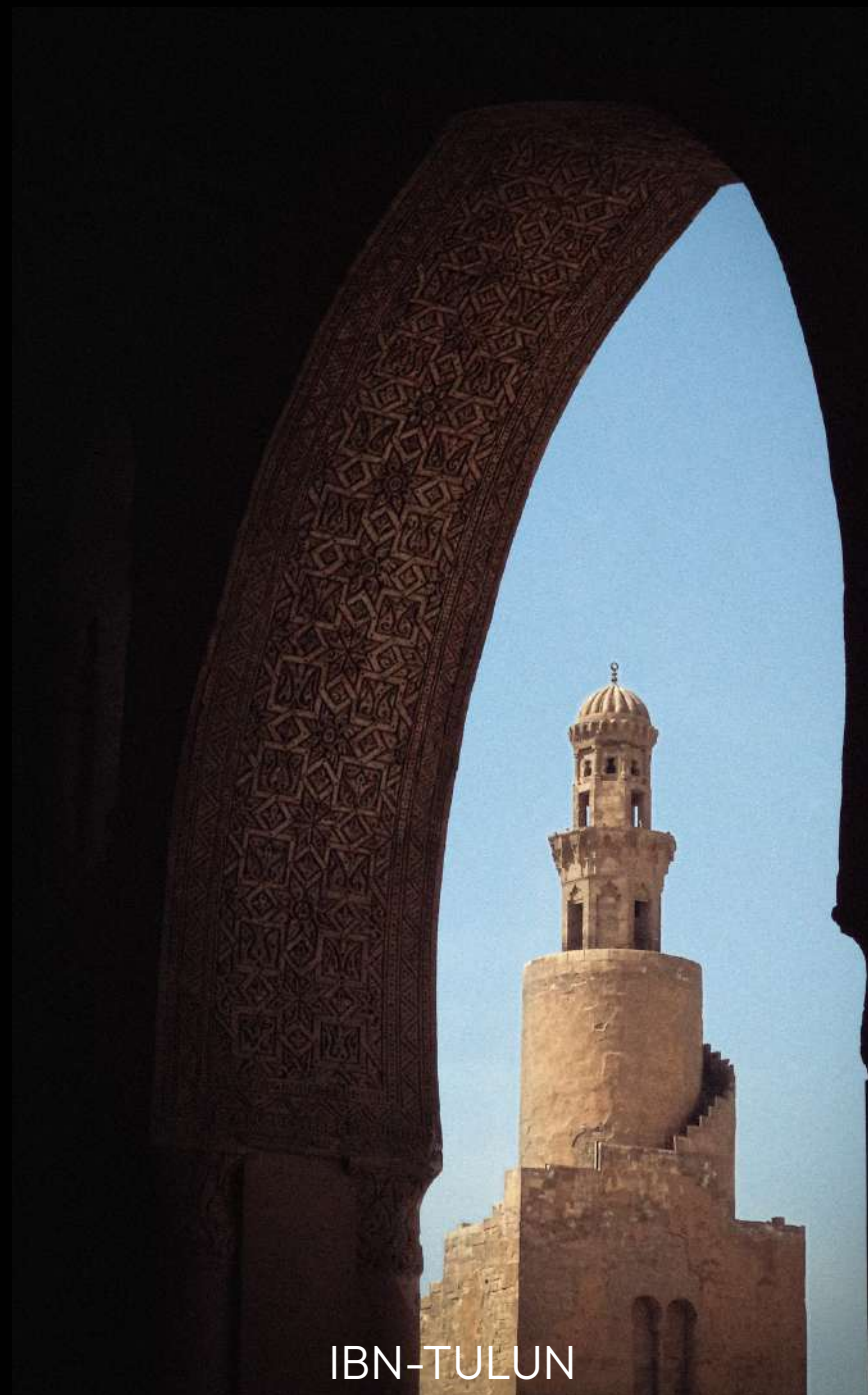

IBN-TULUN



AL-MU'IZZ



AL-SAKAKINI PALACE

A Journey of Discovery

Beyond my passion for architecture, I find joy in walking and exploring the streets, immersing myself in the rhythm of urban life. This curiosity led me to photography, where I capture the hidden stories and fleeting moments that define a place.



CAIRO SKYLINE



AZHAR PARK

A Journey of Discovery

Beyond my passion for architecture, I find joy in walking and exploring the streets, immersing myself in the rhythm of urban life. This curiosity led me to photography, where I capture the hidden stories and fleeting moments that define a place.

Selected works (2023-2026)

Mohamed Ayman

Maadi, Cairo, Egypt
+20 01096107769
mohamed.yman1152003@gmail.com
www.linkedin.com/Mohamed Ayman